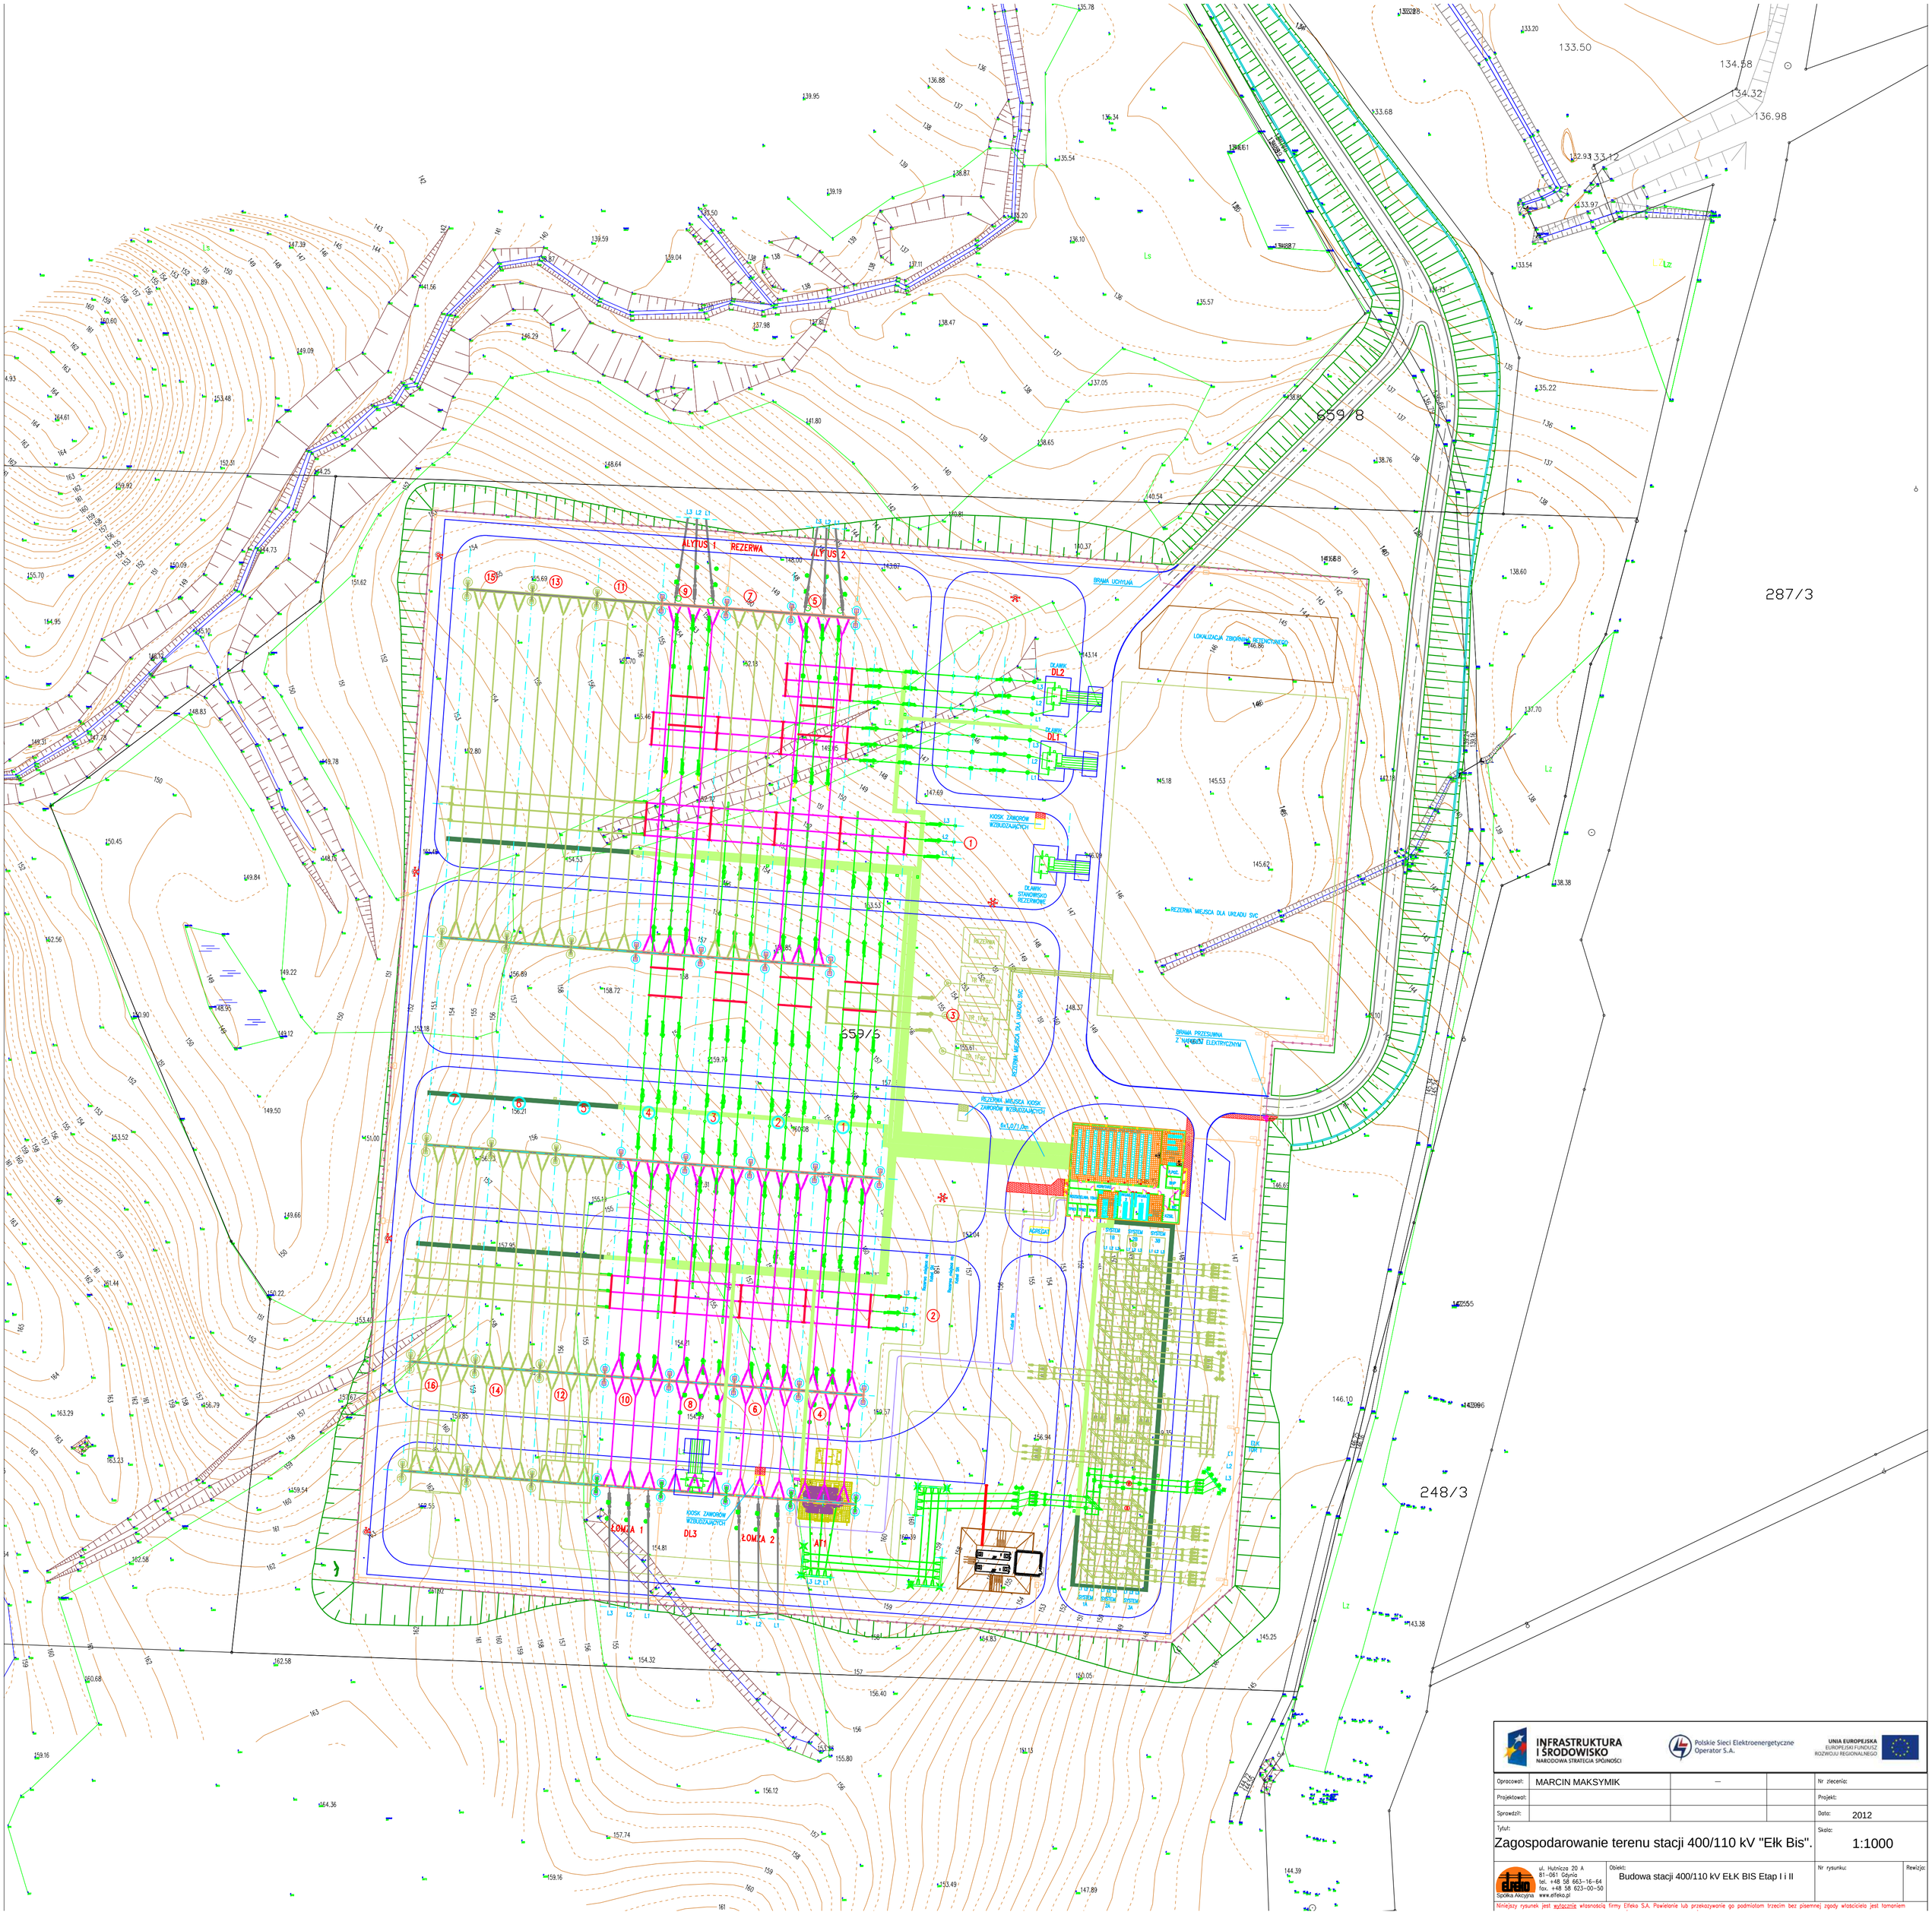

INFRASTRUKTURA I ŚRODOWISKO
NARODOWA STRATEGIA SPÓJNOŚCI

Polskie Sieci Elektroenergetyczne Operator S.A.

UNIA EUROPEJSKA
EUROPEJSKI FUNDUSZ ROZWOJU REGIONALNEGO

Opracował:	MARCIN MAKSYMIK	—		Nr zlecenia:
Projektował:				Projekt:
Sprawdził:				Data: 2012

Tytuł:

Zagospodarowanie terenu stacji 400/110 kV "Ełk Bis".

Skala: 1:1000

Spółka Akcyjna
ul. Hutnicza 20 A
81-061 Gdynia
tel. +48 58 663-16-64
fax. +48 58 623-00-50
www.eltelo.pl

Obiekt: Budowa stacji 400/110 kV EŁK BIS Etap I i II

Nr rysunku:

Rewizja:

Niniejszy rysunek jest wyłącznie własnością firmy Eltelo S.A. Powielanie lub przekazywanie go podmiotom trzecim bez pisemnej zgody właściciela jest tamarem