


THIS LAYOUT IS PRELIMINARY AND INDICATIVE ONLY, NOT FOR PLANNING OR CONSTRUCTION

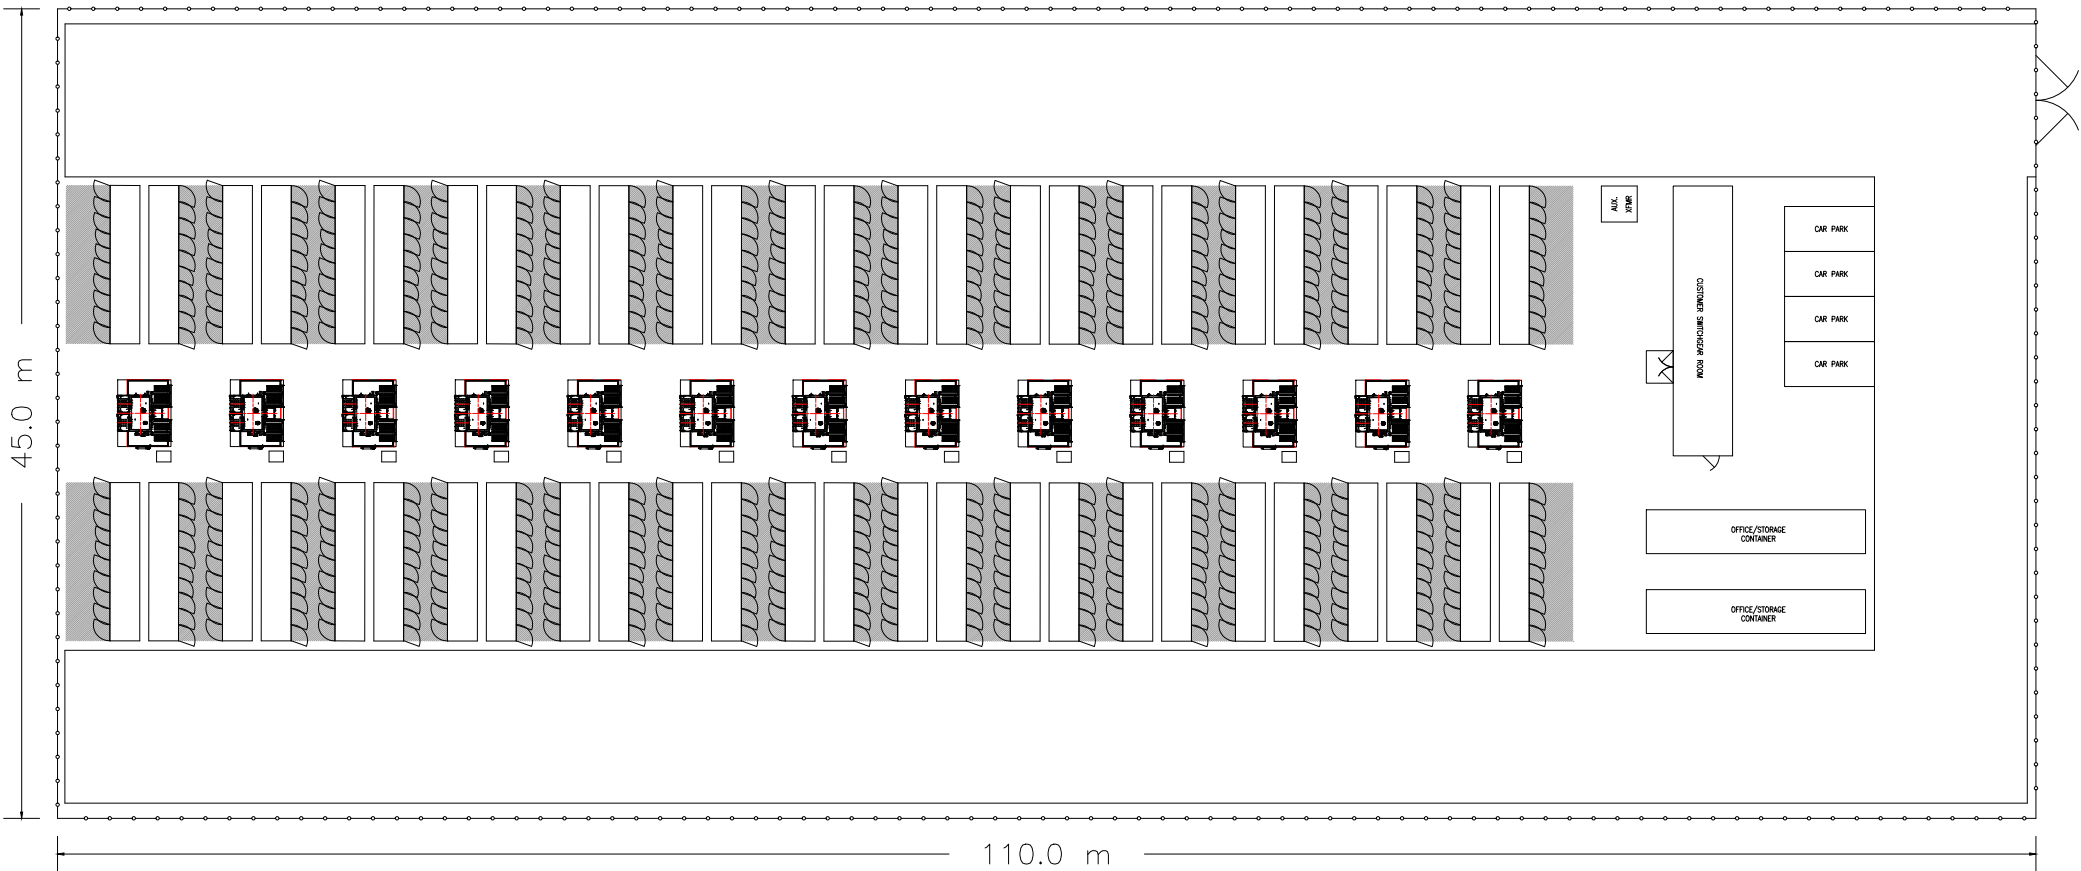

GENERAL NOTES:

1. THIS LAYOUT IS AN EXAMPLE ONLY.
2. HIGH LEVEL CONCEPTUAL DRAWING ONLY. ACTUAL LAYOUT WILL BE DETERMINED DURING THE DETAILED DESIGN PHASE AND MIGHT DEVIATE SIGNIFICANTLY FROM THIS CONCEPTUAL DRAWING.
3. CLEARANCE BETWEEN TESLA EQUIPMENT ARE AS PER TESLA SITE DESIGN AND INSTALLATION MANUALS.
4. TRANSFORMER CLEARANCE SHOWN IS ASSUMING KNAN TRANSFORMER TYPE AND CLEARANCES ACCORDING TO IEC-61936. CLEARANCE WILL INCREASE FOR ONAN TYPE TRANSFORMERS. INSURANCE REQUIREMENTS FOR TRANSFORMER SPACING MAY DEVIATE FROM IEC AND BE BASED ON DIFFERENT STANDARDS.
5. ALL EQUIPMENT AND SITE DIMENSIONS SHOWN ARE INDICATIVE ONLY. THE MEGAPACK, SWITCHGEAR, TRANSFORMER AND OTHER EQUIPMENT DIMENSIONS MAY VARY.
6. LIGHTING, SECURITY AND FIRE CAMERA EQUIPMENT ARE YET TO BE SHOWN. SYSTEMS WILL BE INSTALLED IN ACCORDANCE AND COMPLIANCE WITH PROVIDED EMPLOYER REQUIREMENTS.
7. THE SHOWN FOOTPRINT OF HV AND MV SWITCHYARD AREAS REMAINS UNCHANGED FROM THE ORIGINAL PROPOSAL. THIS MIGHT CHANGE DURING DETAILED DESIGN BY EXTENDING IT TO THE CONSTRUCTION LAYDOWN AREA BELOW.



TESLA MOTORS, INC.
3500 DEER CREEK RD.
PALO ALTO, CA 94304
(650) 681-5000

PRELIMINARY
NOT FOR
CONSTRUCTION

INDICATIVE BESS LAYOUT
50 MW/200 MWh

TESLA ENERGY

NO.	REVISION	DATE	INIT.	DX
1	INDICATIVE LAYOUT	03 AUG 22		

ORIGINAL SIZE:
297x420mm
SHEET SIZE ISO A3

SHEET TITLE
INDICATIVE LAYOUT

SHEET NUMBER

PROPRIETARY AND CONFIDENTIAL