



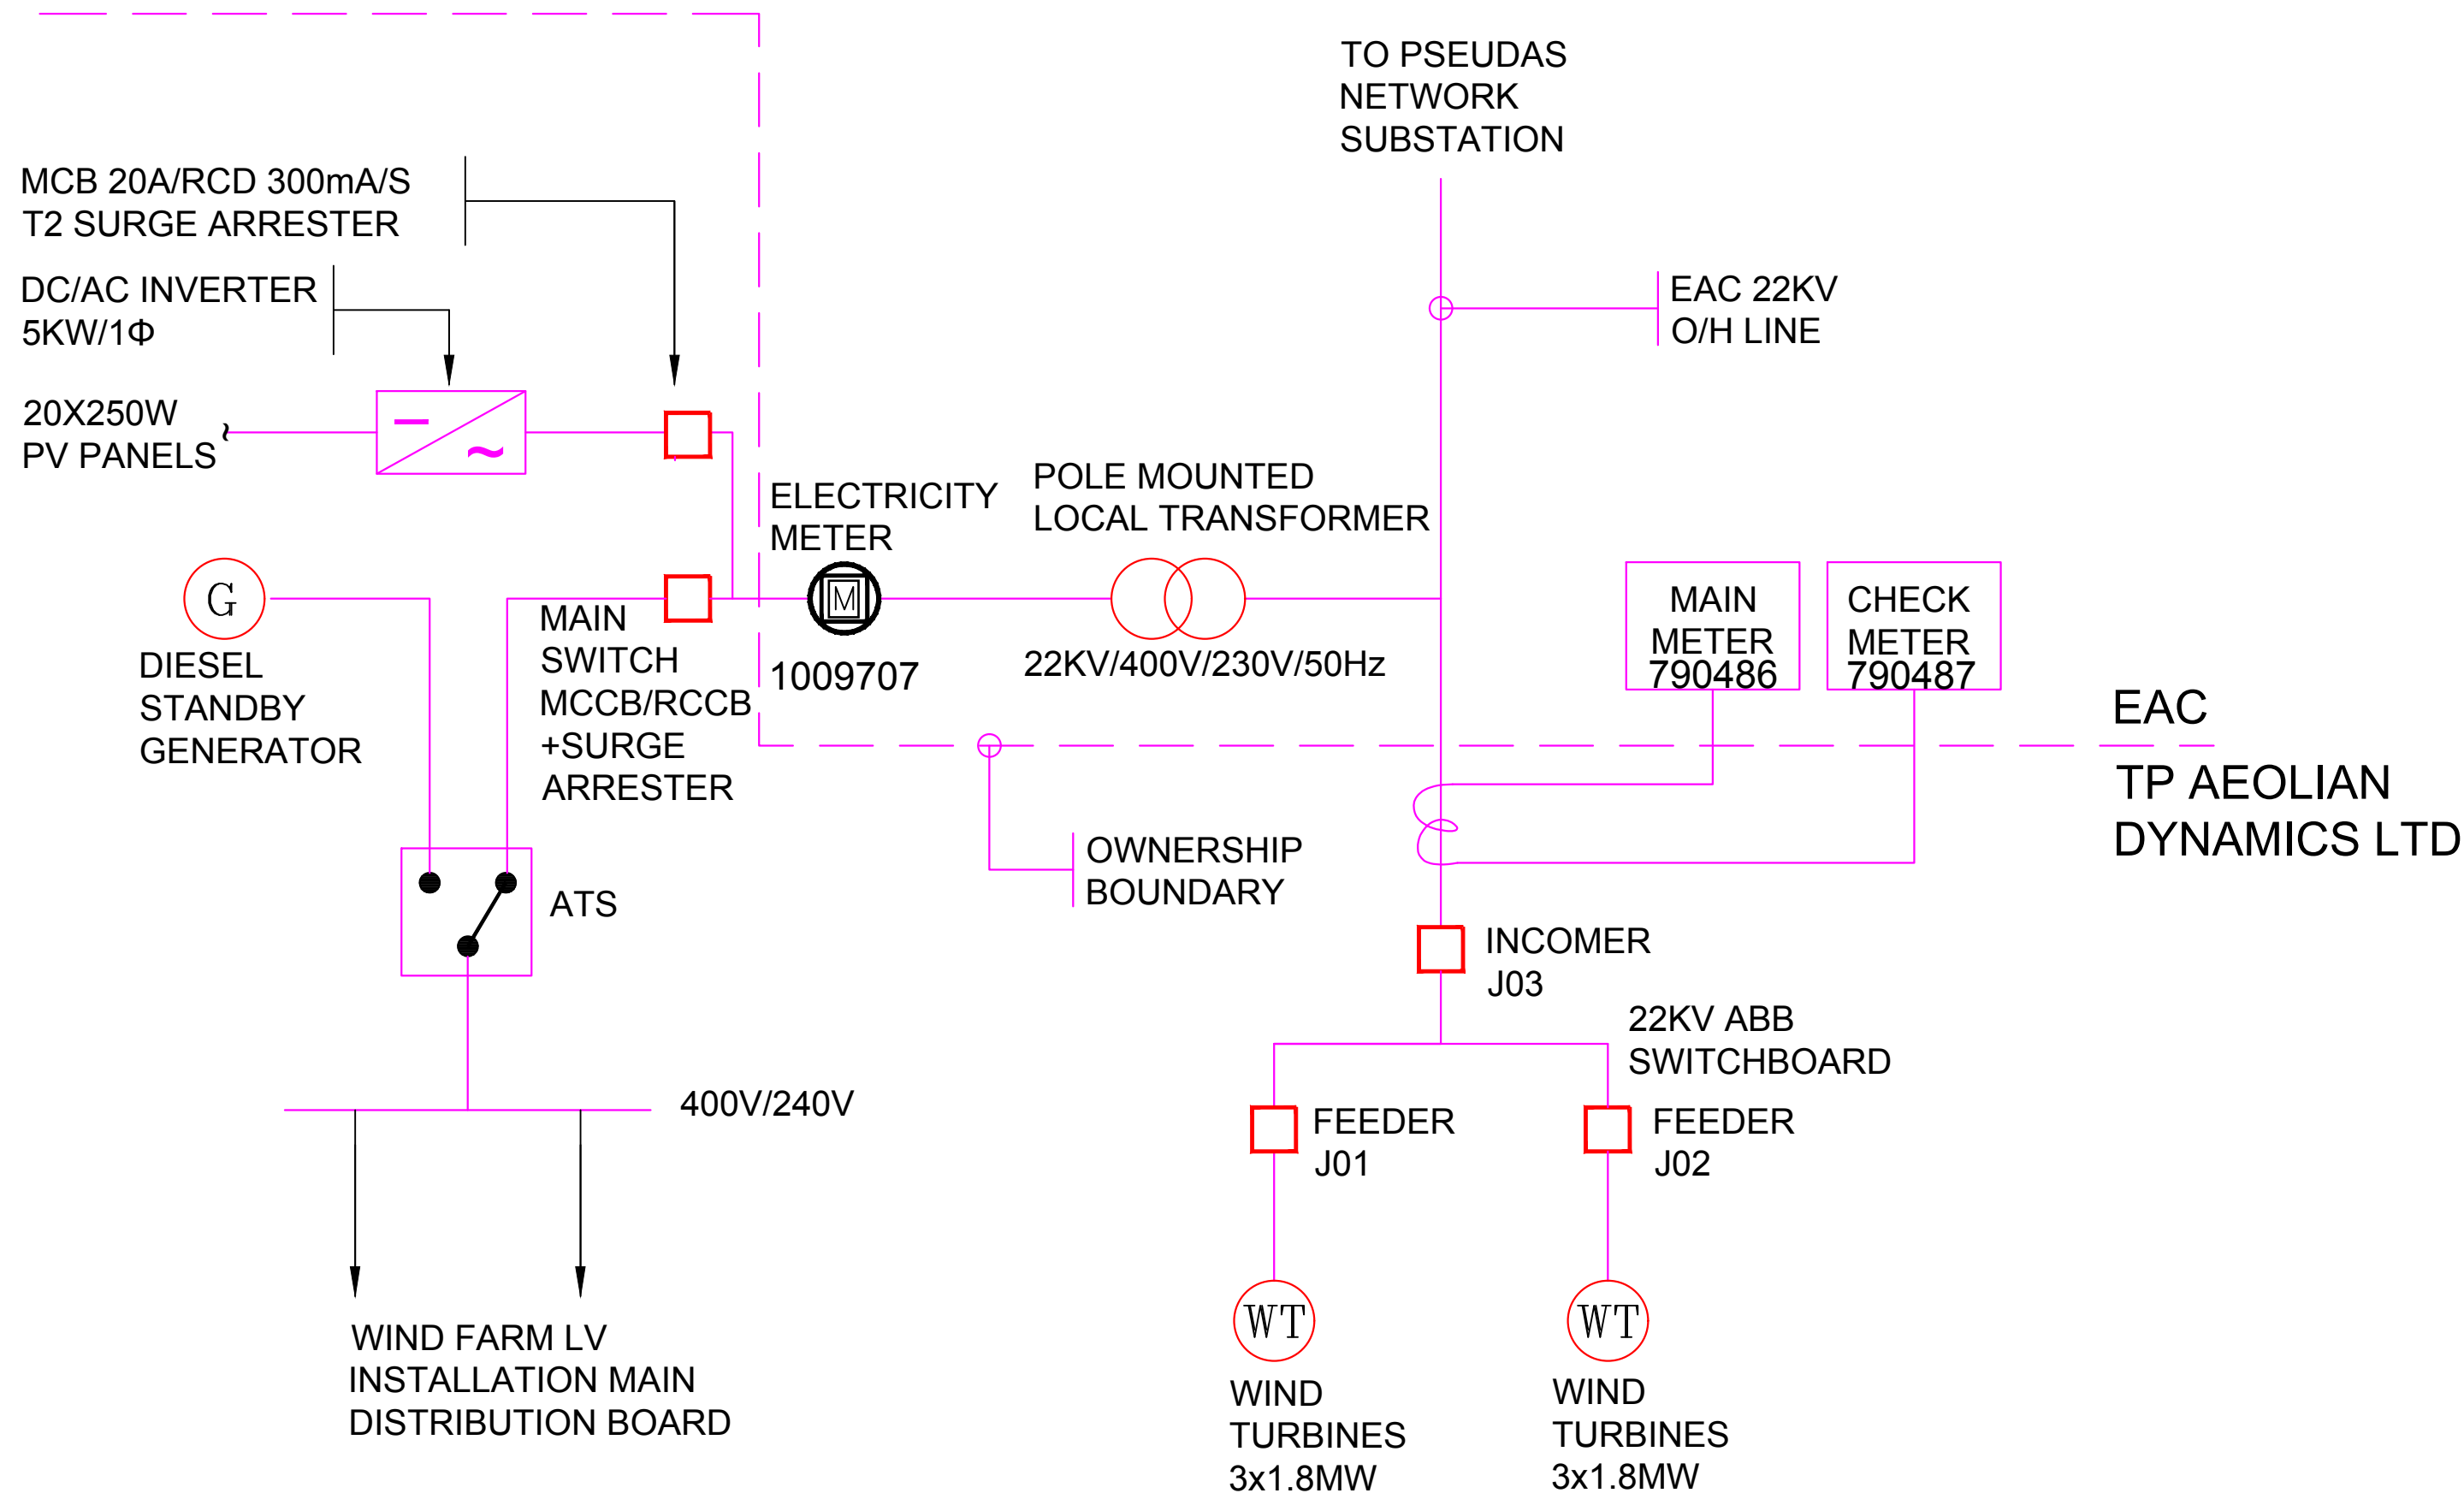

SINGLE LINE DIAGRAM

T.P. AEOLIAN DYNAMICS LTD
AEOLIAN DYNAMICS WIND PARK

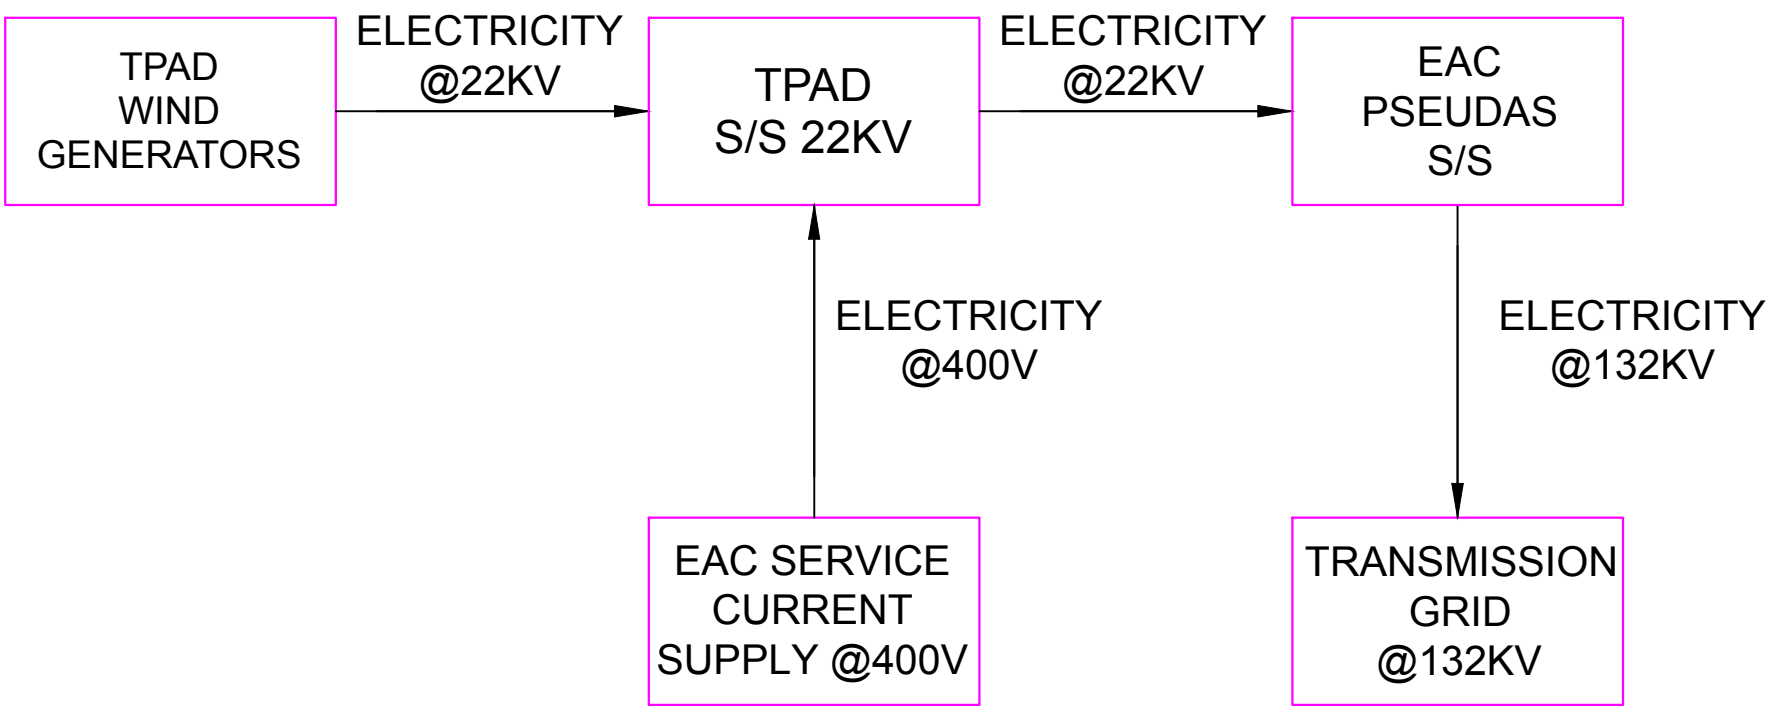

ENERGY FLOW DIAGRAM

UPDATED FOR THE NET METERING OF PV SYSTEM	13-09-17		K.Z
ALL INDICATED DIMENSIONS SUPERCEED MEASURED DIMENSIONS ON THE DRAWINGS. ALL DIMENSIONS SHALL BE CHECKED ON SITE PRIOR TO WORKS COMMENCEMENT. ALL DISCREPANCIES SHALL BE REPORTED TO THE ARCHITECTS FOR CLARIFICATIONS			
Εργο / Project: T.P. AEOLIAN DYNAMICS WIND PARK			
Ιδιοκτήτης / Client: T.P. AEOLIAN DYNAMICS LTD			
Περιγραφή / Description: SINGLE LINE AND ENERGY FLOW DIAGRAMS			
ΠΟΛΙΤΙΚΟΙ ΜΗΧΑΝΙΚΟΙ : EARTHQUAKE PROTECTED STRUCTURES ΓΕΩΡΓΙΟΣ ΔΗΜΗΤΡΙΑΔΗΣ ΝΙΚΟΣ ΚΑΛΑΘΑΣ Διδυμότειχο 9, 3115 Λευκός Τηλ: 25770978 Φαξ: 25770979 email:dk_eps@spidernet.com.cy Αθηνών 111, 2035 Στρόβολος Τηλ.: 22495133 φαξ: 22495123 email:earth@spidernet.com.cy			
ΑΡΧΙΤΕΚΤΟΝΕΣ: ΗΡΑΚΛΗΣ ΠΑΠΑΧΡΙΣΤΟΥ ΑΡΧΙΤΕΚΤΟΝΕΣ 			
Γωνία Αεωφ. Κέντρου & Αριστερή Χαράδρους 1, Αεωκασία 1077, Γραφείο 401, Τηλ.: 22 875996, Fax: 22 374816, E-mail: e.papachristou@cytanet.com.cy			
ELECTRICAL & MECHANICAL CONSULTING ENGINEERS ELIOFOTOU, ZINIERIS STASIS PARTNERS Mechanical Electrical Technology Consultants 77, STROVOLOS AVENUE, STROVOLOS CENTER, FLAT 401, 2018 STROVOLOS - NICOSIA Tel. 22879613 Fax.22314043 e-mail : meltec@meltec-cy.com			
στάδιο μελέτης / design stage:	ημερ. / date:	Κατηγορία μελέτης	
	03/15		
Μέγεθος / scale :	σχεδιαστή / drawn by :	ελεγχός / checked by :	
	E.G.	K.Z.	
αρ. έργου / pr. number :	αρ. σχεδίου / dr. number :	κωδ. σχεδίου / dr. code :	
1291/14	E-02/1 A		