


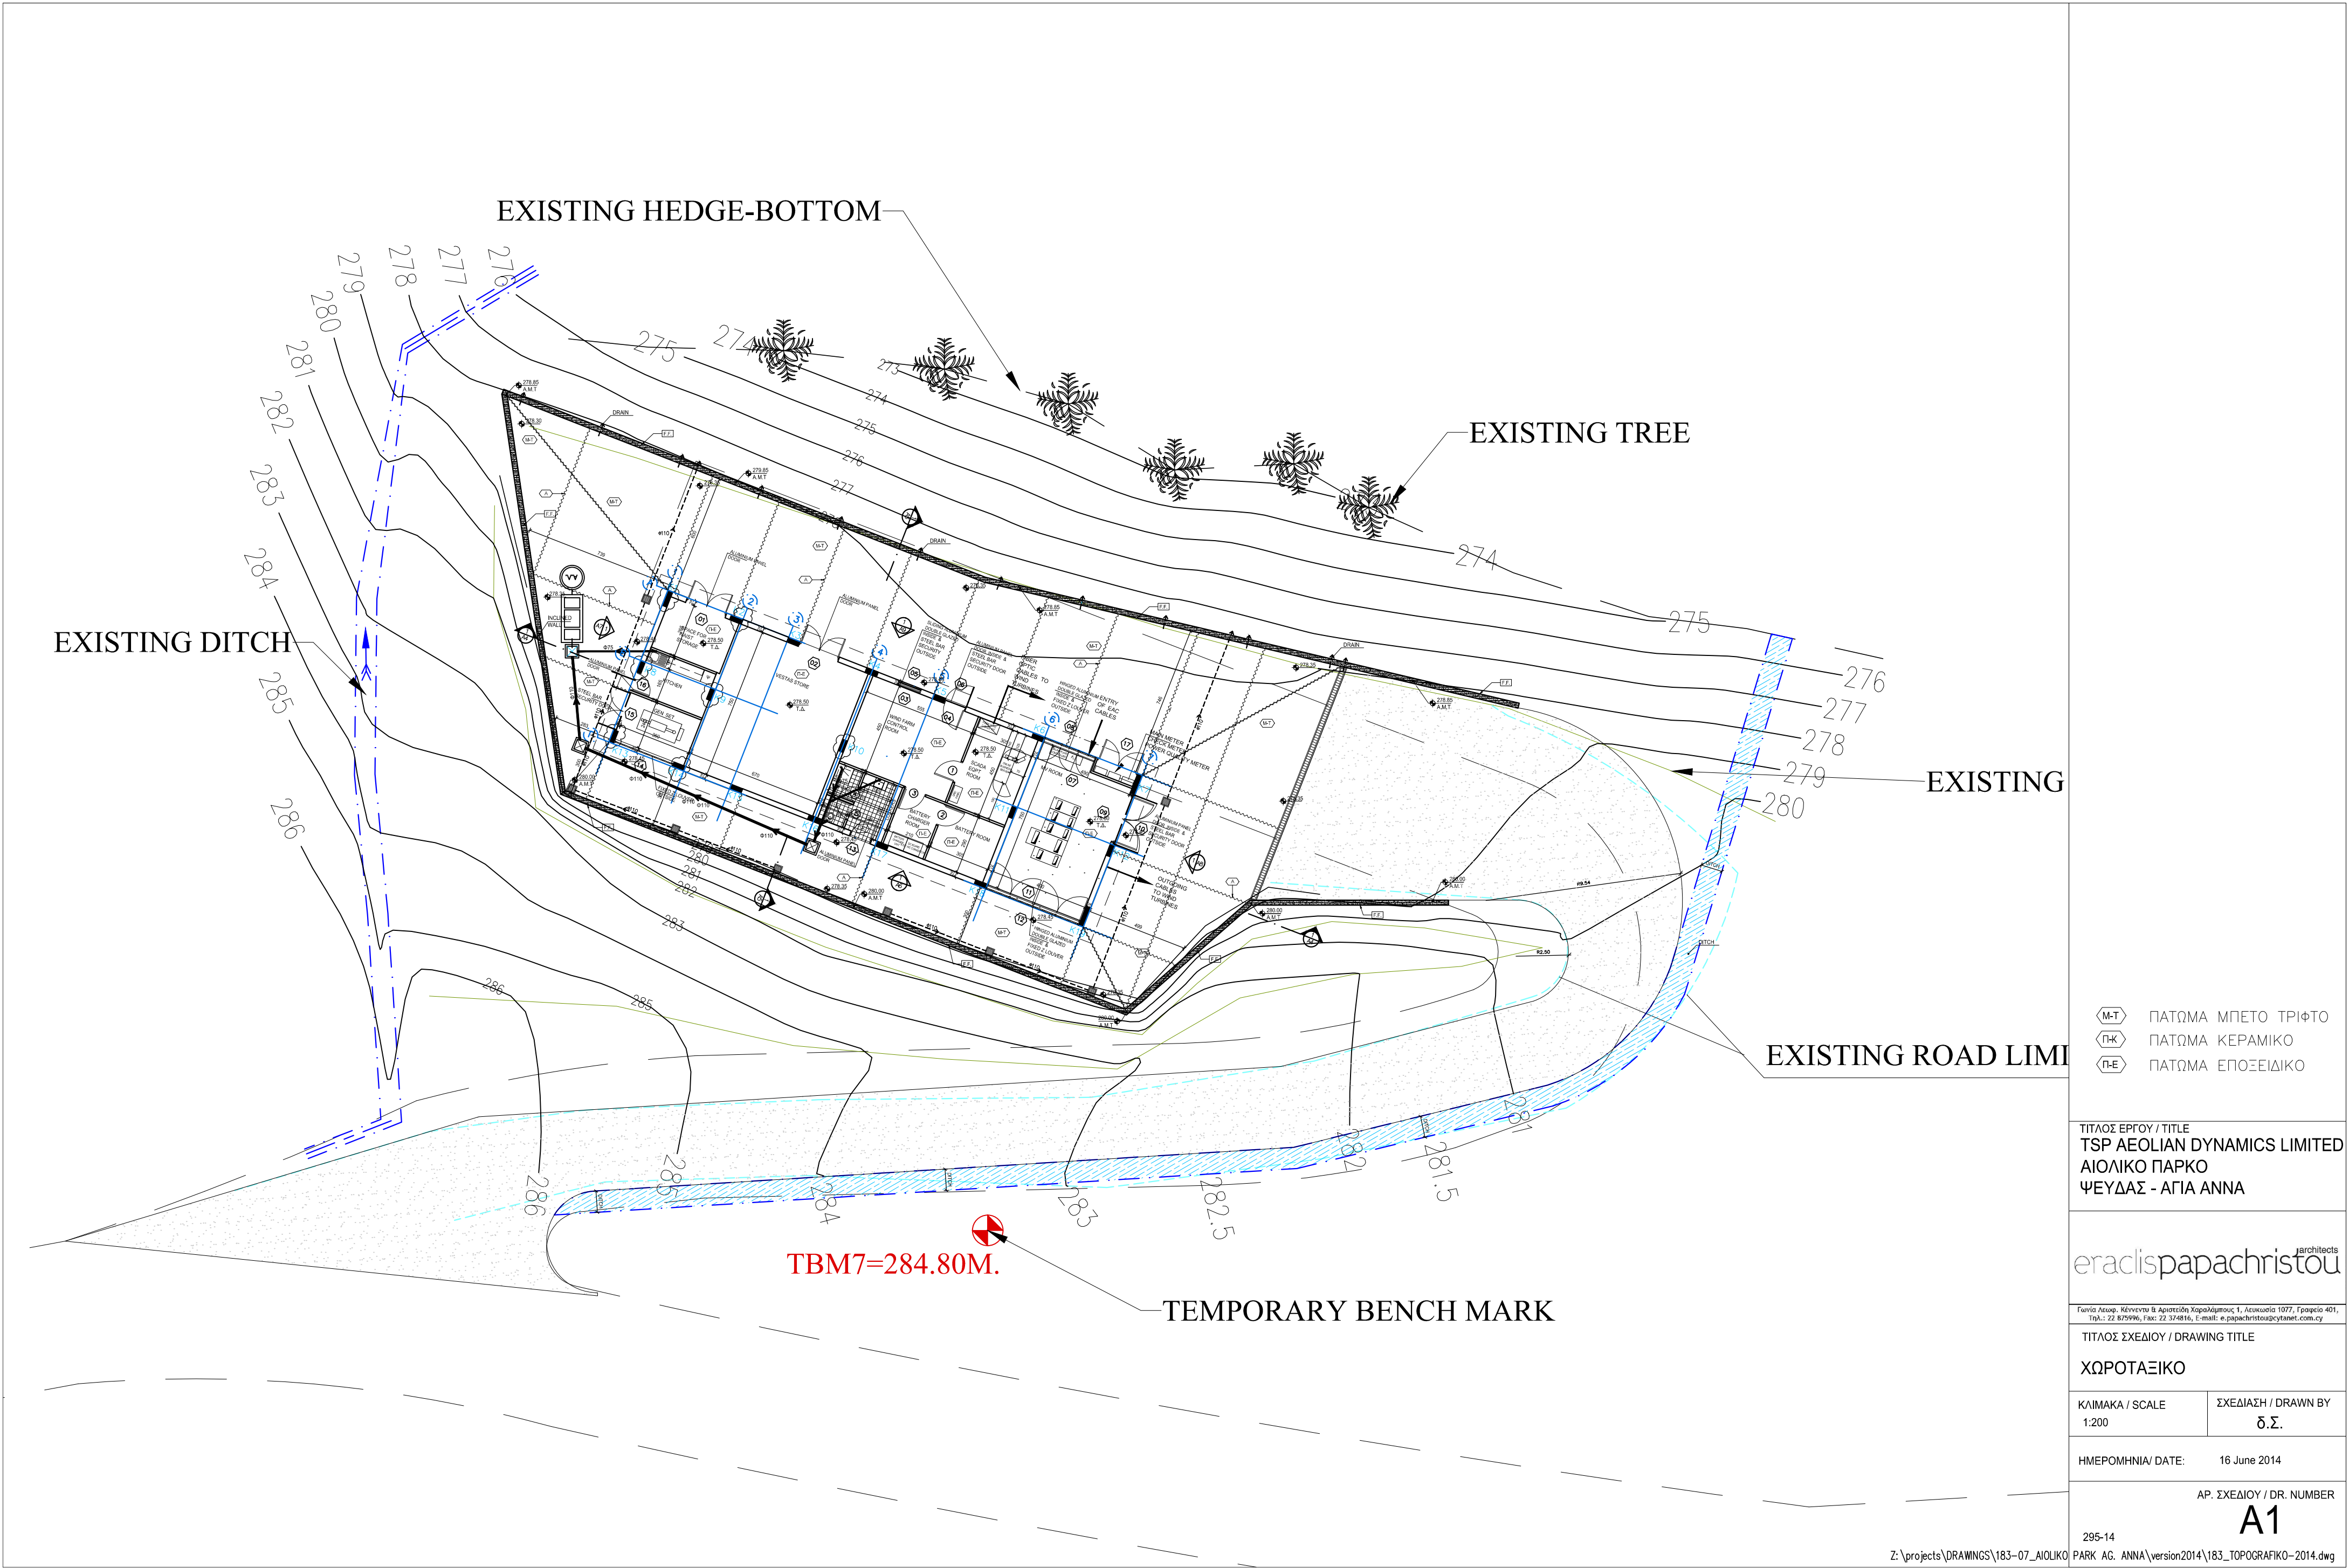

- Μ-Τ ΠΑΤΩΜΑ ΜΠΕΤΟ ΤΡΙΦΤΟ
- ΠΚ ΠΑΤΩΜΑ ΚΕΡΑΜΙΚΟ
- Π-Ε ΠΑΤΩΜΑ ΕΠΟΞΕΙΔΙΚΟ

ΤΙΤΛΟΣ ΕΡΓΟΥ / TITLE
ΤΣΡ ΑΕΟΛΙΑΝ DYNAMICS LIMITED
ΑΙΟΛΙΚΟ ΠΑΡΚΟ
ΨΕΥΔΑΣ - ΑΓΙΑ ΑΝΝΑ

eraclispapachristou architects

Γενία Αεωρ. Κέντρου & Αρτιστική Χαραλάμους 1, Λευκωσία 1077, Γραφείο 401,
Τηλ.: 22 875996, Fax: 22 374816, E-mail: e.papachristou@cytanet.com.cy

ΤΙΤΛΟΣ ΣΧΕΔΙΟΥ / DRAWING TITLE
ΧΩΡΟΤΑΞΙΚΟ

ΚΛΙΜΑΚΑ / SCALE
1:200

ΣΧΕΔΙΑΣΗ / DRAWN BY
Δ.Σ.

ΗΜΕΡΟΜΗΝΙΑ / DATE: 16 June 2014

ΑΡ. ΣΧΕΔΙΟΥ / DR. NUMBER
A1

295-14