


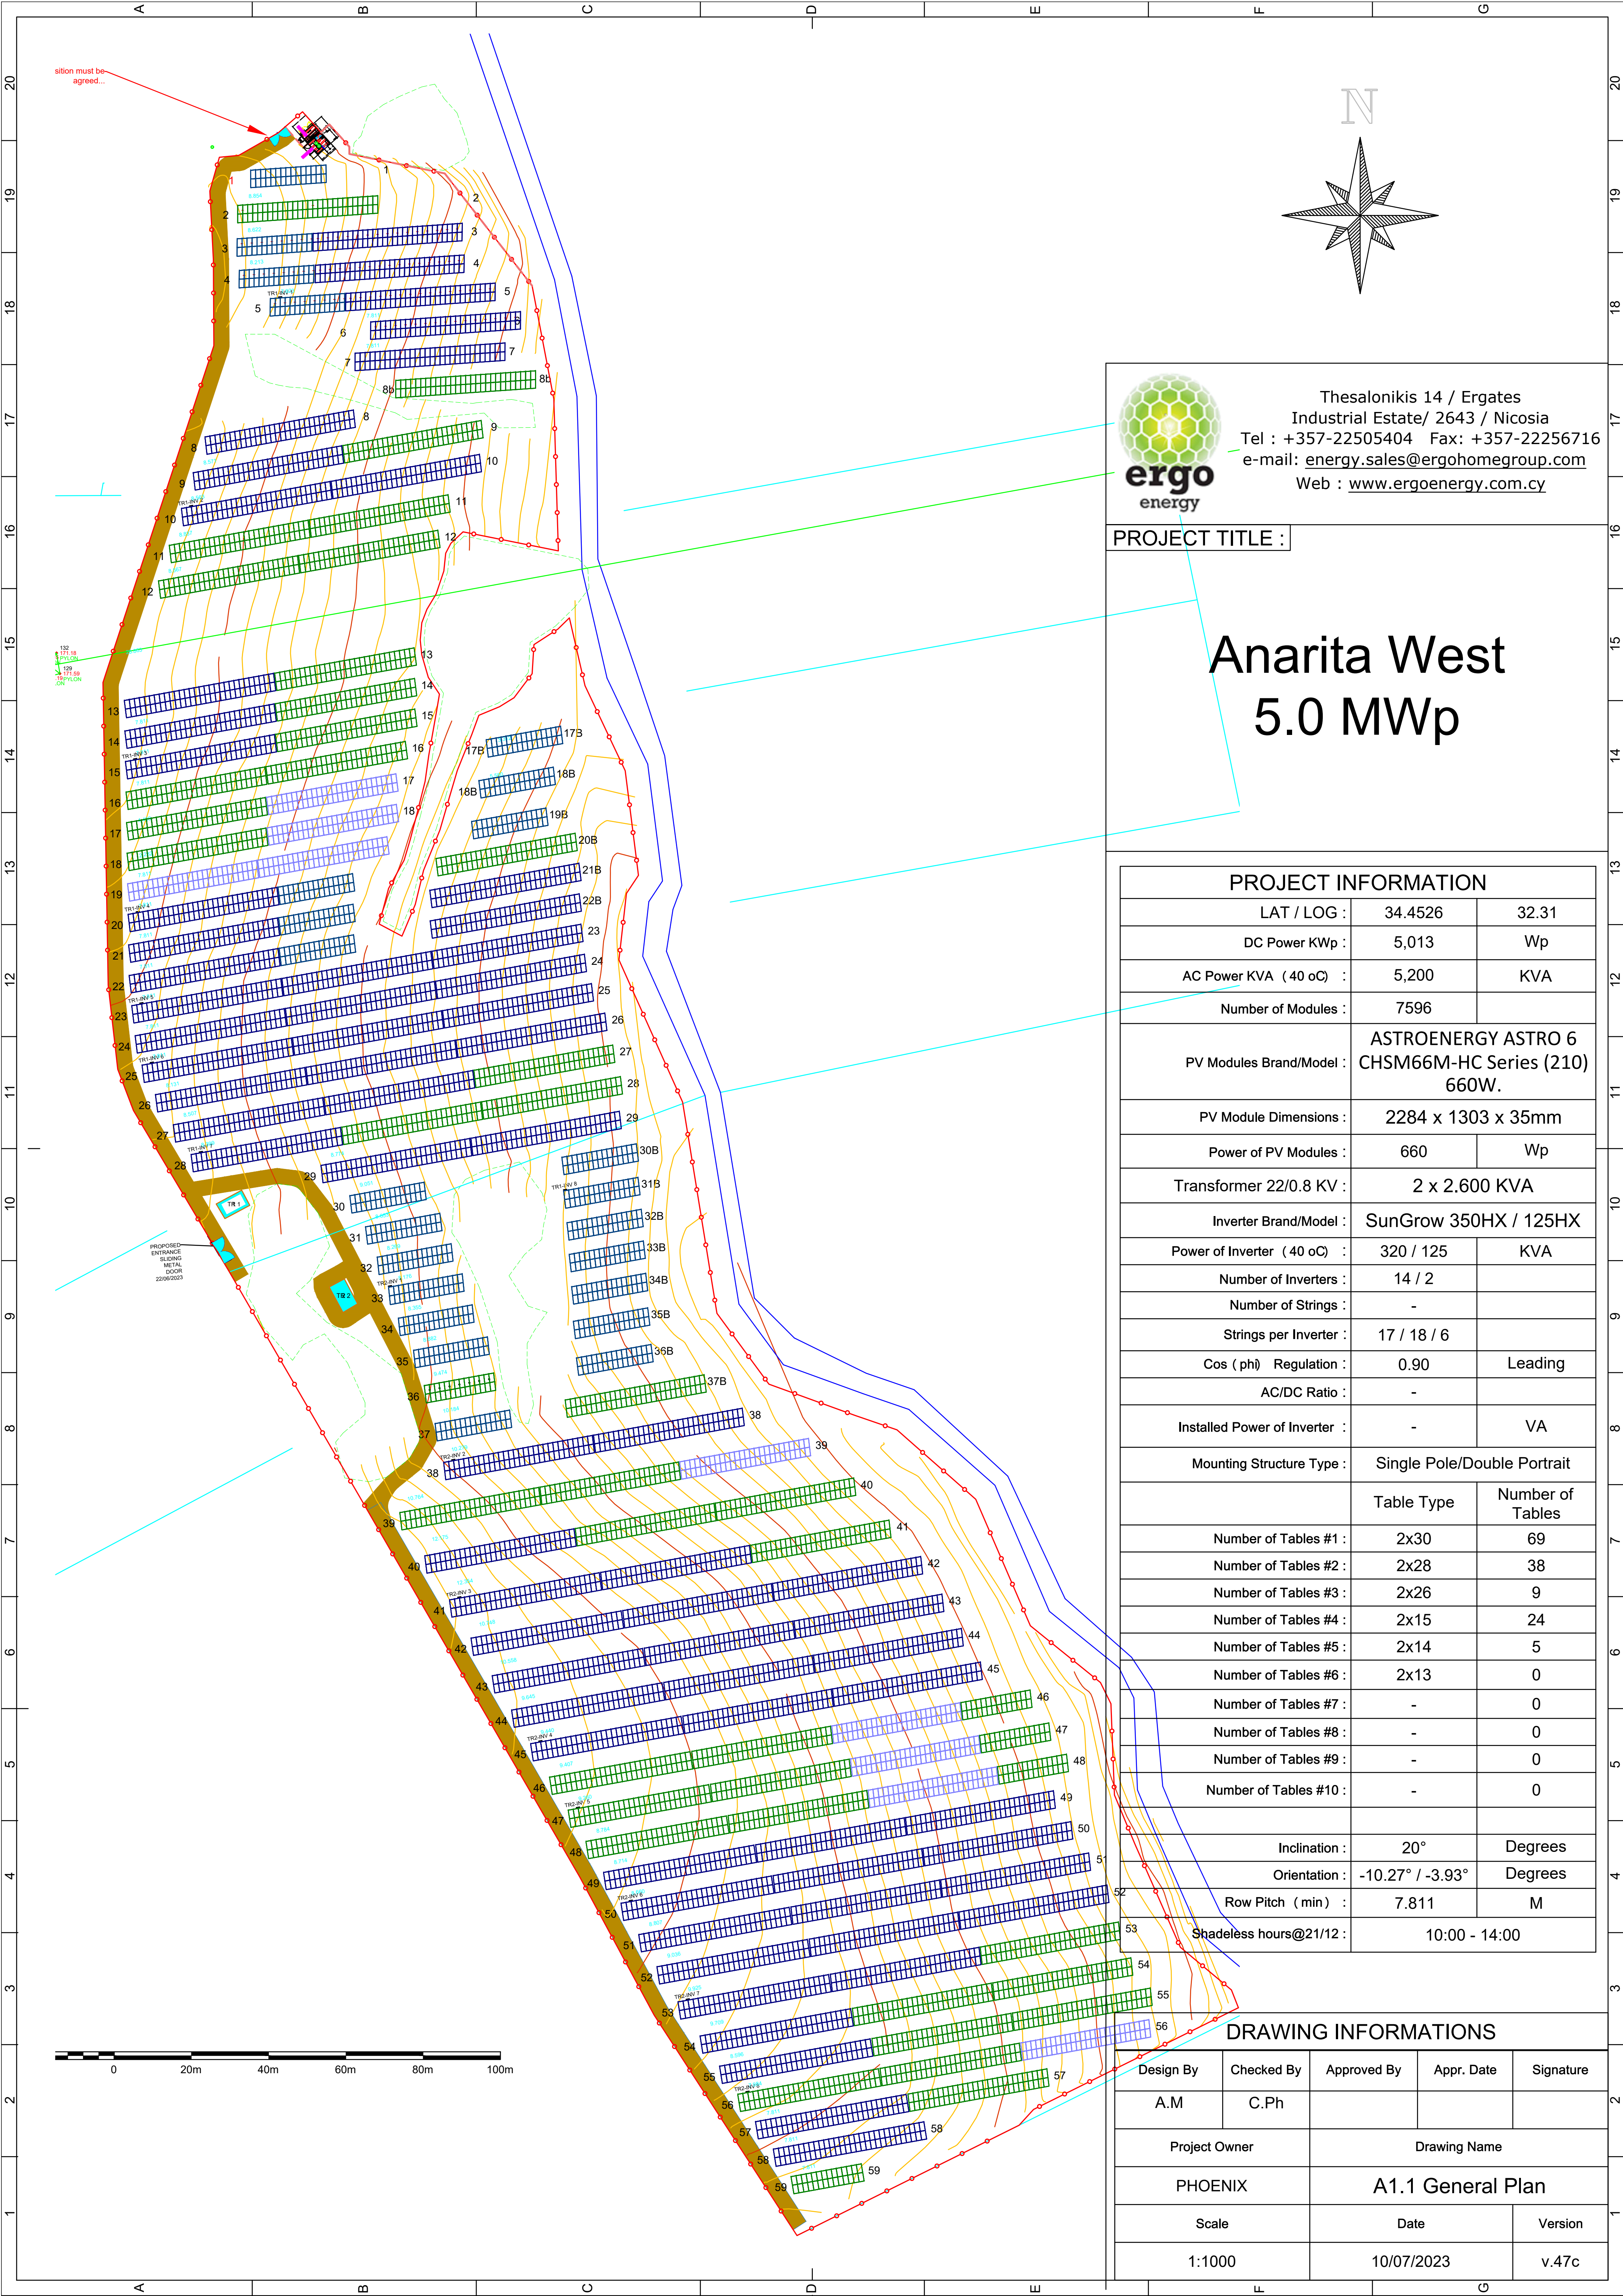



Thessalonikis 14 / Ergates
Industrial Estate/ 2643 / Nicosia
Tel : +357-22505404 Fax: +357-22256716
e-mail: energy.sales@ergohomegroup.com
Web : www.ergoenergy.com.cy

PROJECT TITLE :

Anarita West

5.0 MWp

PROJECT INFORMATION		
LAT / LOG :	34.4526	32.31
DC Power KWp :	5,013	Wp
AC Power KVA (40 oC) :	5,200	KVA
Number of Modules :	7596	
PV Modules Brand/Model :	ASTROENERGY ASTRO 6 CHSM66M-HC Series (210) 660W.	
PV Module Dimensions :	2284 x 1303 x 35mm	
Power of PV Modules :	660	Wp
Transformer 22/0.8 KV :	2 x 2.600 KVA	
Inverter Brand/Model :	SunGrow 350HX / 125HX	
Power of Inverter (40 oC) :	320 / 125	KVA
Number of Inverters :	14 / 2	
Number of Strings :	-	
Strings per Inverter :	17 / 18 / 6	
Cos (phi) Regulation :	0.90	Leading
AC/DC Ratio :	-	
Installed Power of Inverter :	-	VA
Mounting Structure Type :	Single Pole/Double Portrait	
	Table Type	Number of Tables
Number of Tables #1 :	2x30	69
Number of Tables #2 :	2x28	38
Number of Tables #3 :	2x26	9
Number of Tables #4 :	2x15	24
Number of Tables #5 :	2x14	5
Number of Tables #6 :	2x13	0
Number of Tables #7 :	-	0
Number of Tables #8 :	-	0
Number of Tables #9 :	-	0
Number of Tables #10 :	-	0
Inclination :	20°	Degrees
Orientation :	-10.27° / -3.93°	Degrees
Row Pitch (min) :	7.811	M
Shadeless hours@21/12 :	10:00 - 14:00	

DRAWING INFORMATIONS

Design By	Checked By	Approved By	Appr. Date	Signature
A.M	C.Ph			
Project Owner		Drawing Name		
PHOENIX		A1.1 General Plan		
Scale	Date		Version	
1:1000	10/07/2023		v.47c	