


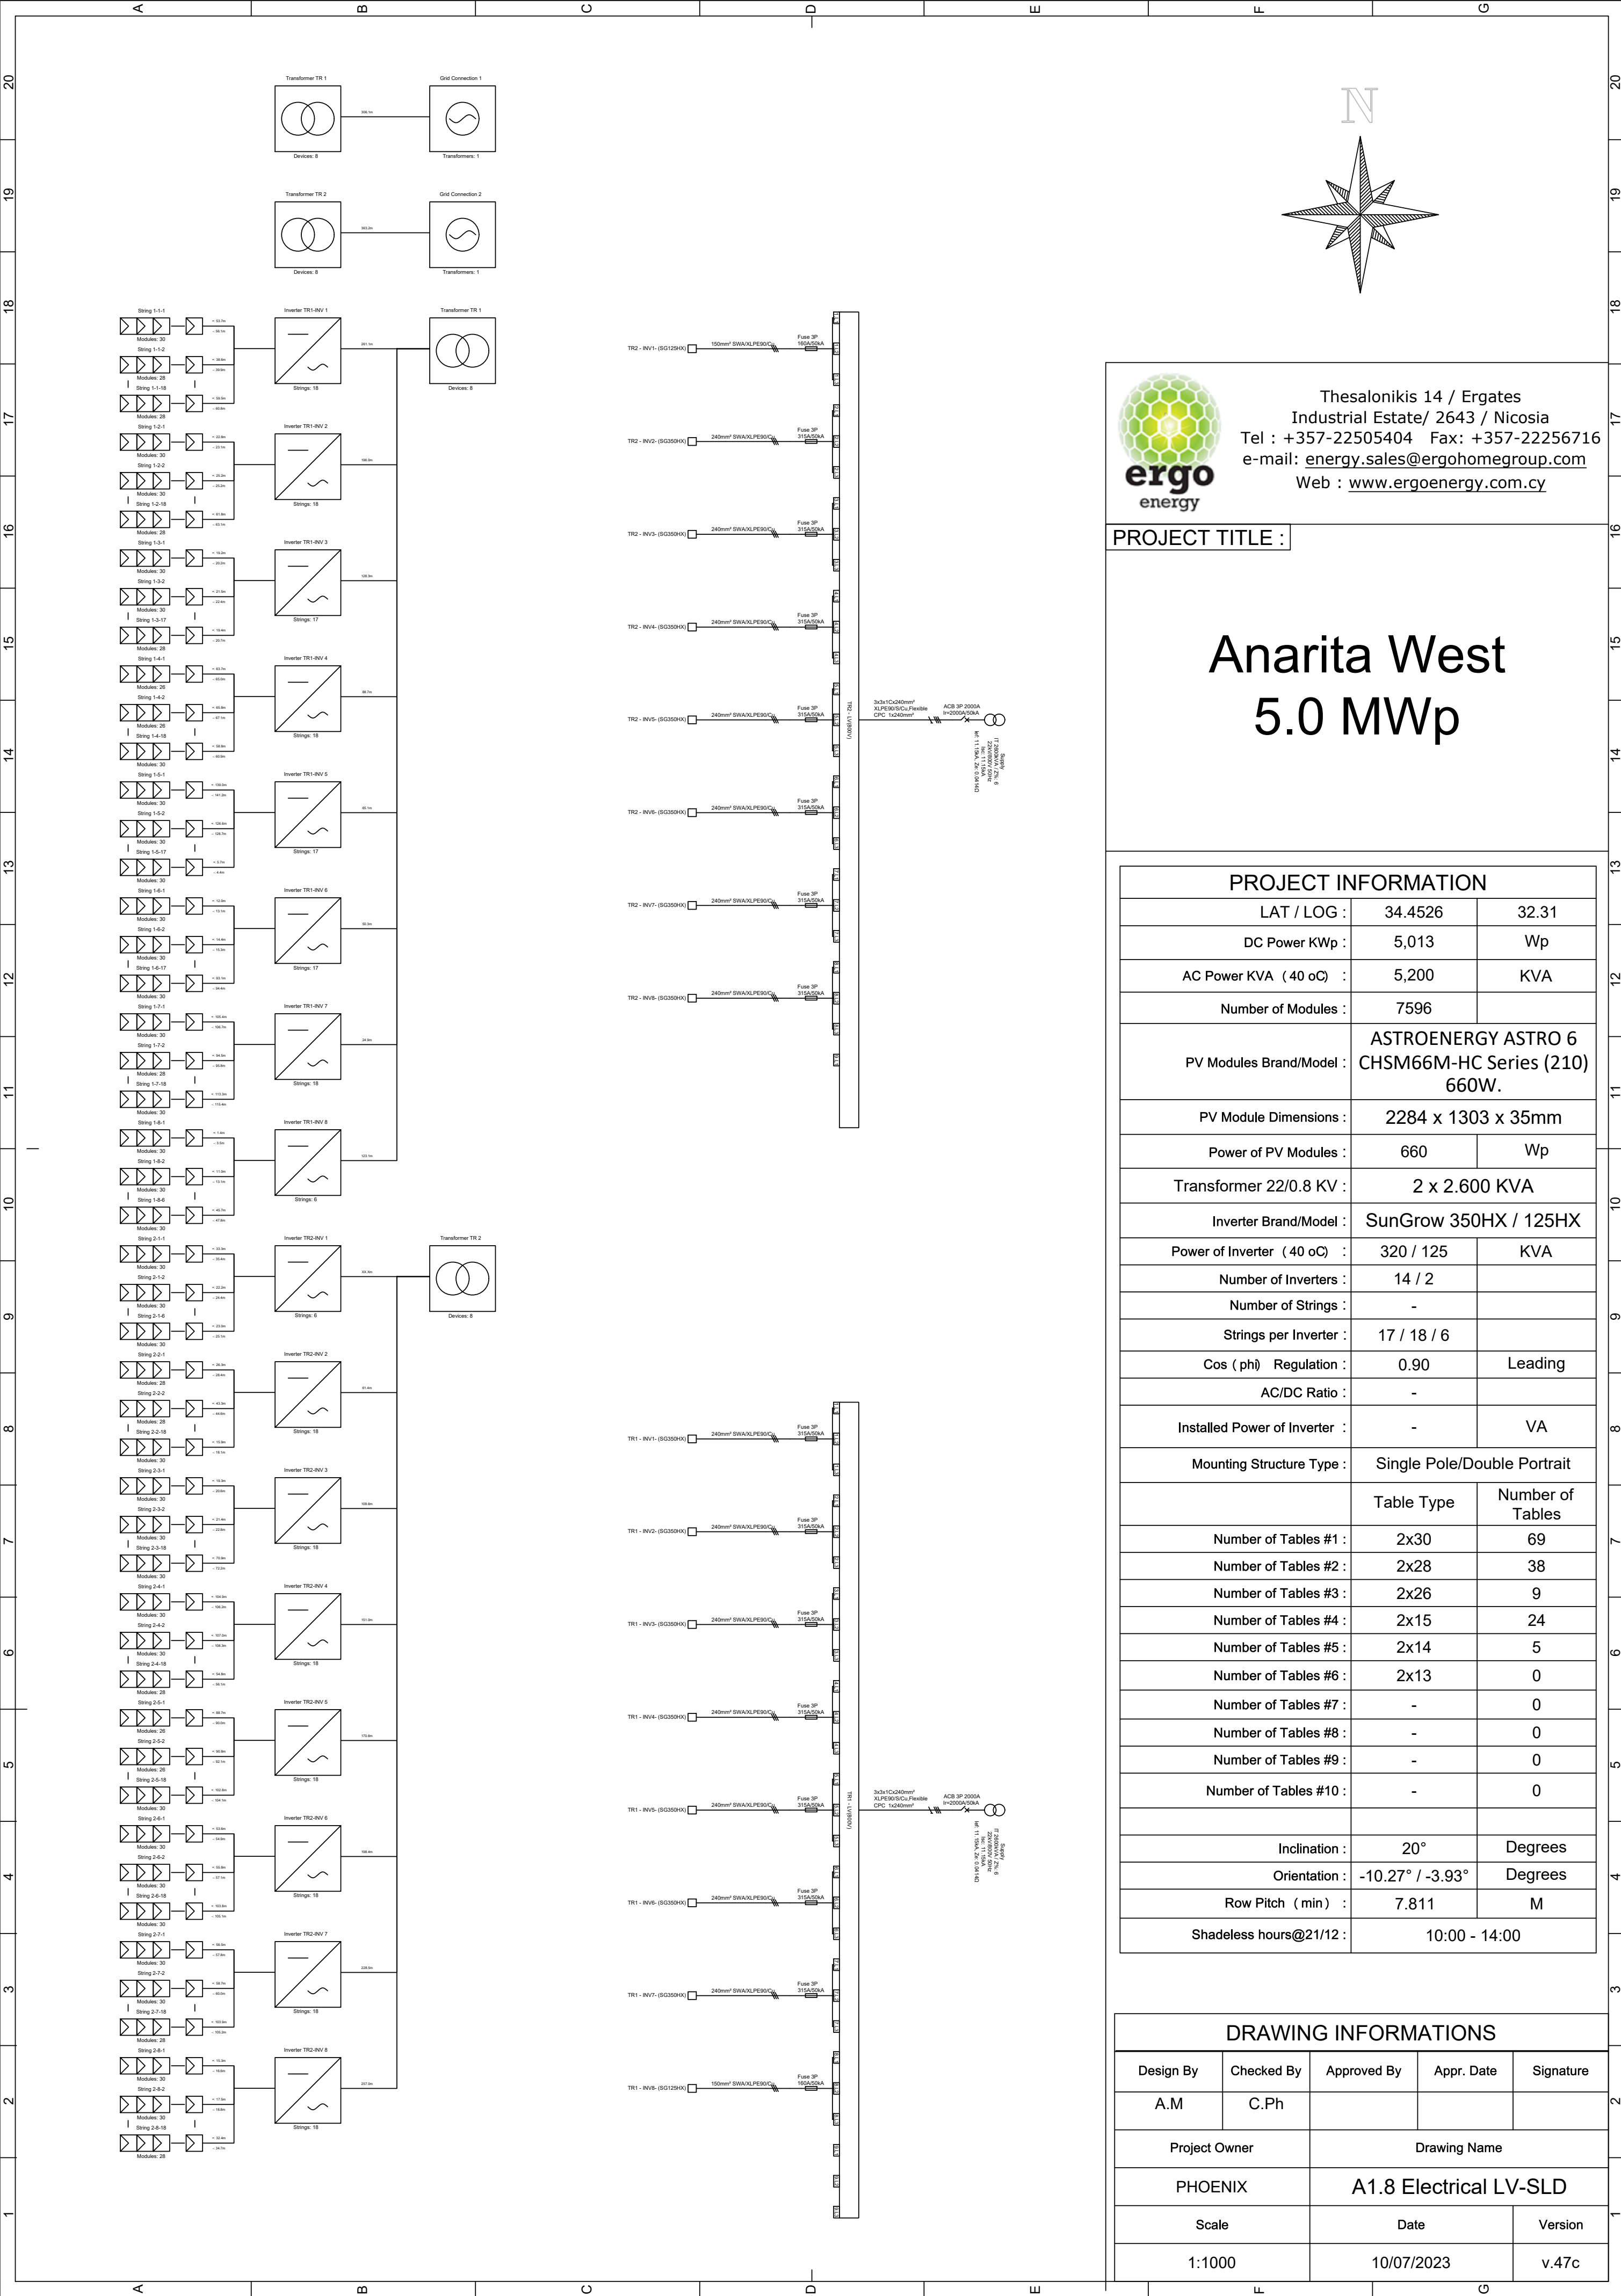

Thessalonikis 14 / Ergates  
Industrial Estate/ 2643 / Nicosia  
Tel : +357-22505404 Fax: +357-22256716  
e-mail: [energy.sales@ergohomegroup.com](mailto:energy.sales@ergohomegroup.com)  
Web : [www.ergoenergy.com.cy](http://www.ergoenergy.com.cy)

PROJECT TITLE :

# Anarita West 5.0 MWp

| PROJECT INFORMATION           |                                                         |                  |
|-------------------------------|---------------------------------------------------------|------------------|
| LAT / LOG :                   | 34.4526                                                 | 32.31            |
| DC Power KWp :                | 5,013                                                   | Wp               |
| AC Power KVA ( 40 oC ) :      | 5,200                                                   | KVA              |
| Number of Modules :           | 7596                                                    |                  |
| PV Modules Brand/Model :      | ASTROENERGY ASTRO 6<br>CHSM66M-HC Series (210)<br>660W. |                  |
| PV Module Dimensions :        | 2284 x 1303 x 35mm                                      |                  |
| Power of PV Modules :         | 660                                                     | Wp               |
| Transformer 22/0.8 KV :       | 2 x 2.600 KVA                                           |                  |
| Inverter Brand/Model :        | SunGrow 350HX / 125HX                                   |                  |
| Power of Inverter ( 40 oC ) : | 320 / 125                                               | KVA              |
| Number of Inverters :         | 14 / 2                                                  |                  |
| Number of Strings :           | -                                                       |                  |
| Strings per Inverter :        | 17 / 18 / 6                                             |                  |
| Cos ( phi ) Regulation :      | 0.90                                                    | Leading          |
| AC/DC Ratio :                 | -                                                       |                  |
| Installed Power of Inverter : | -                                                       | VA               |
| Mounting Structure Type :     | Single Pole/Double Portrait                             |                  |
|                               | Table Type                                              | Number of Tables |
| Number of Tables #1 :         | 2x30                                                    | 69               |
| Number of Tables #2 :         | 2x28                                                    | 38               |
| Number of Tables #3 :         | 2x26                                                    | 9                |
| Number of Tables #4 :         | 2x15                                                    | 24               |
| Number of Tables #5 :         | 2x14                                                    | 5                |
| Number of Tables #6 :         | 2x13                                                    | 0                |
| Number of Tables #7 :         | -                                                       | 0                |
| Number of Tables #8 :         | -                                                       | 0                |
| Number of Tables #9 :         | -                                                       | 0                |
| Number of Tables #10 :        | -                                                       | 0                |
| Inclination :                 | 20°                                                     | Degrees          |
| Orientation :                 | -10.27° / -3.93°                                        | Degrees          |
| Row Pitch ( min ) :           | 7.811                                                   | M                |
| Shadeless hours@21/12 :       | 10:00 - 14:00                                           |                  |

| DRAWING INFORMATIONS |            |                        |            |           |
|----------------------|------------|------------------------|------------|-----------|
| Design By            | Checked By | Approved By            | Appr. Date | Signature |
| A.M                  | C.Ph       |                        |            |           |
| Project Owner        |            | Drawing Name           |            |           |
| PHOENIX              |            | A1.8 Electrical LV-SLD |            |           |
| Scale                | Date       |                        | Version    |           |
| 1:1000               | 10/07/2023 |                        | v.47c      |           |