




CUSTOMER: ERGO HOME ENERGY LTD						PANEL: MV PANEL SBC-SBC-SBC			
ADDRESS: 41-49, Nimeli CourtBlock B, 2408 Egkomi P.O. Box 26774, 1647 Nicosia Cyprus						TEL: +357 7777 14 11 E-MAIL: info@ergohomegroup.com			
PROJECT: ANARITA 10MW						DRAWING NO: -			
LOCATION: CYPRUS						ORDER NO: -			
						PROJECT CODE:			
						PROJECT START: -			
						PROJECT END: -			

SPECIFICATIONS	Switchgear		Electrical Characteristics		COMMENTS				
	Type:	Unisec 24kV/20kV	Rated Current:	630A					
	Color:	RAL7035	Voltage /Frequency:	20kV / 50Hz					
	Dimensions:	2429x1180x2000mm	Short Circuit Capacity:	20kA / 3s					
	Protection Rate (IP):	IP3X	Control Voltage:	230VAC					
	Internal Arc Classification (IAC):	AF	Signalling Voltage:	230VAC					
	Appartus Type:	SF6	Construction Standard:	EN 62271:200					

REVISIONS	No	Date	Description	Drawn	Date	Checked	Date	Approved	Date
	03	20/07/2023	EL. DRAWING 3rd VERSION FOR REVIEW	A. ALEXIOU	20/07/2023	A. ALEXIOU	20/07/2023	A. ALEXIOU	20/07/2023
	02	20/03/2023	EL. DRAWING 2ND VERSION FOR REVIEW	A. ALEXIOU	20/03/2023	A. ALEXIOU	20/03/2023	A. ALEXIOU	20/03/2023
01	20/02/2023	EL. DRAWING 1ST VERSION FOR REVIEW	A. ALEXIOU	20/02/2023	A. ALEXIOU	20/02/2023	ILVIEF SA	20/02/2023	

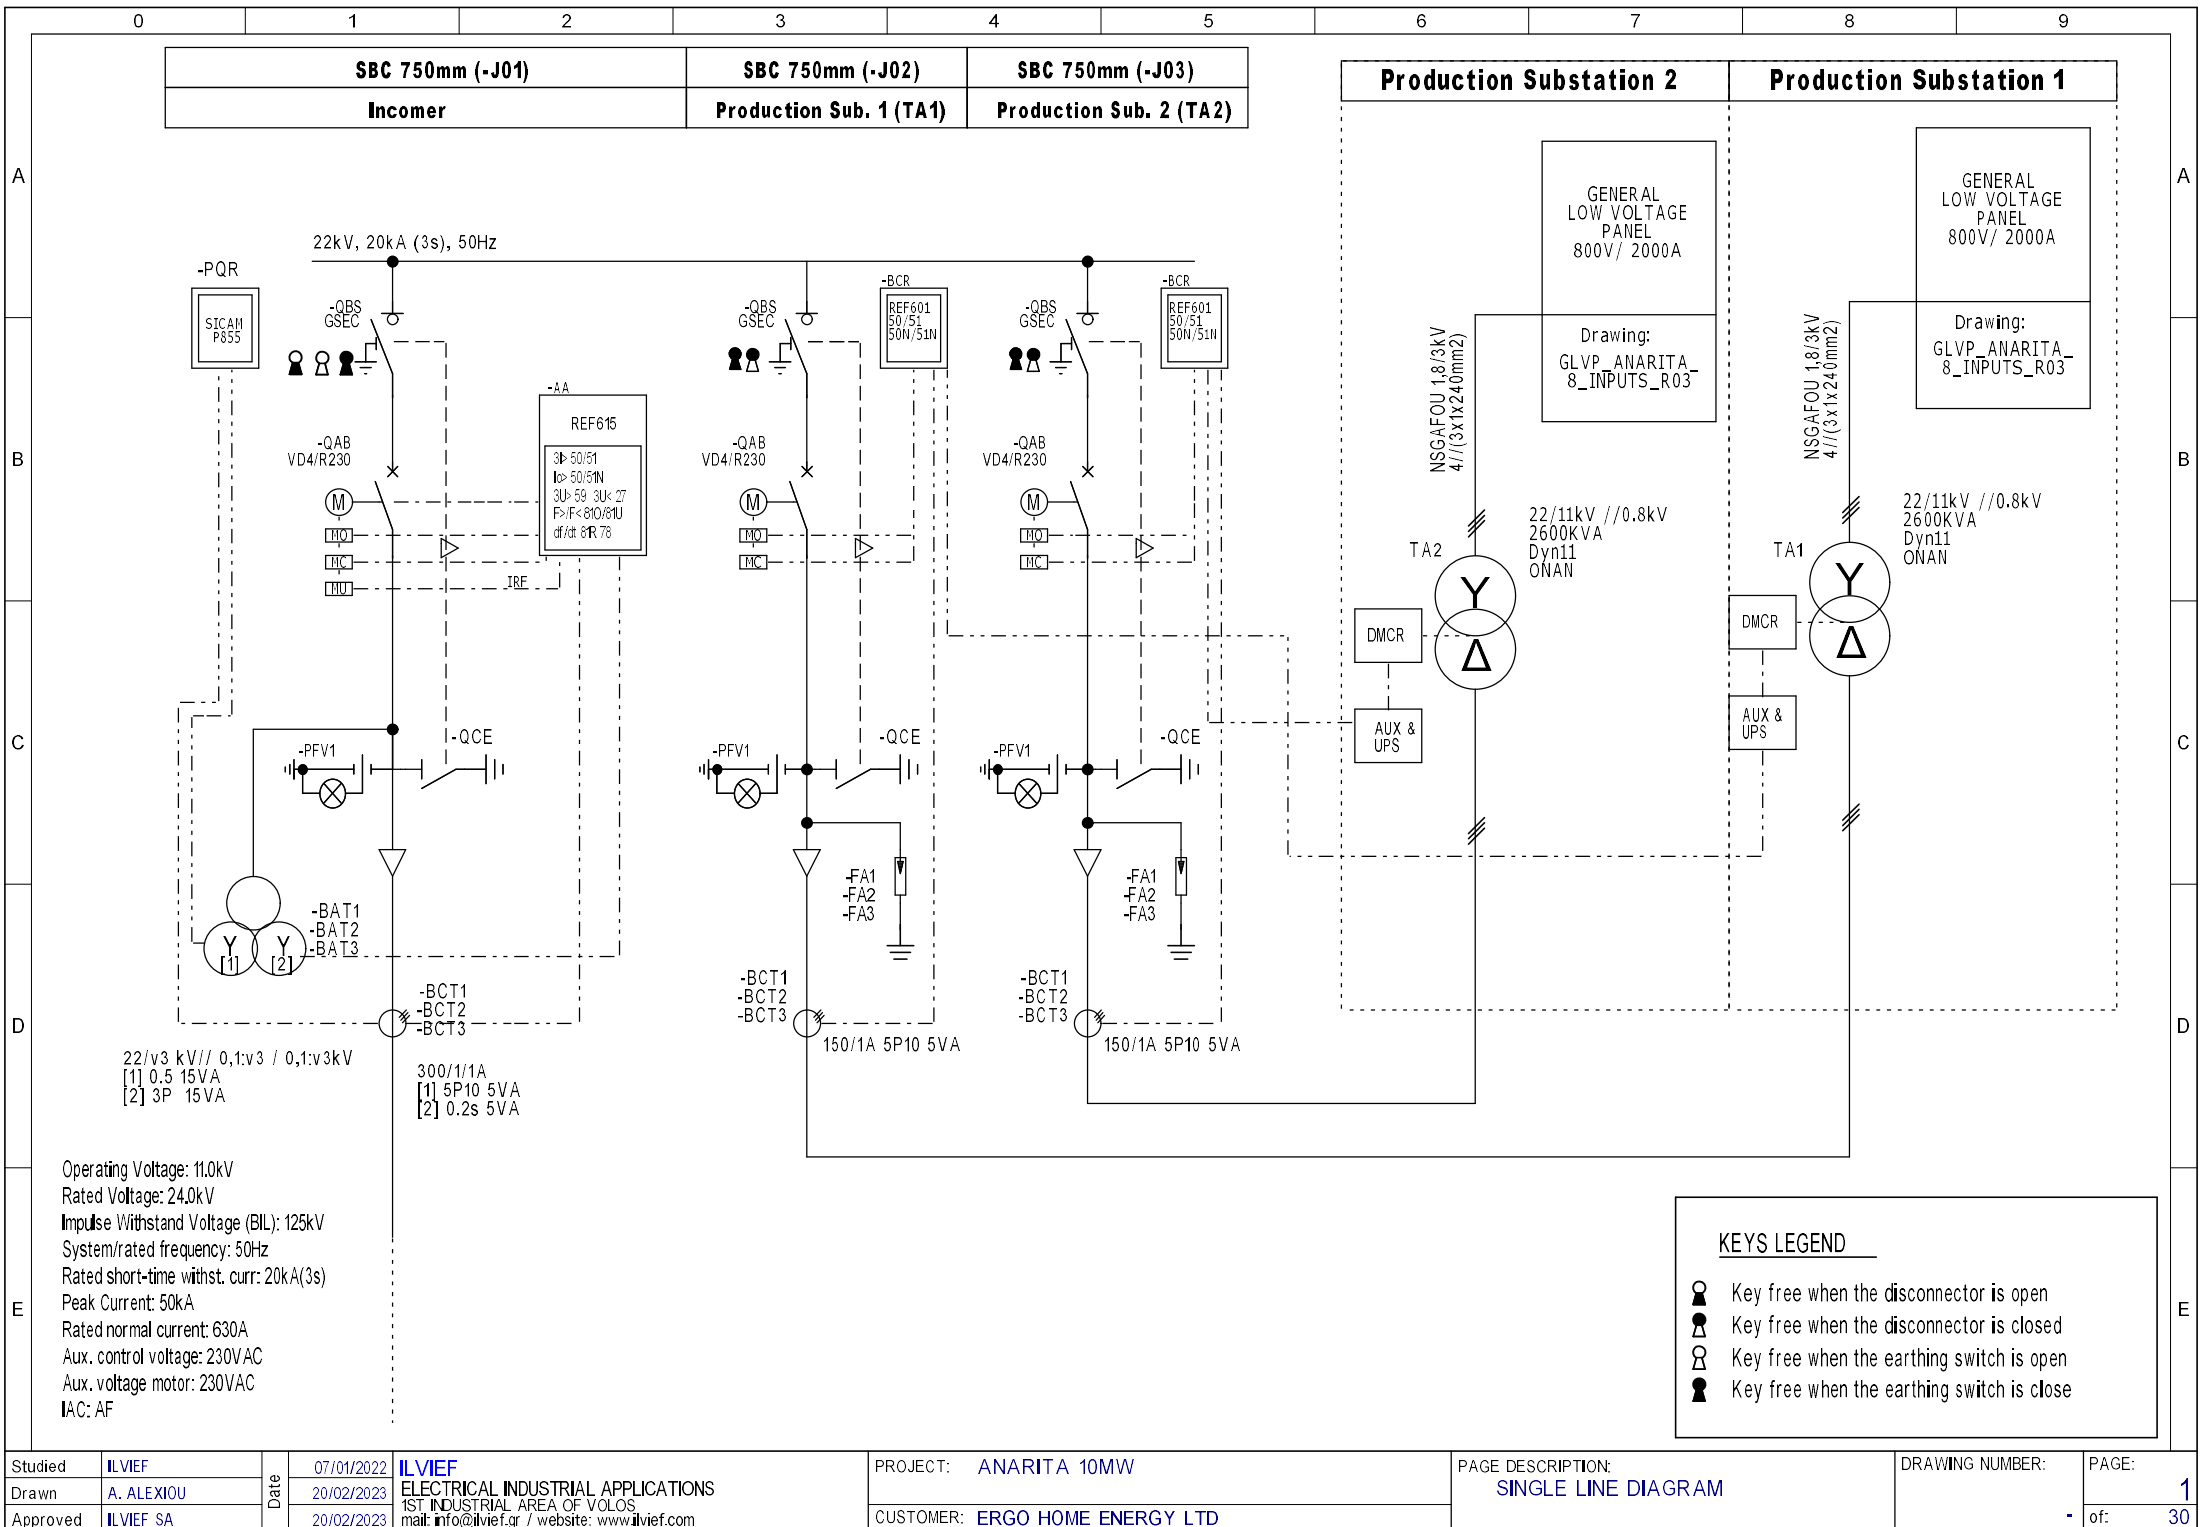


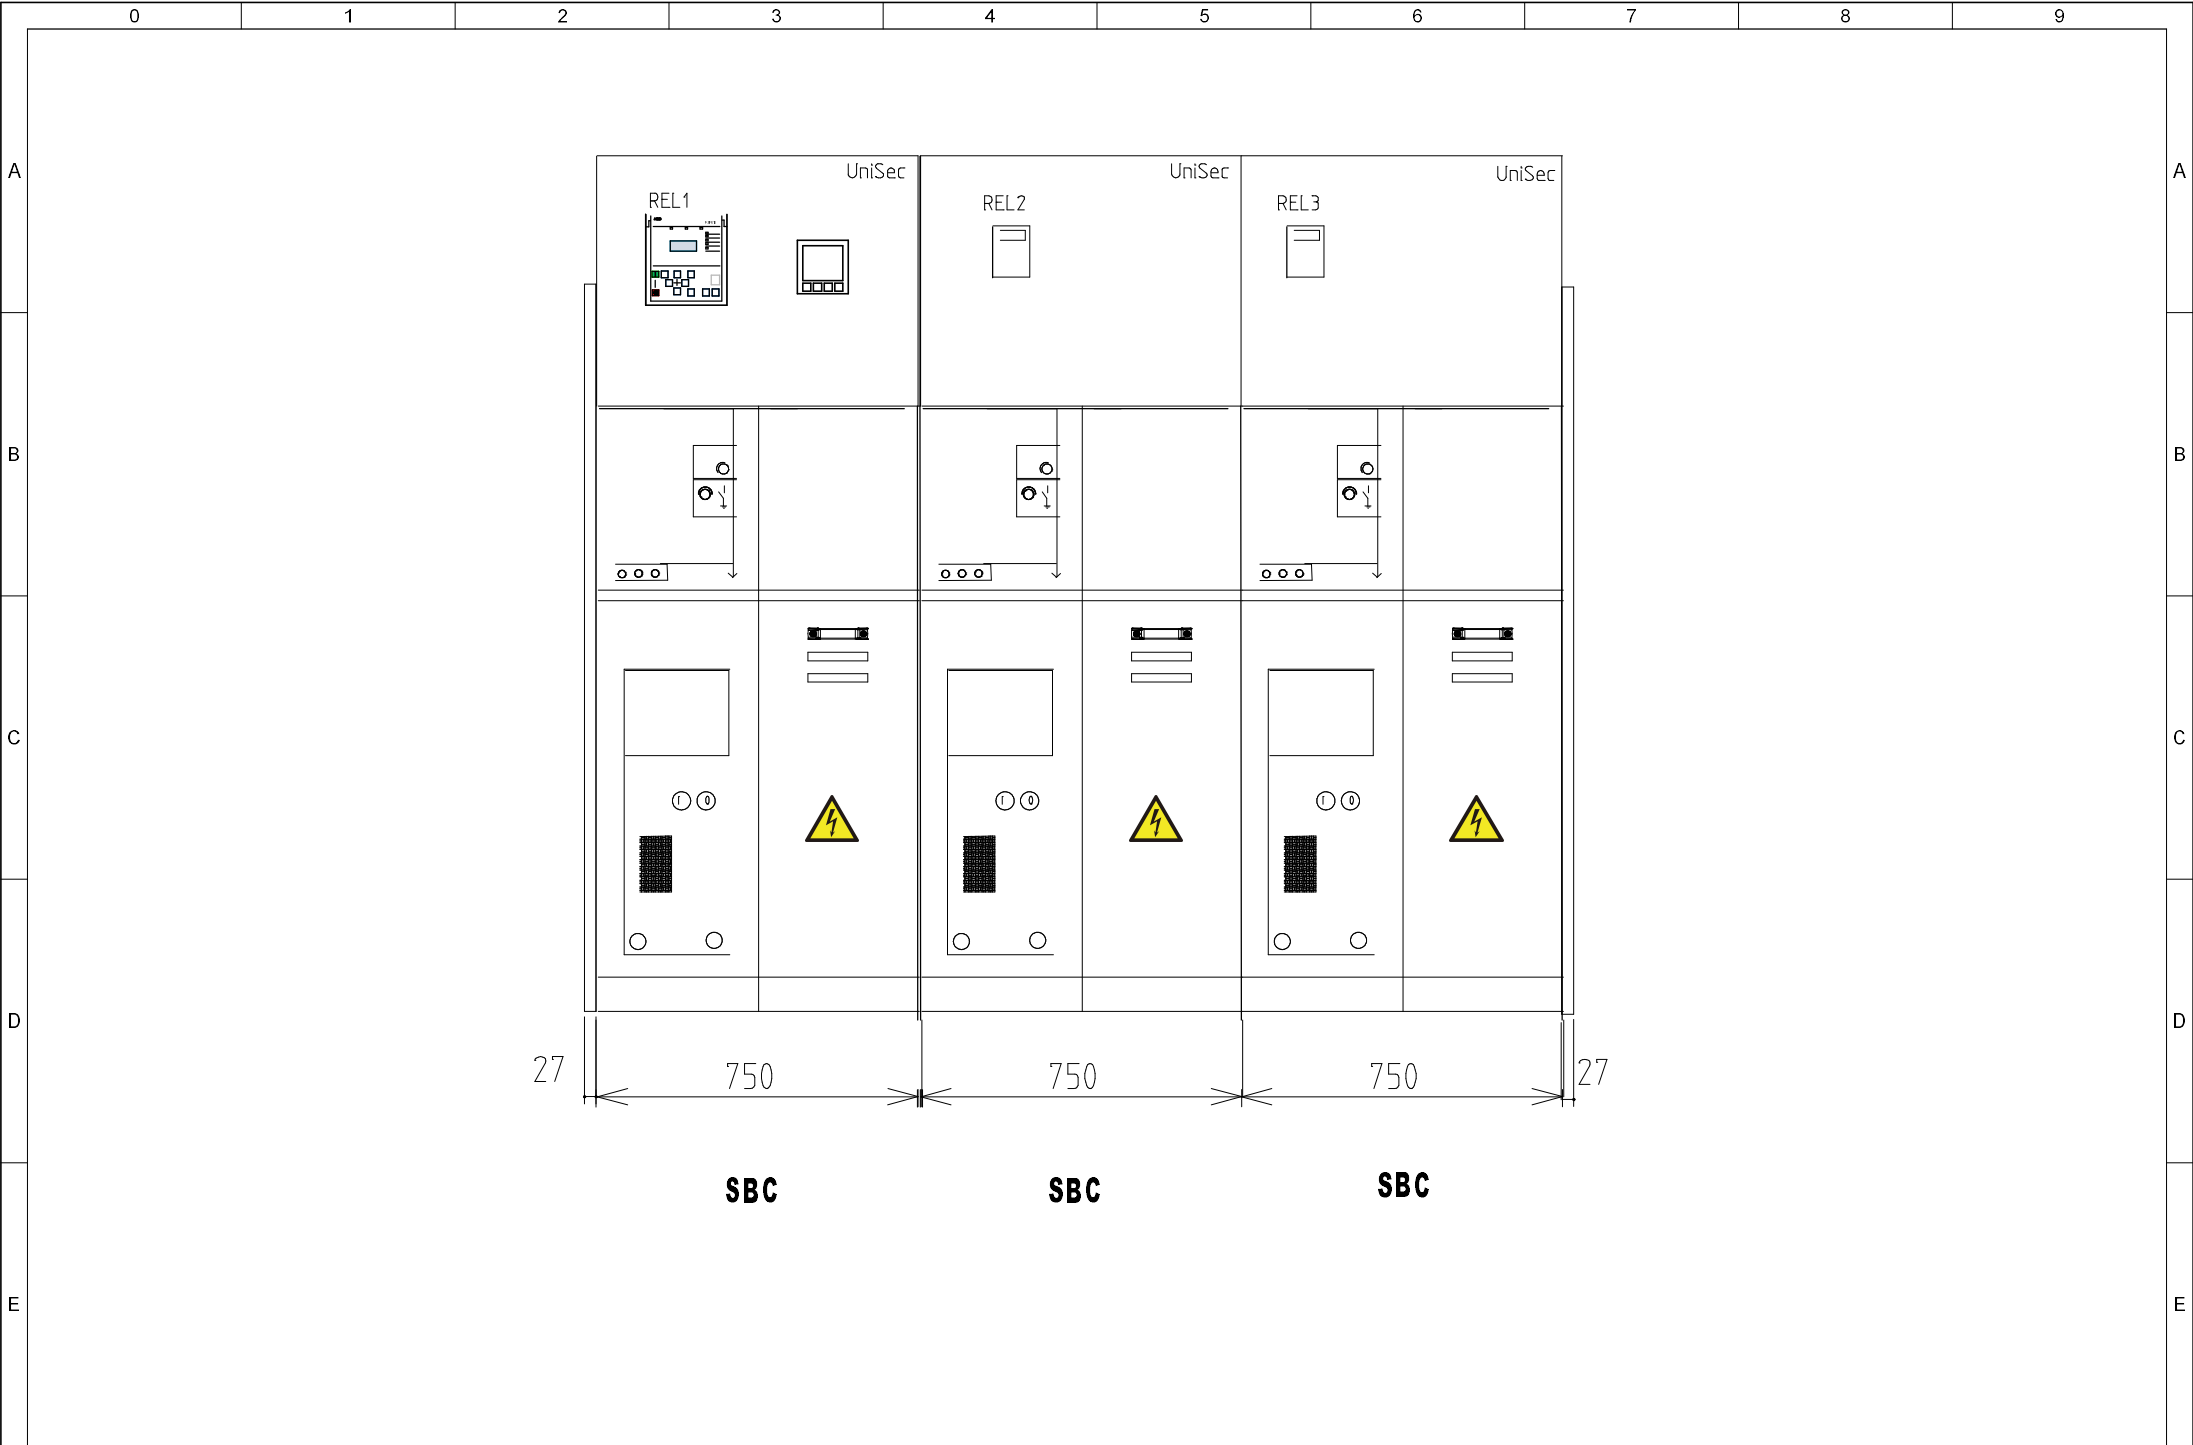


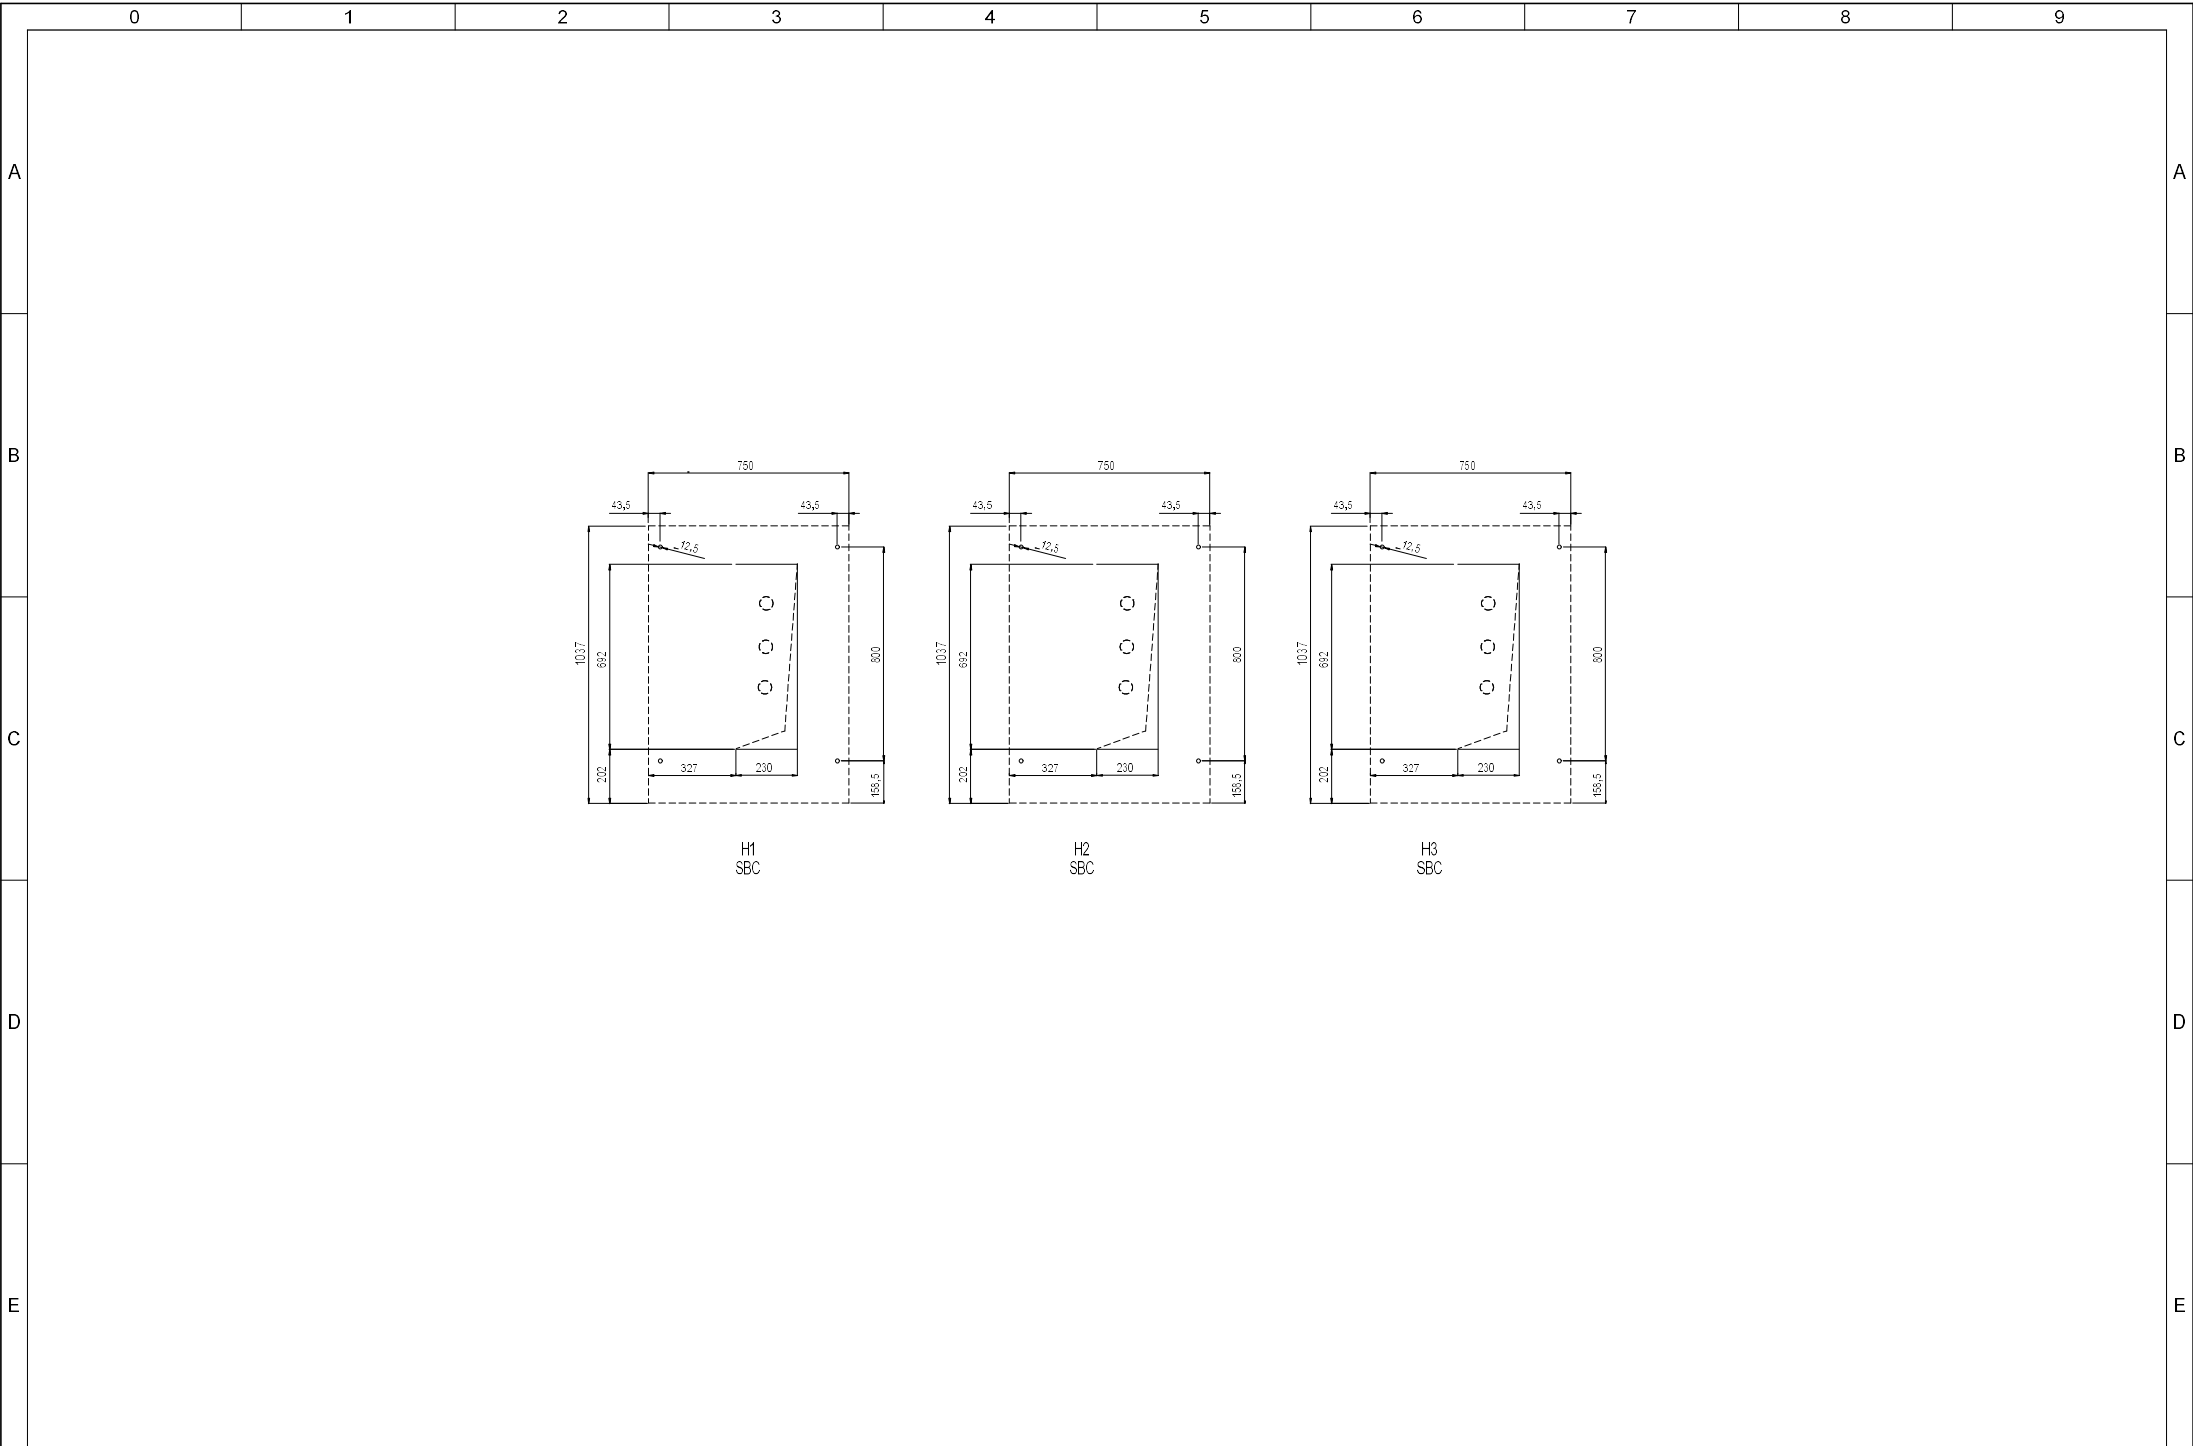



Studied	ILVIEF	Date	07/01/2022	ELECTRICAL INDUSTRIAL APPLICATIONS 1ST INDUSTRIAL AREA OF VOLOS mail: info@ilvief.gr / website: www.ilvief.com	PROJECT: ANARITA 10MW	PAGE DESCRIPTION: BASE VIEW	DRAWING NUMBER:	PAGE: 3
Drawn	A. ALEXIOU		20/02/2023					
Approved	ILVIEF SA		20/02/2023		CUSTOMER: ERGO HOME ENERGY LTD		- of: 30	


SEE FILE: ANARITA MV PANEL

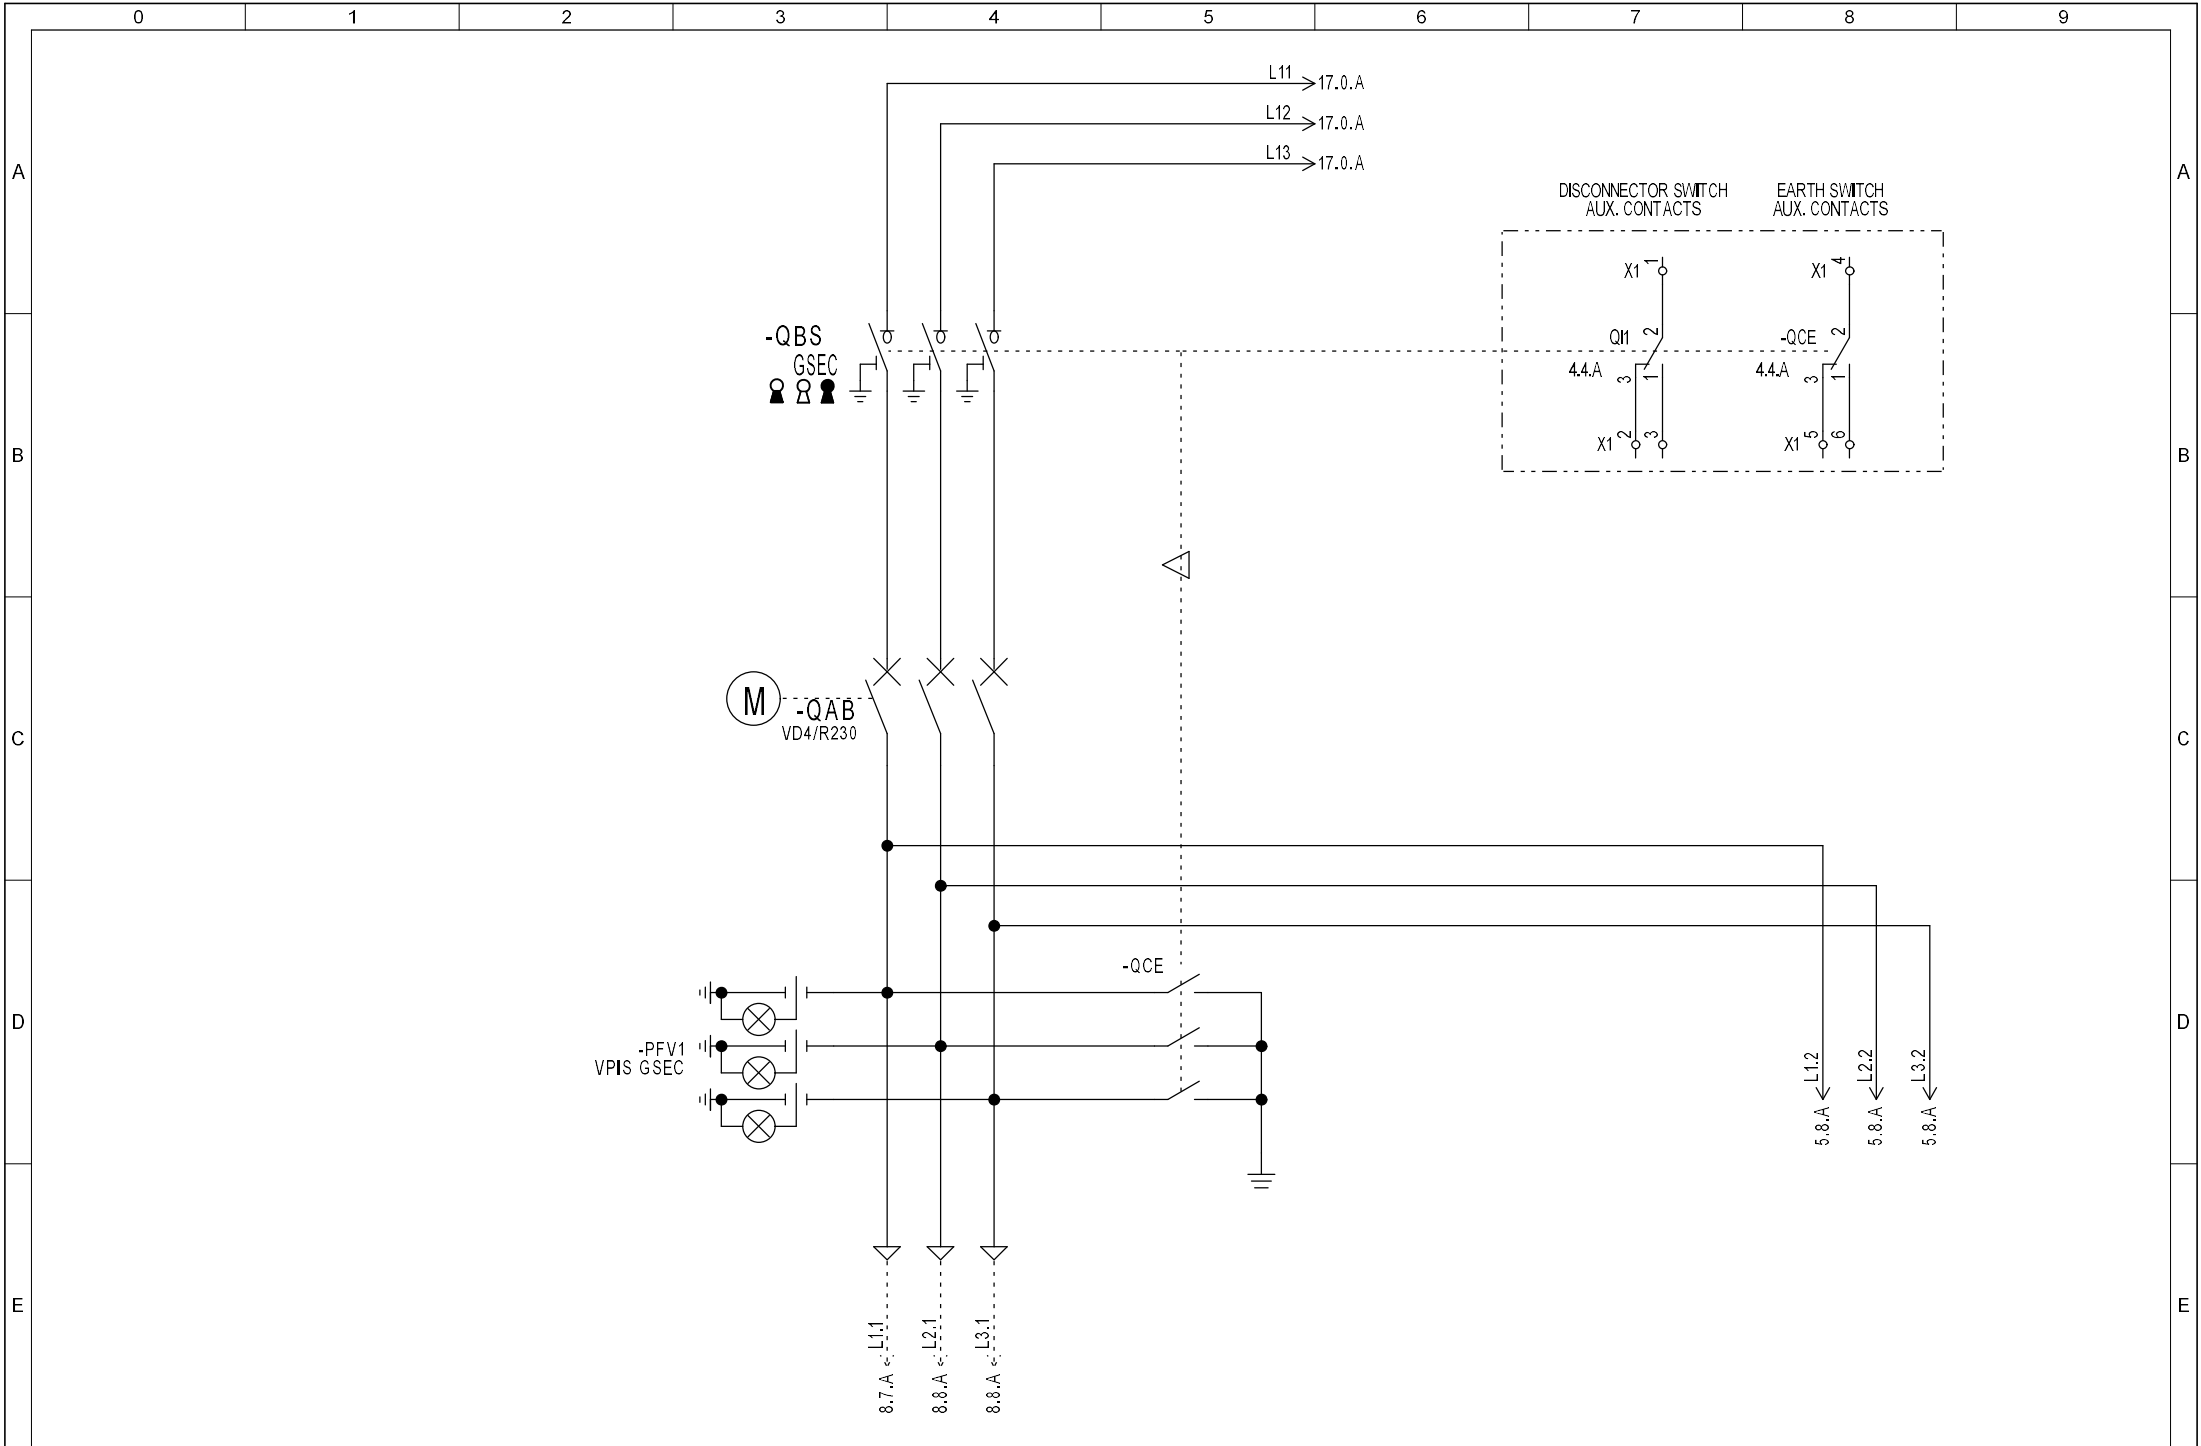


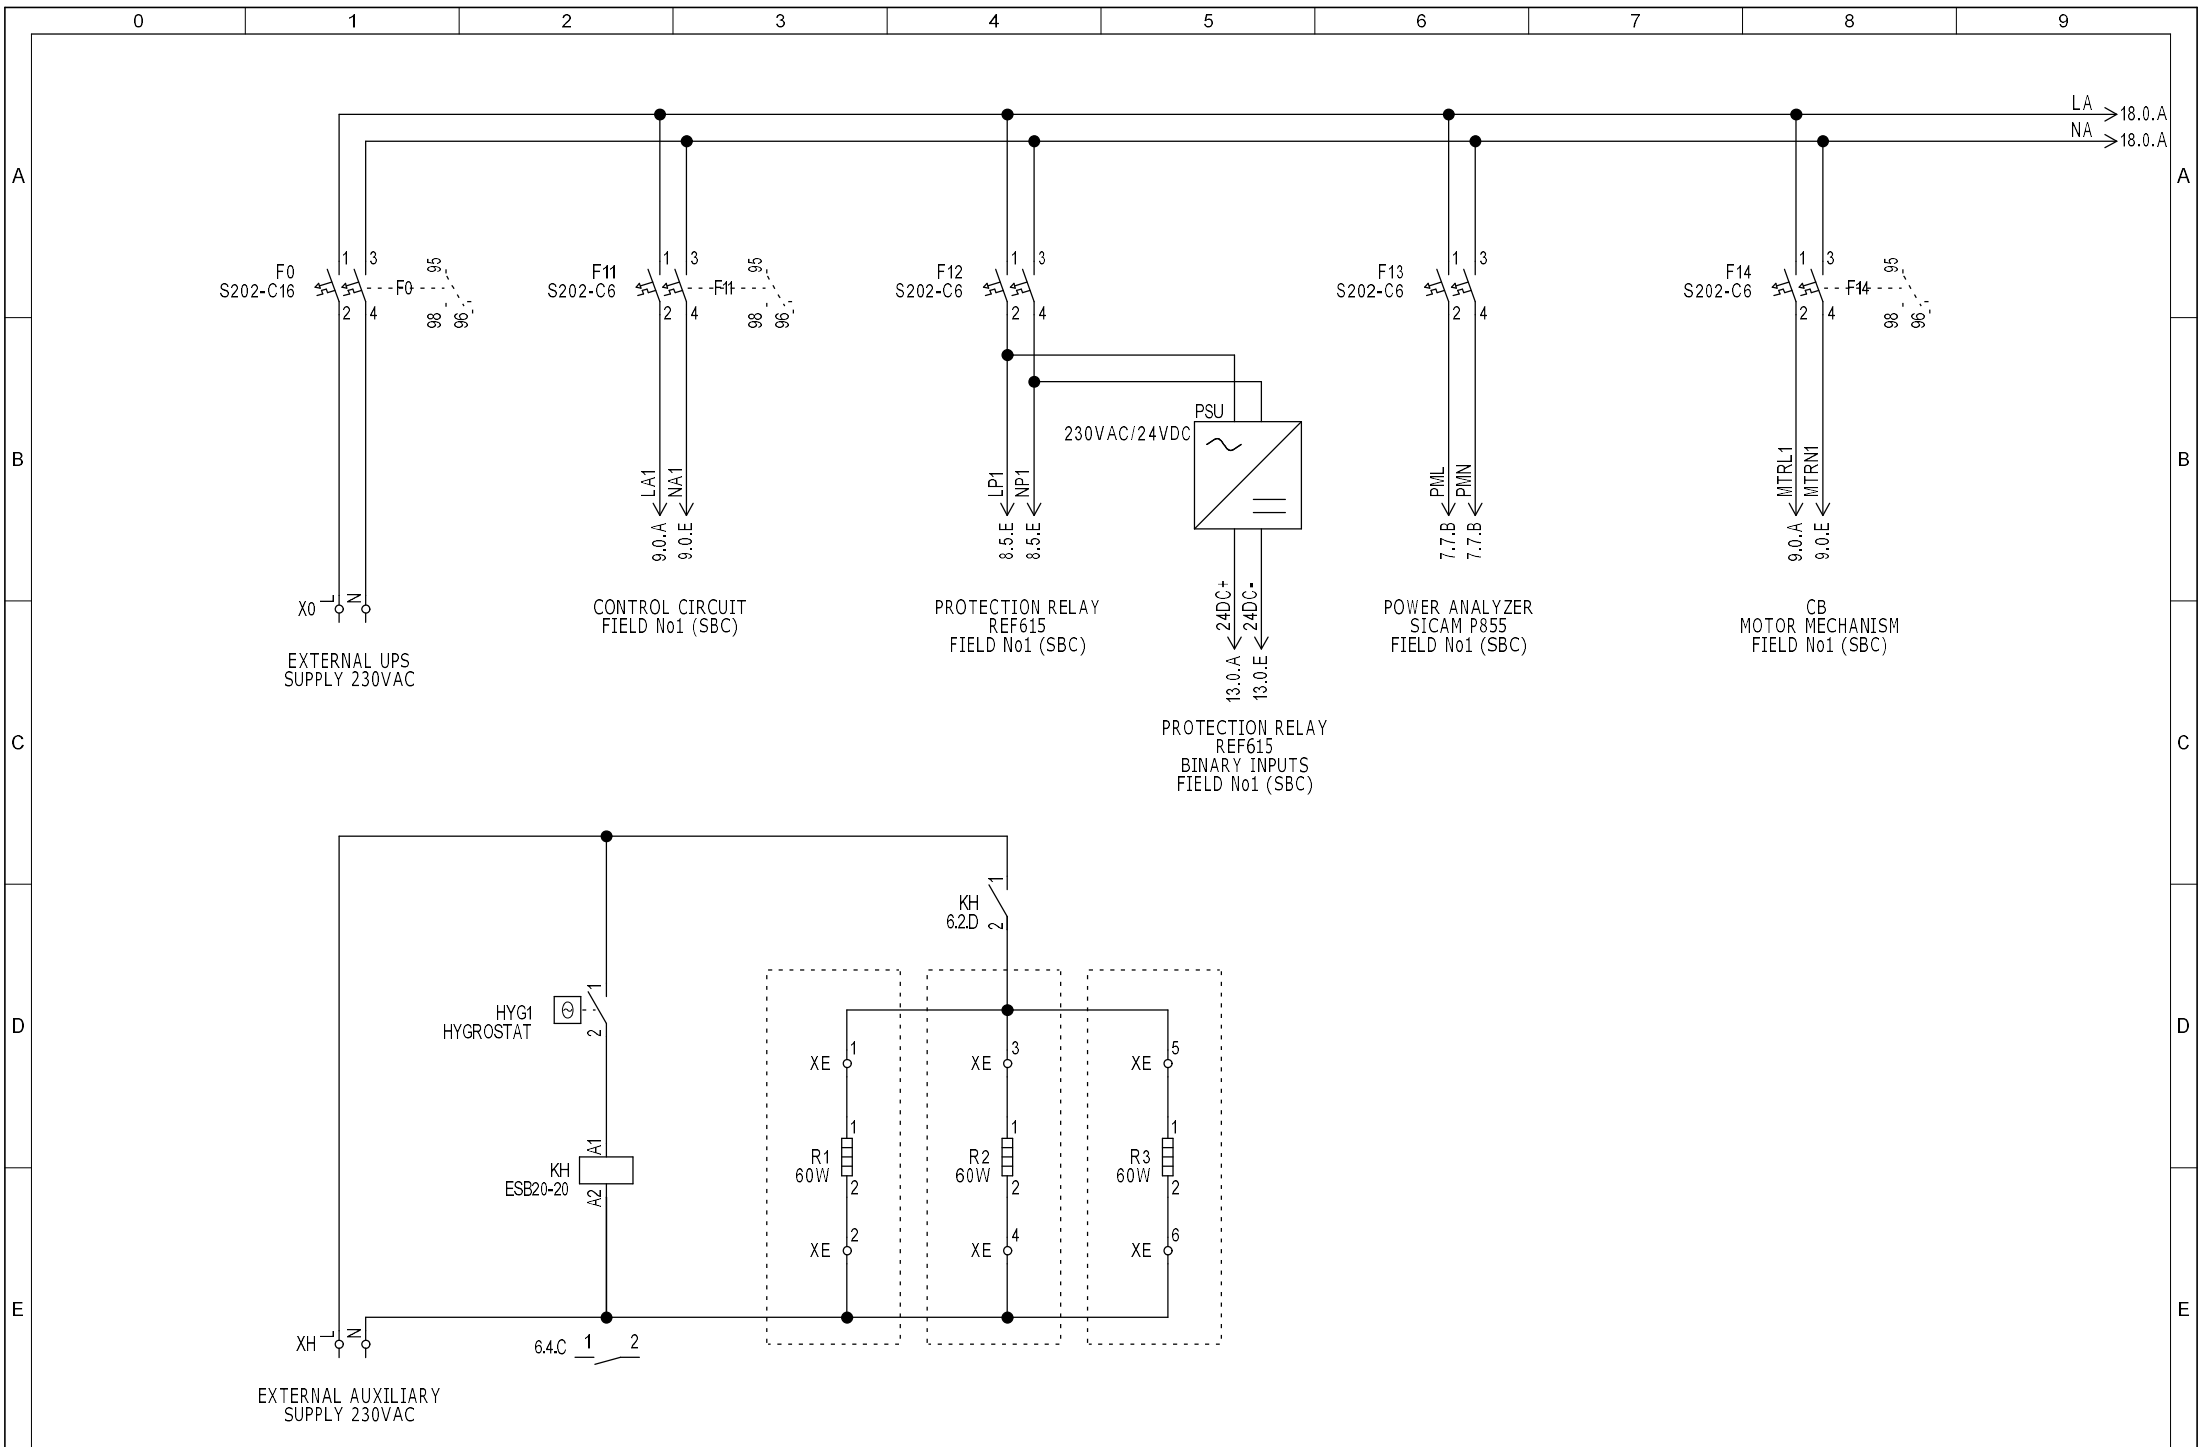


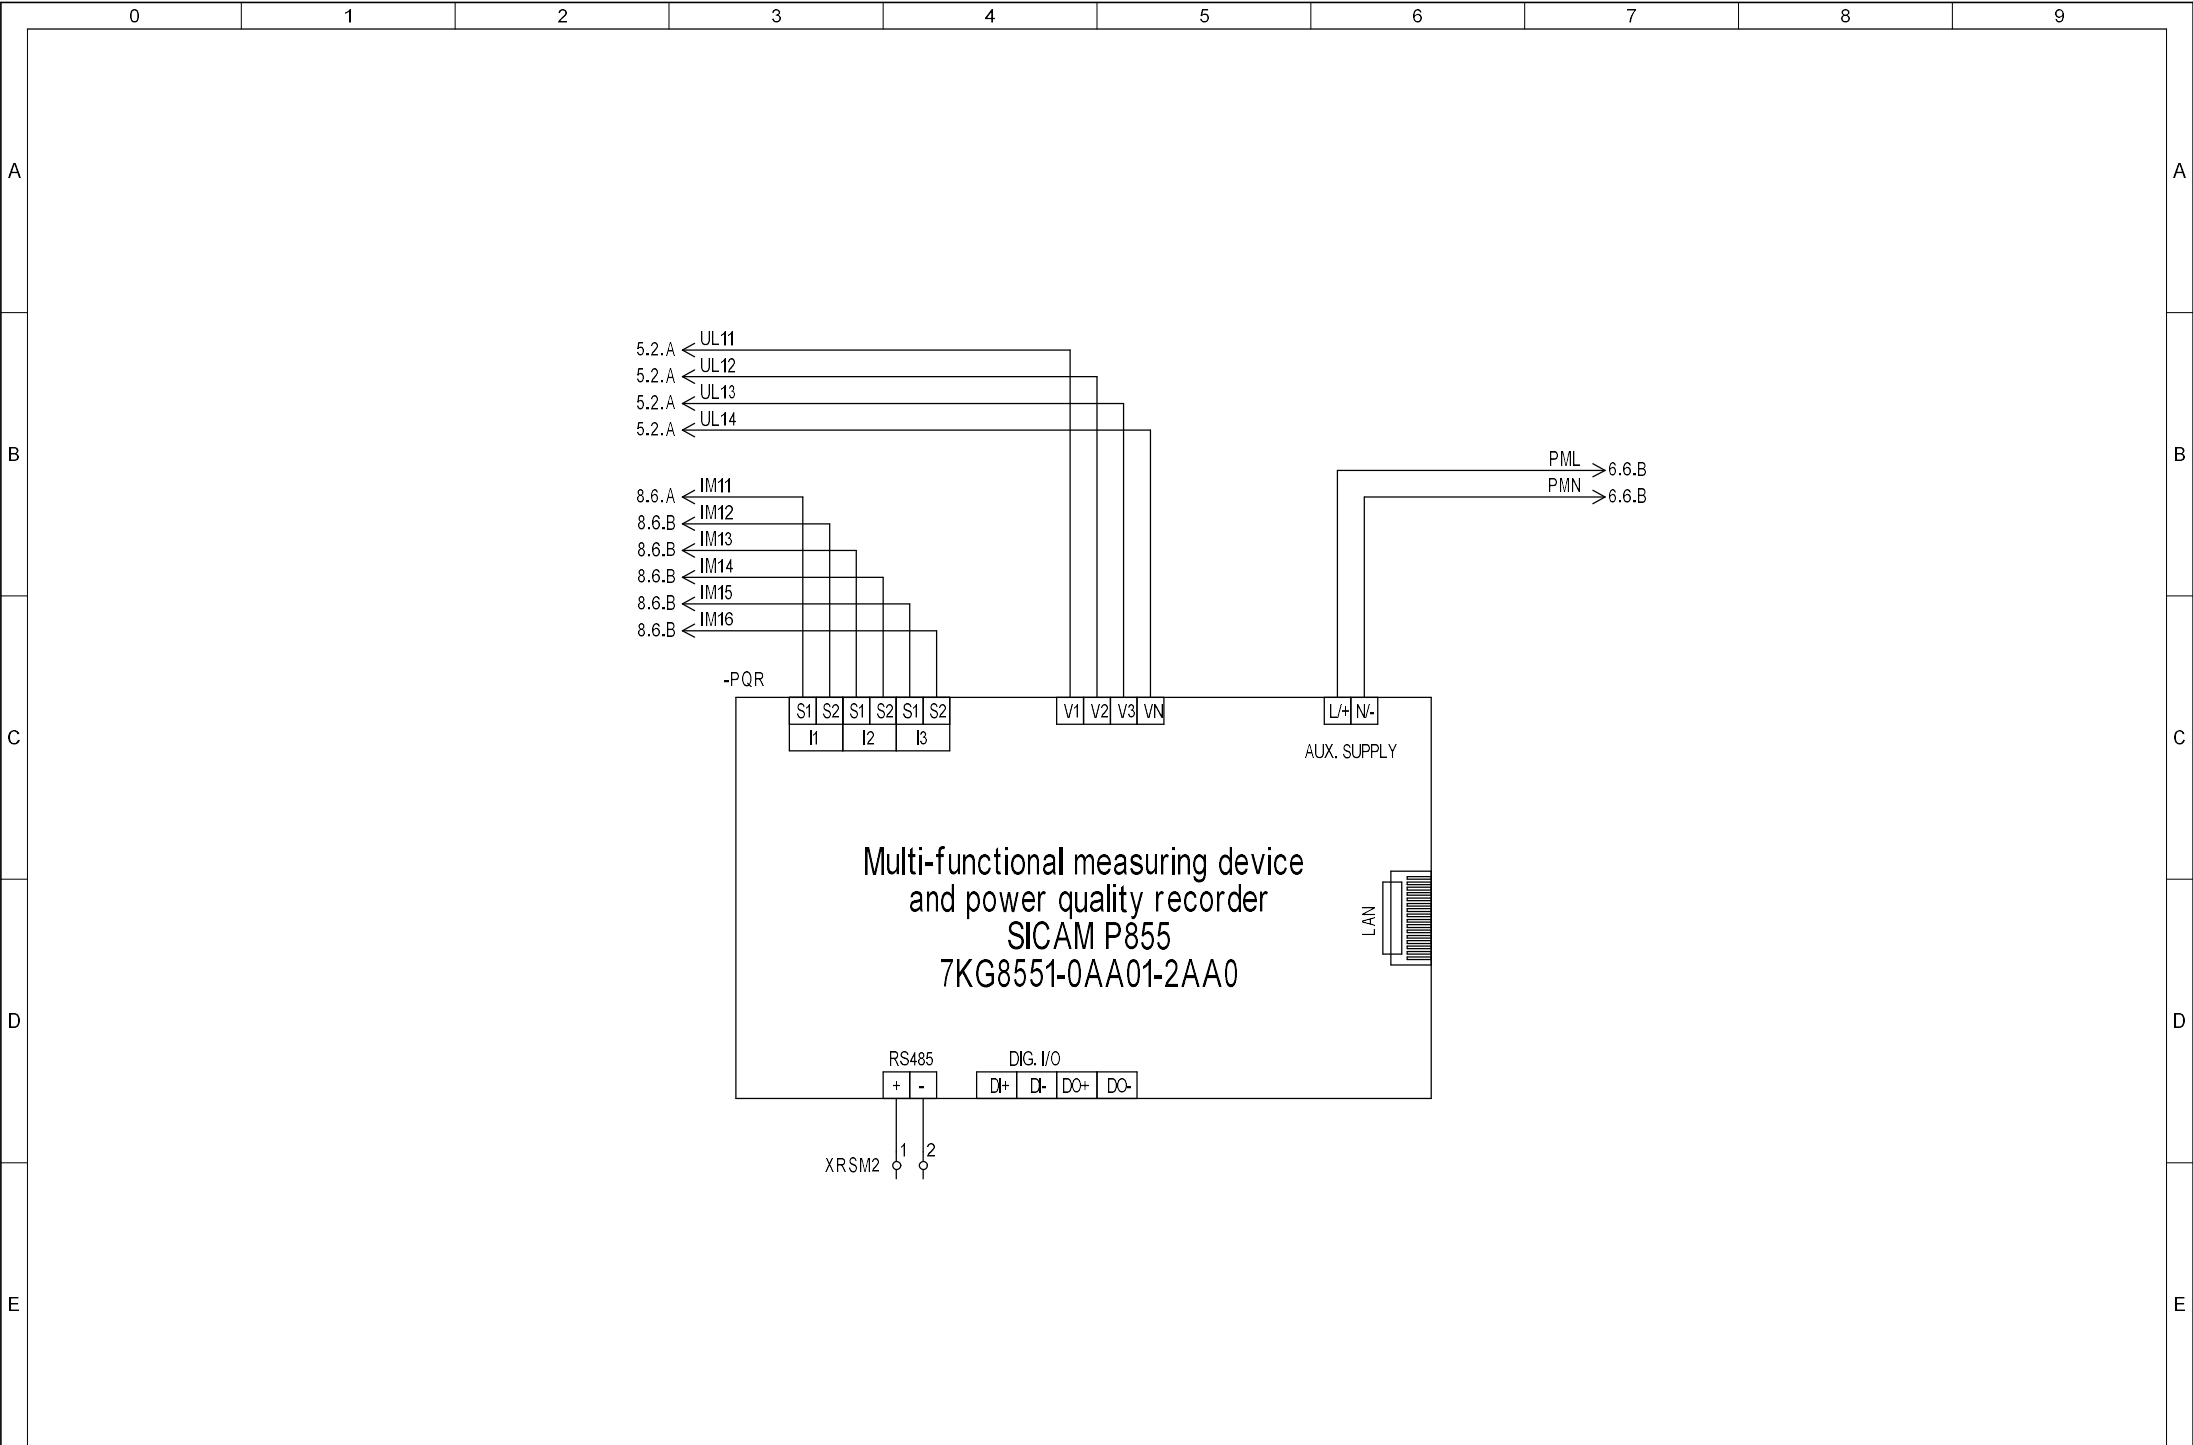


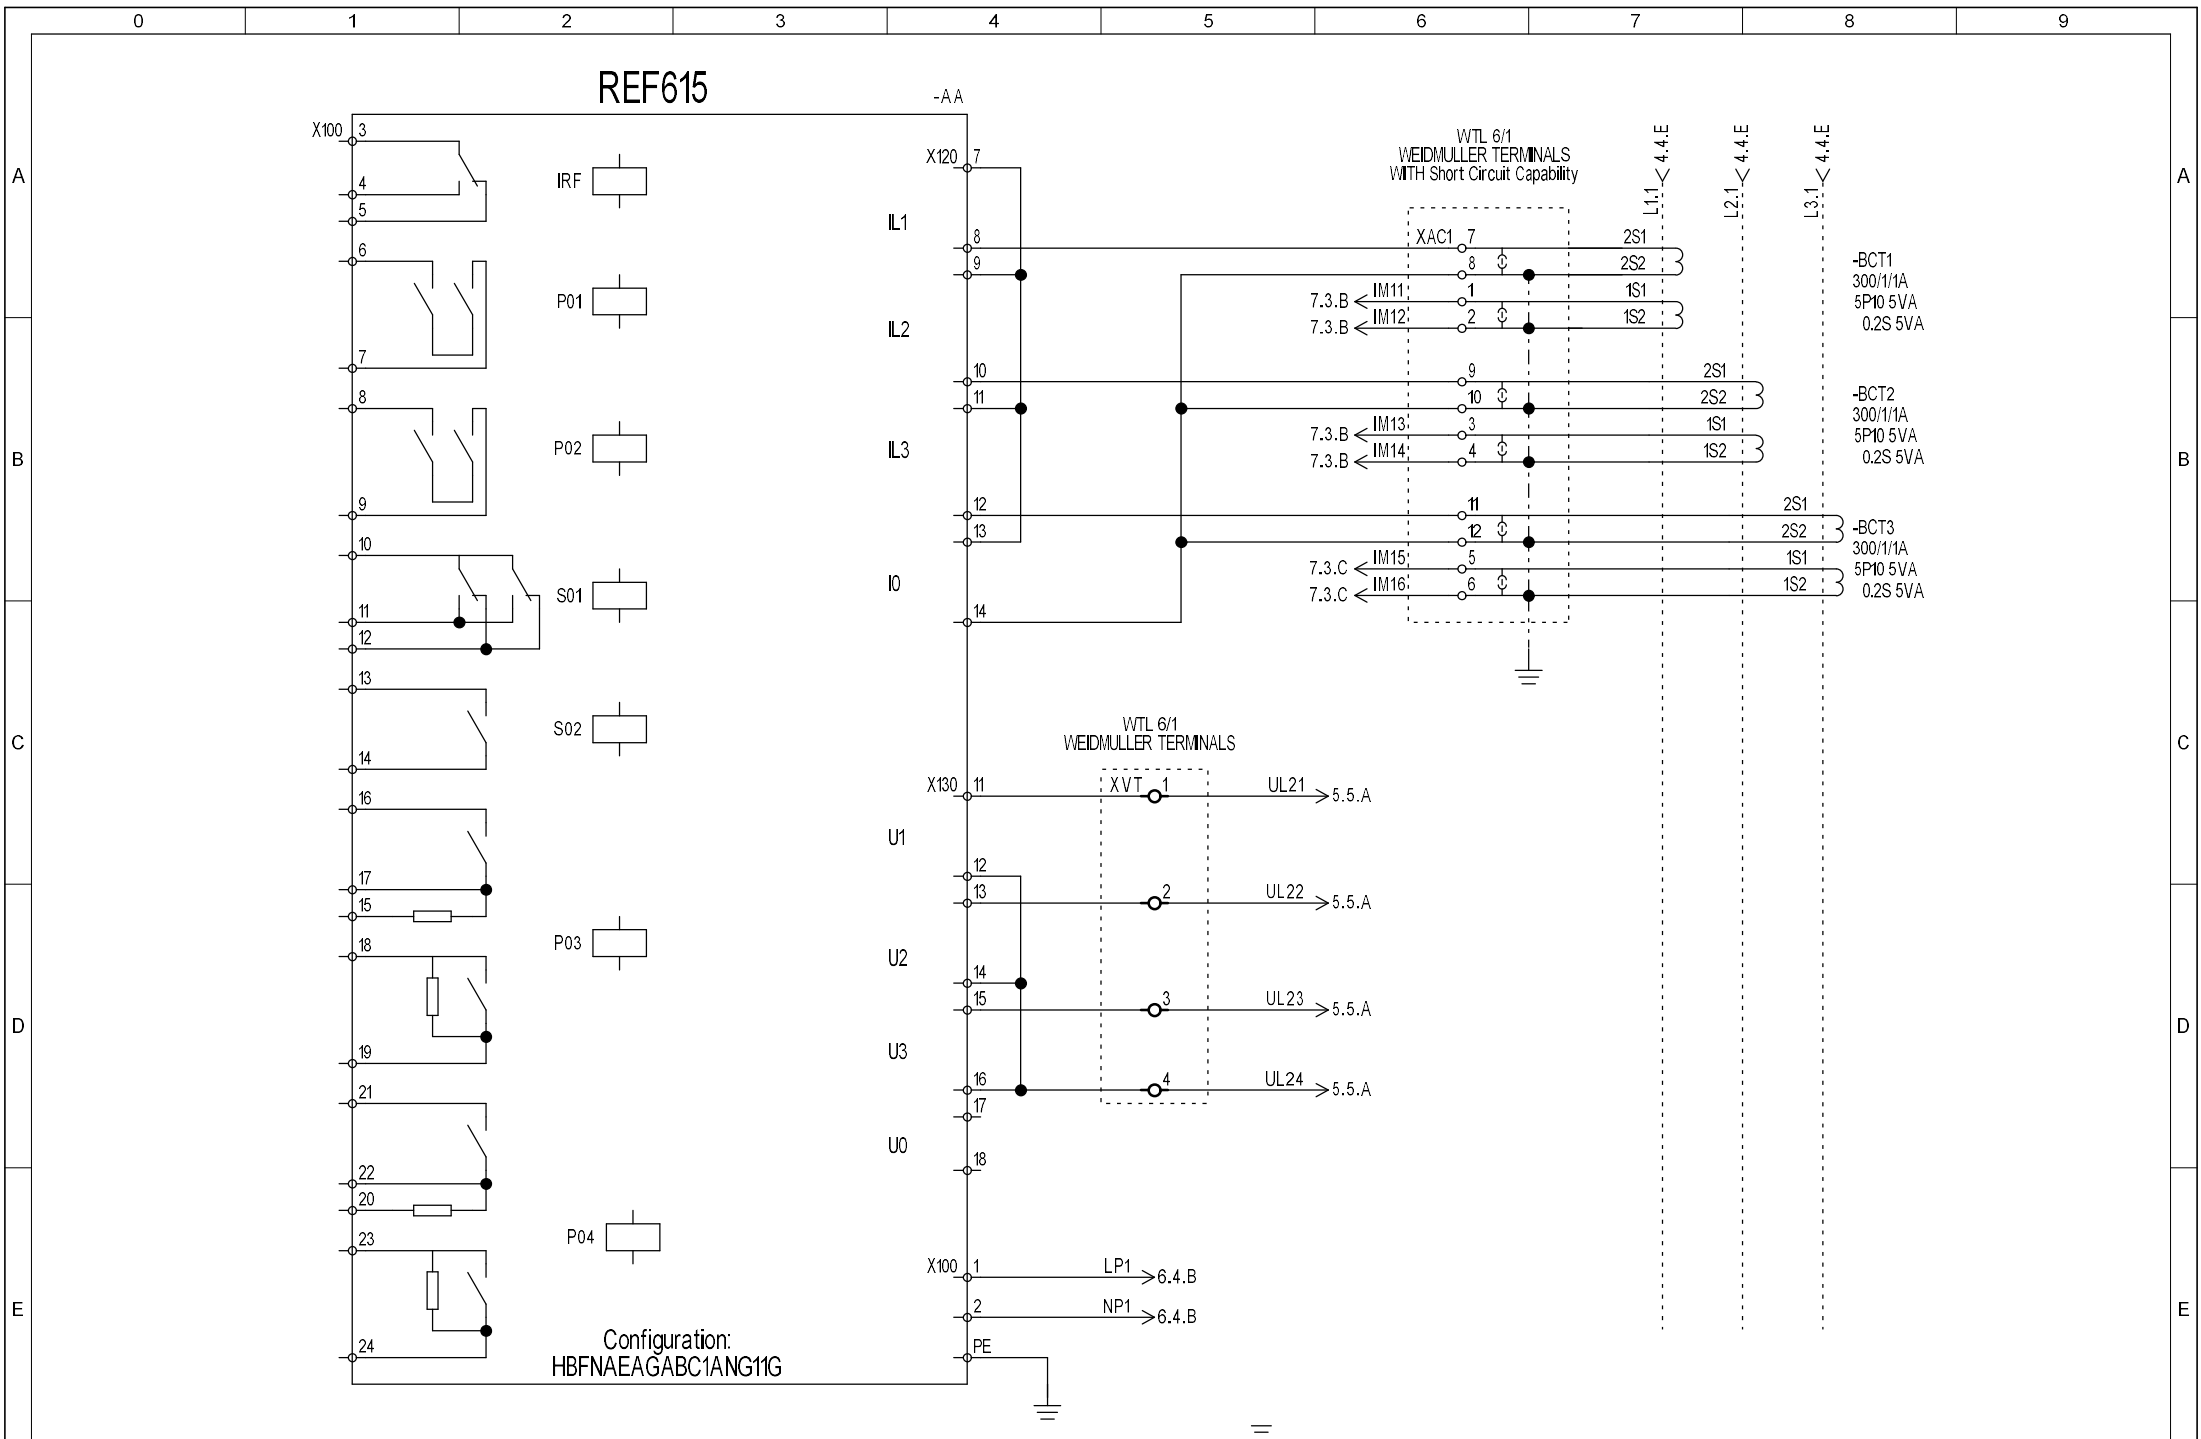


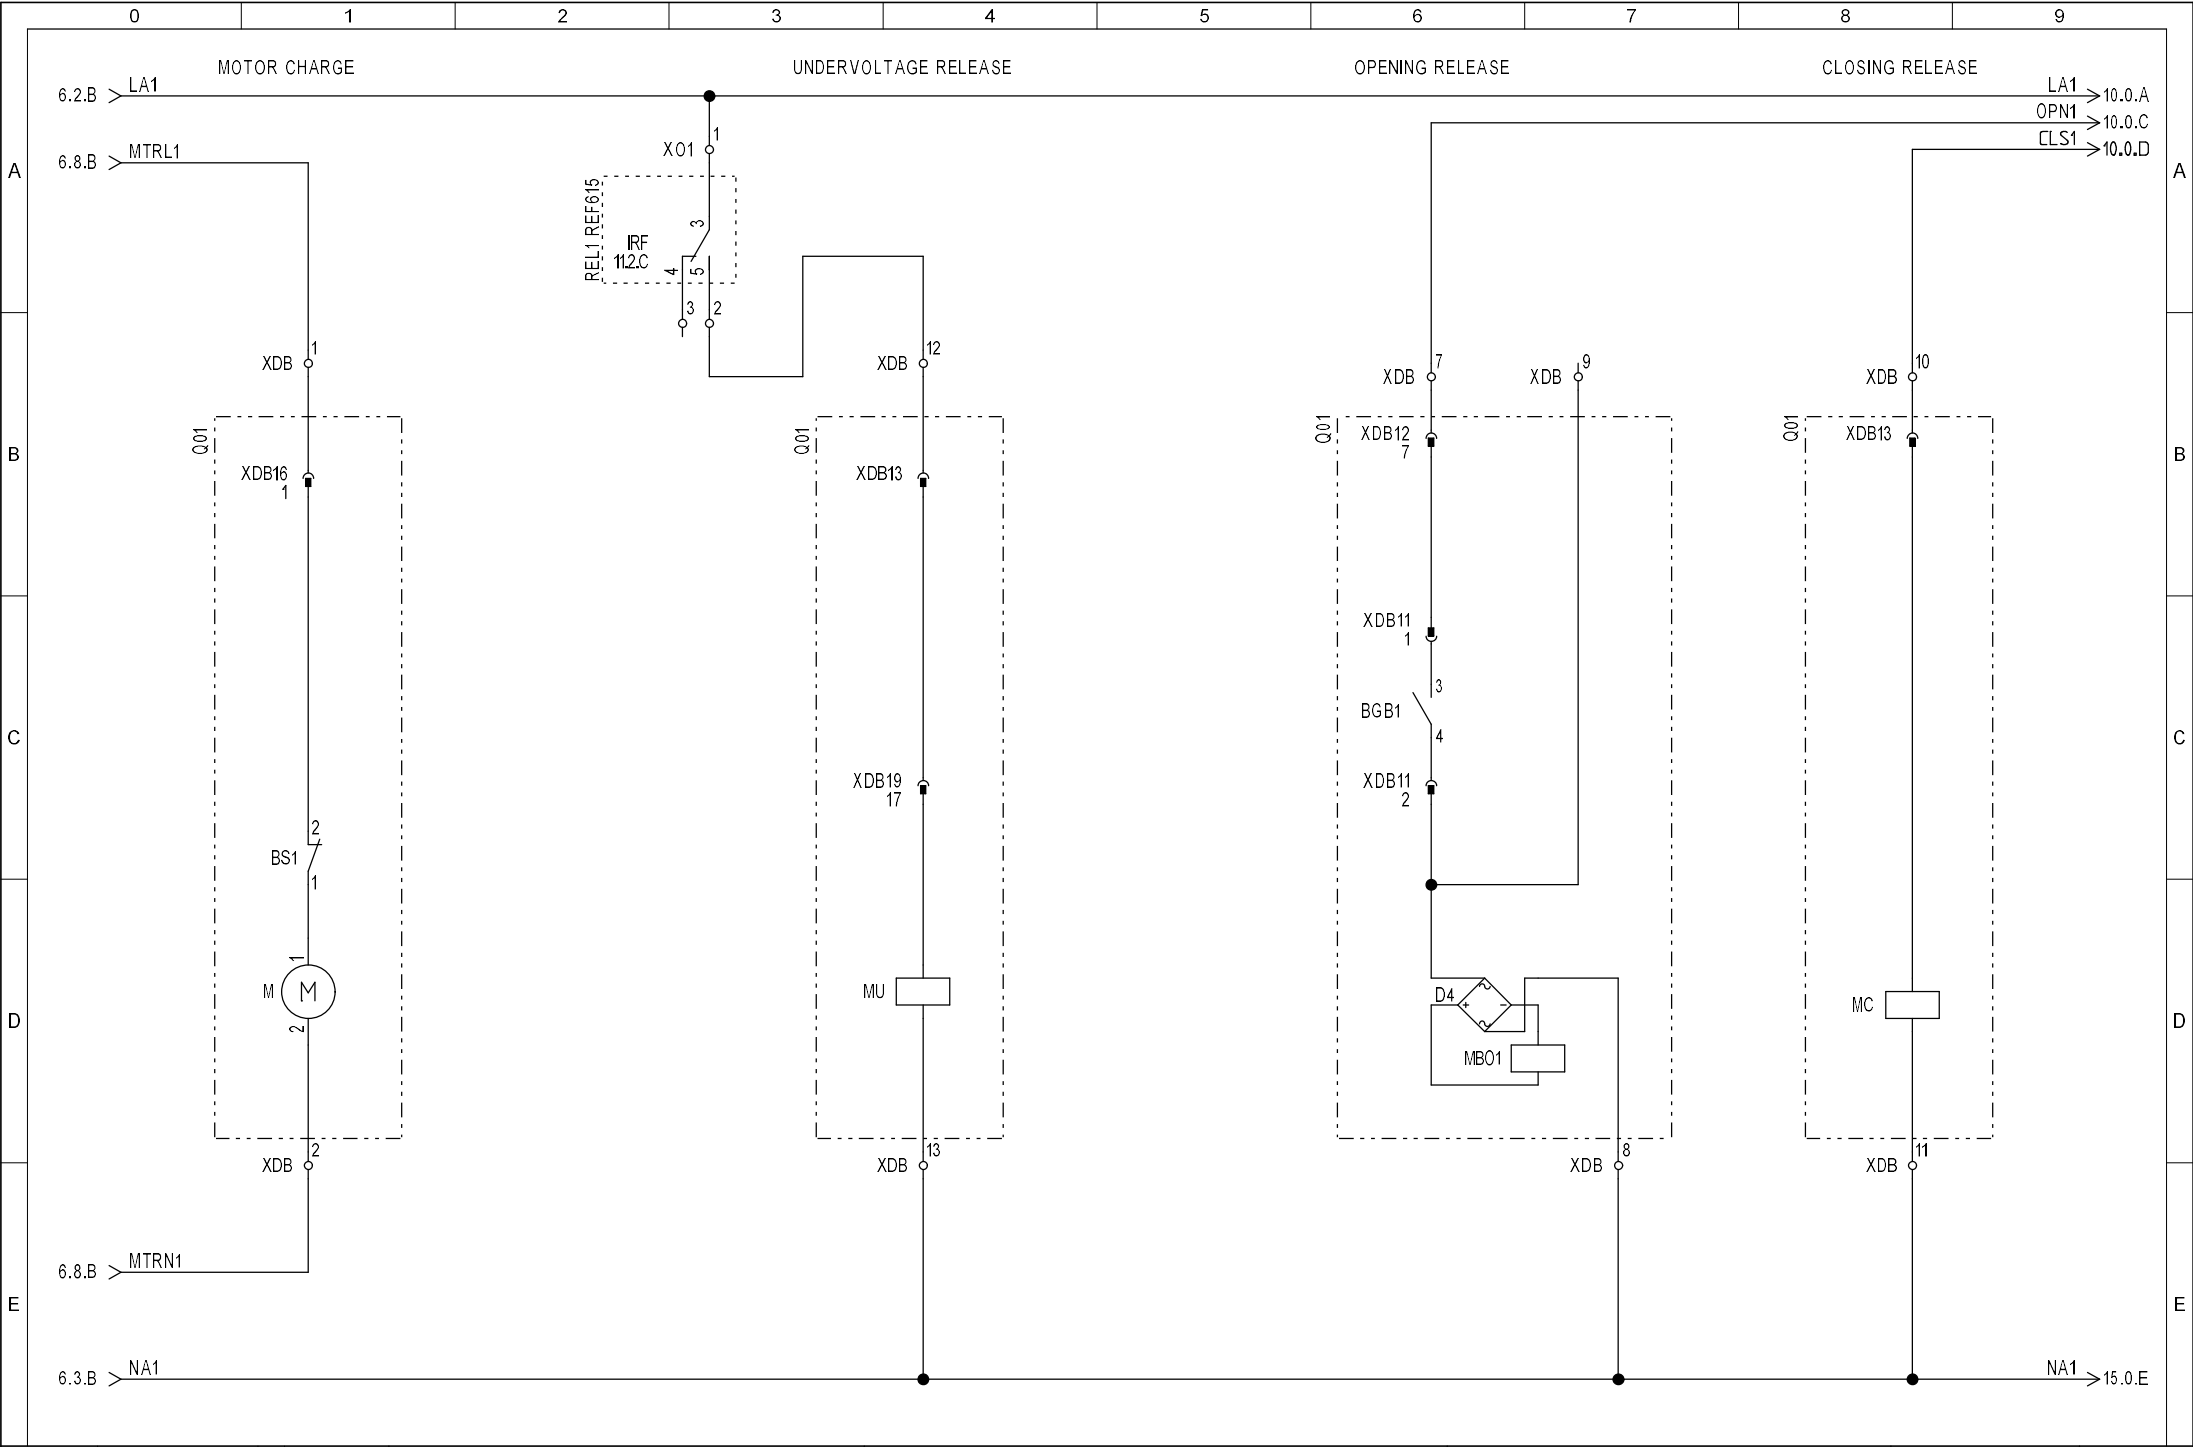


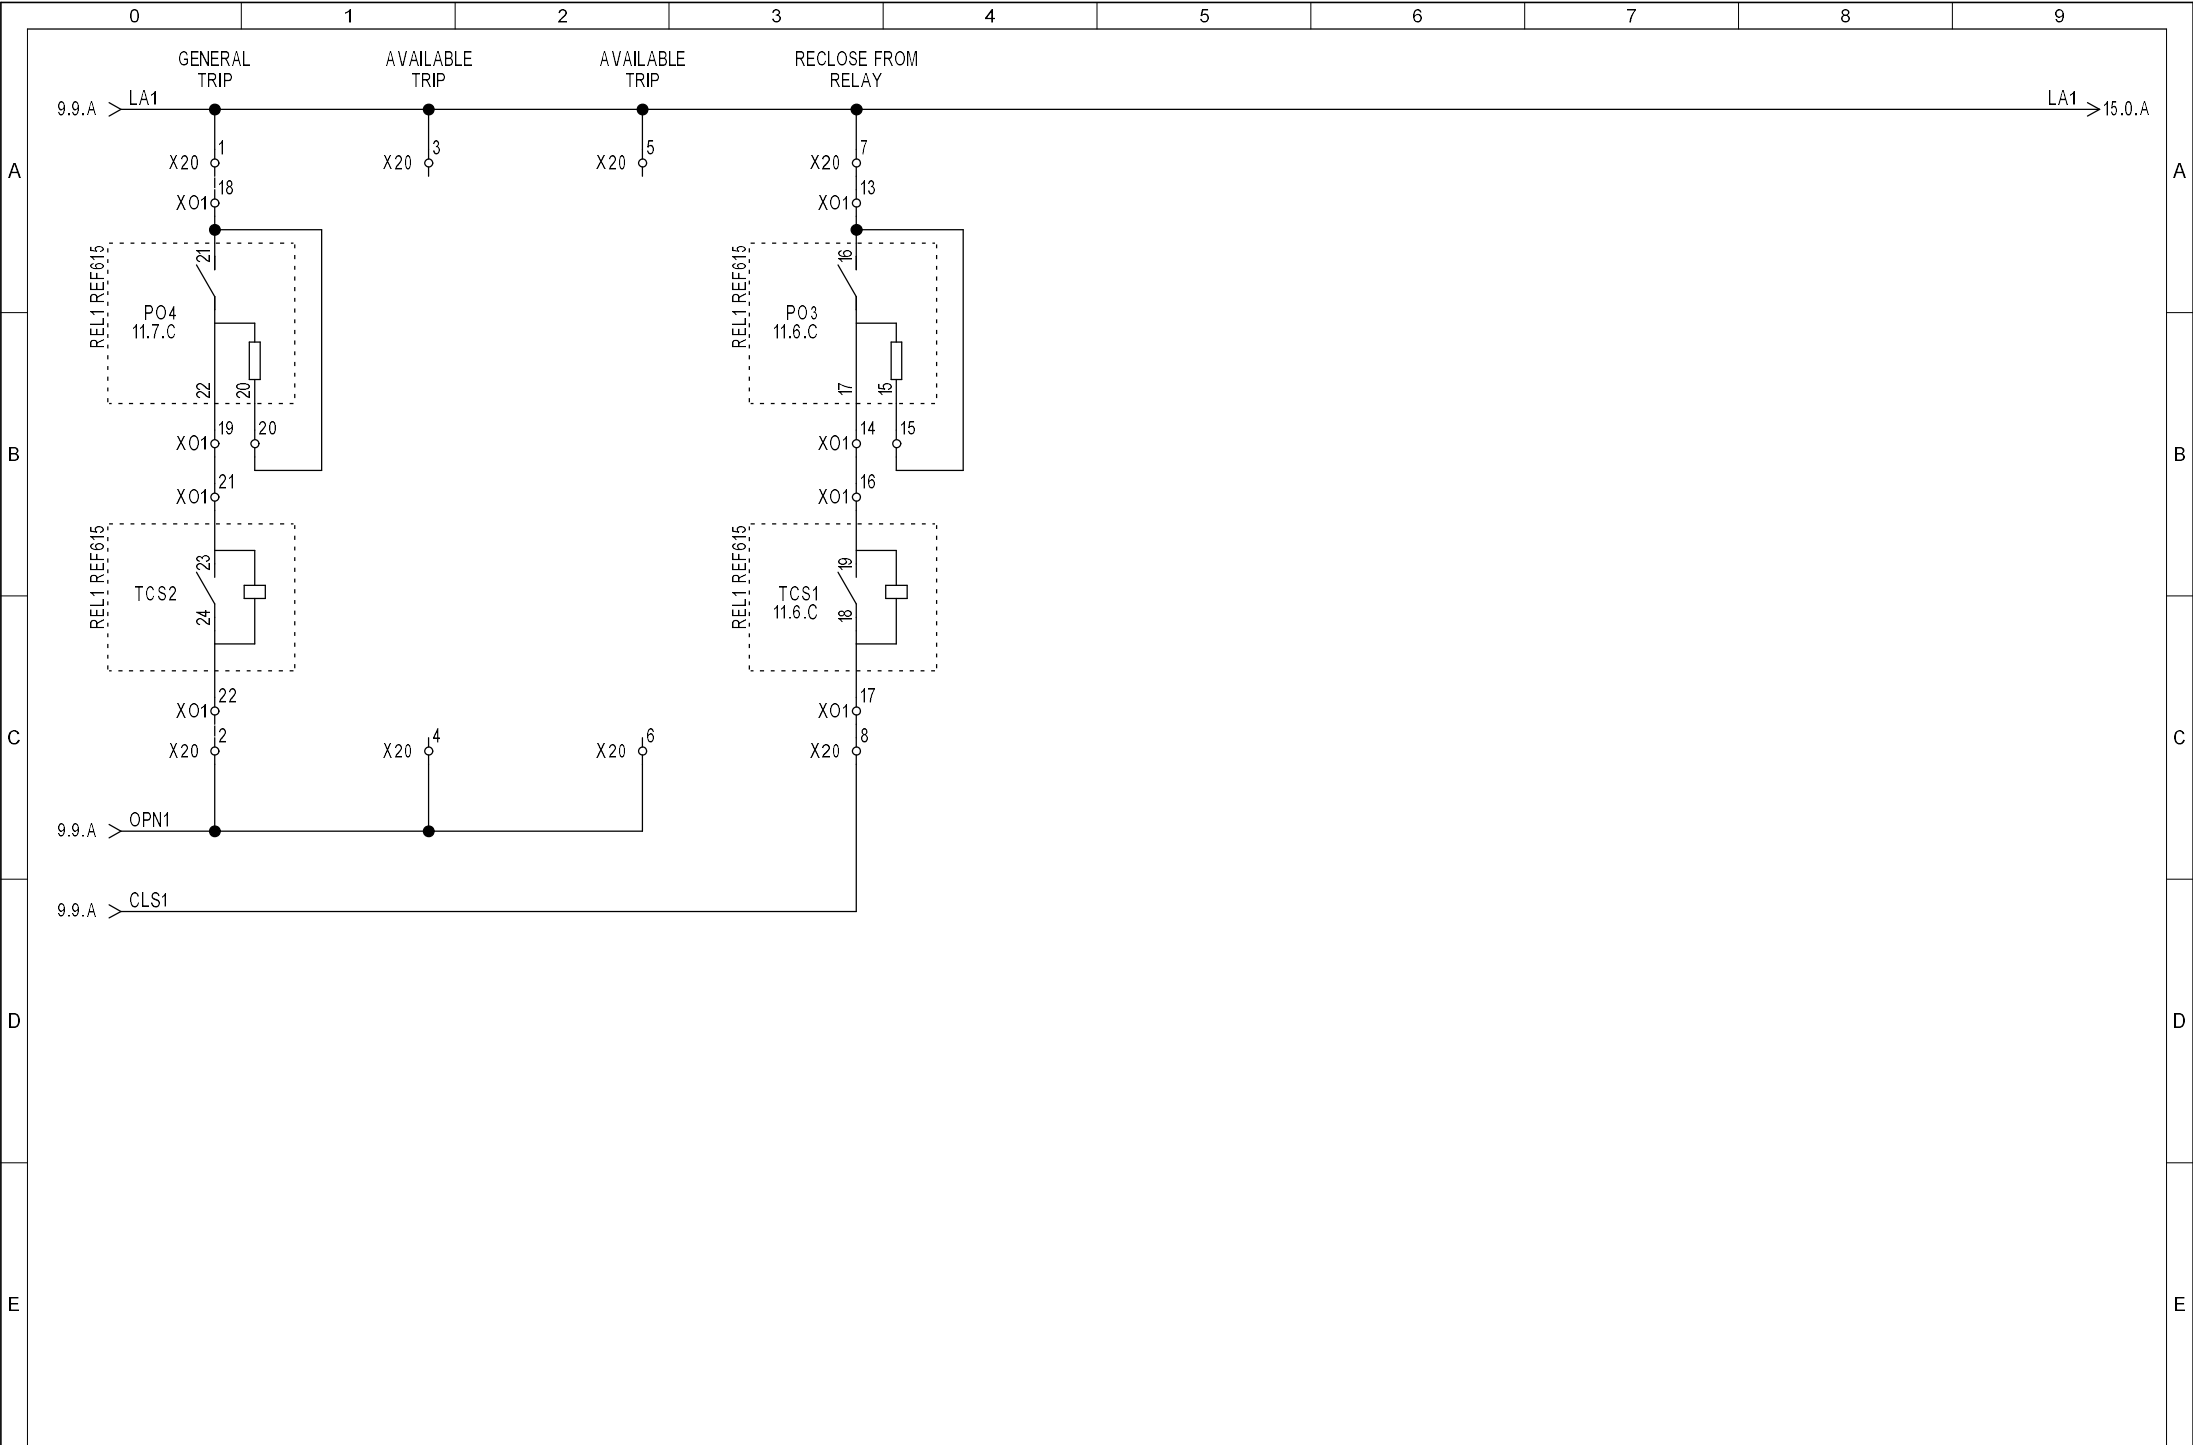


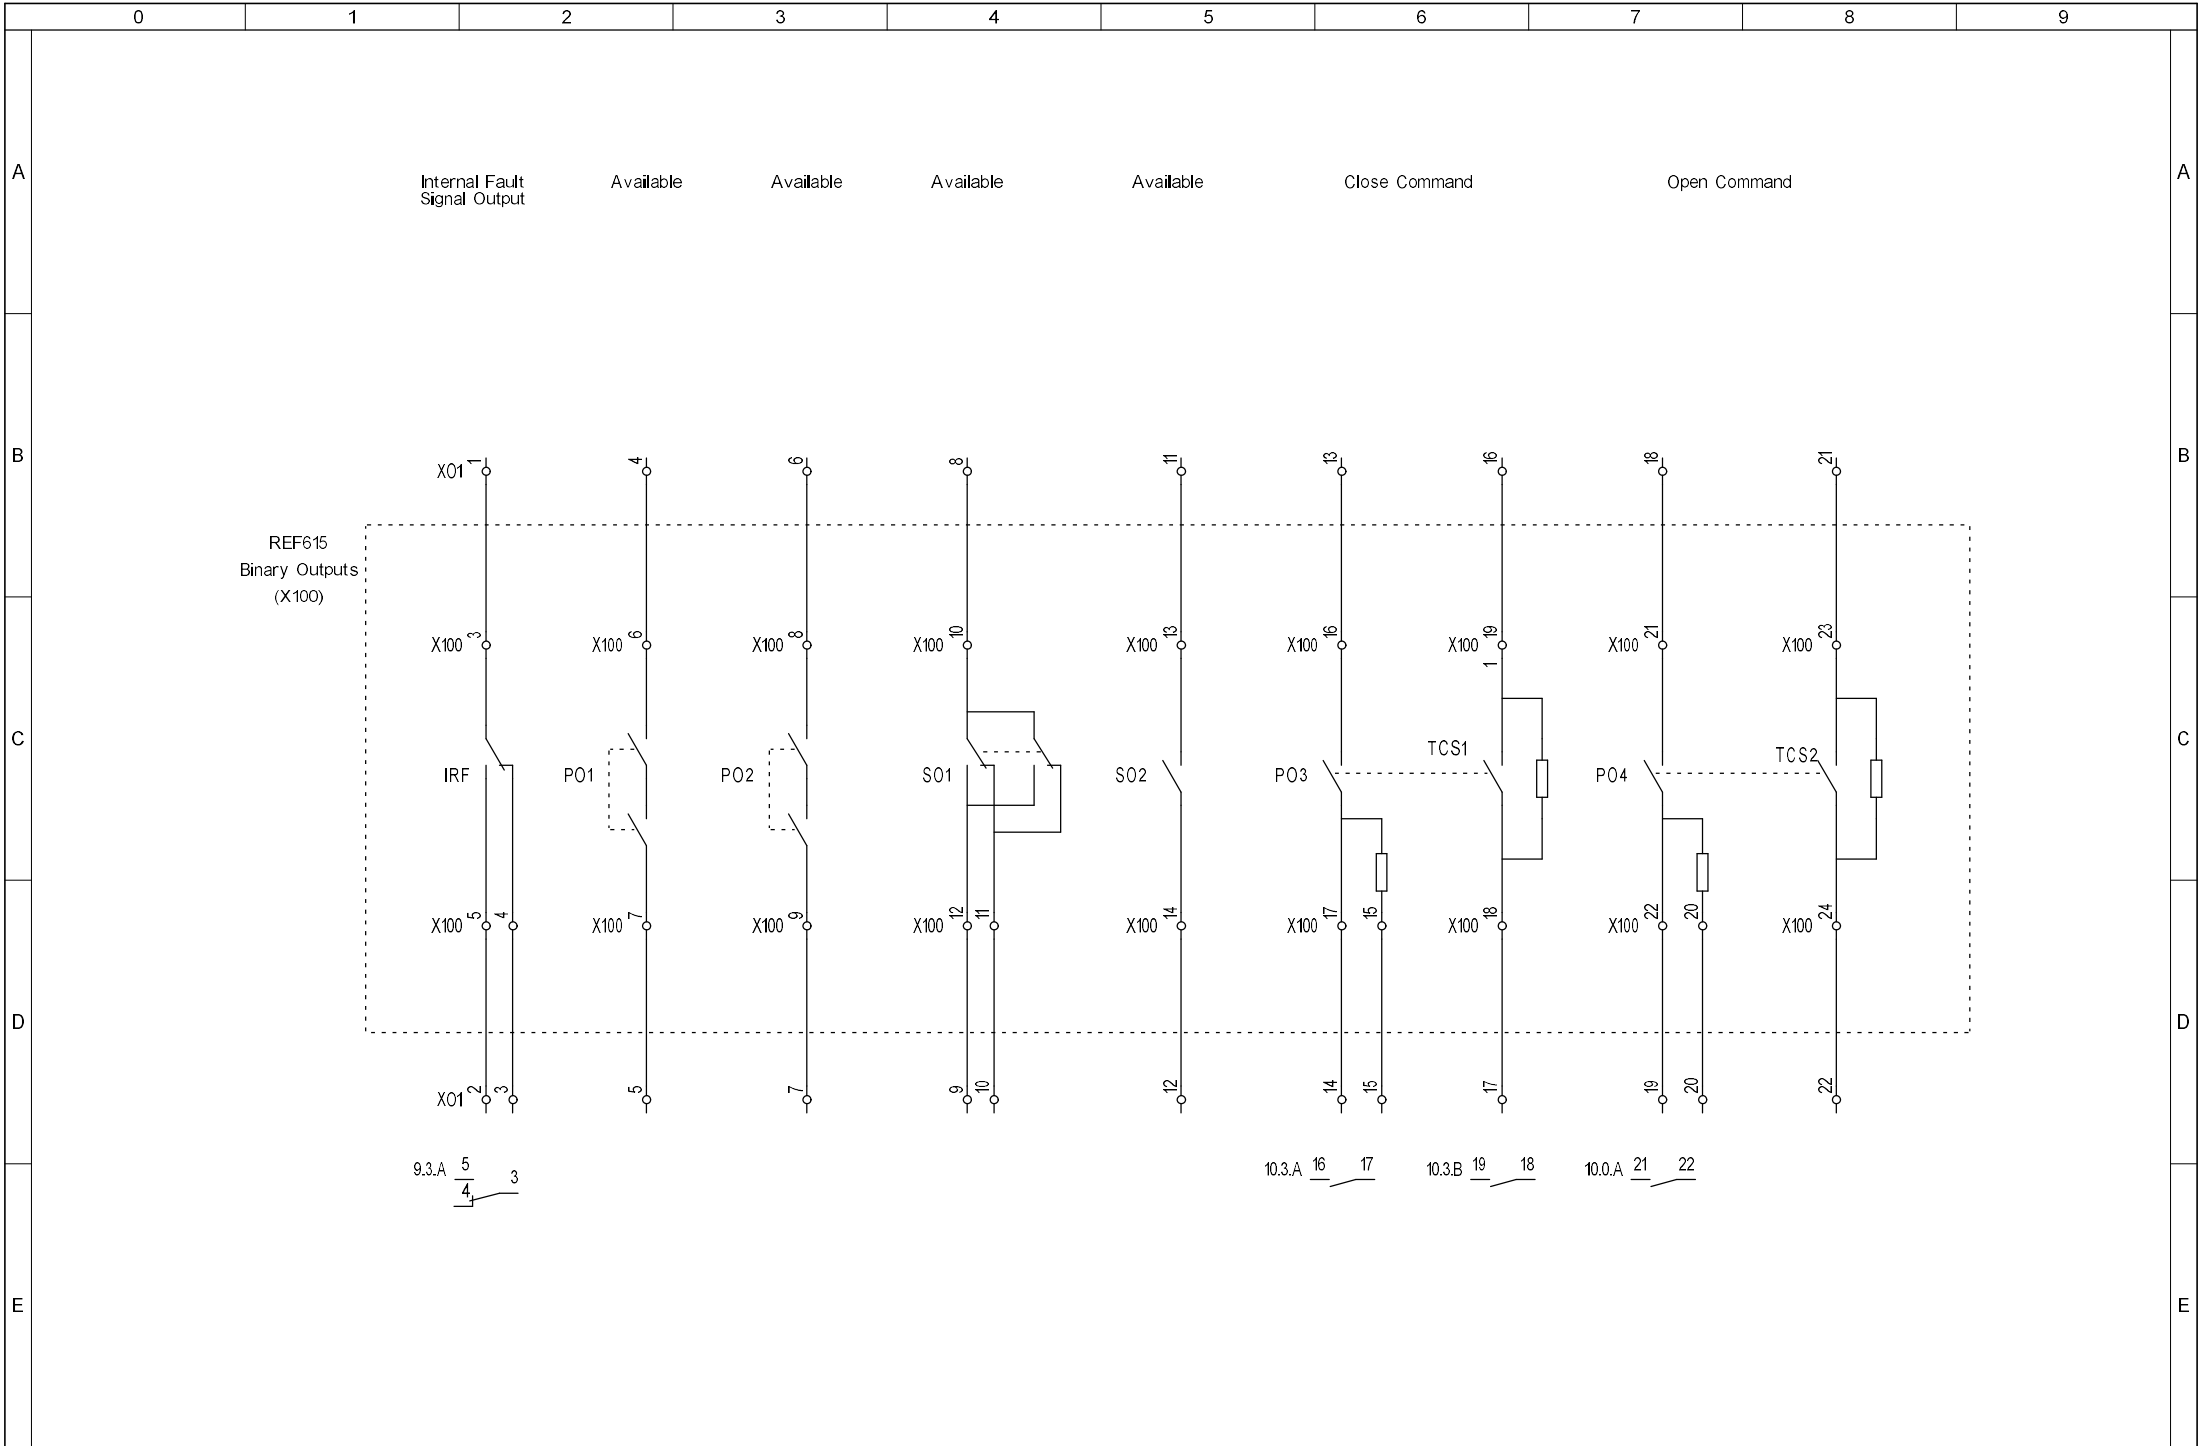


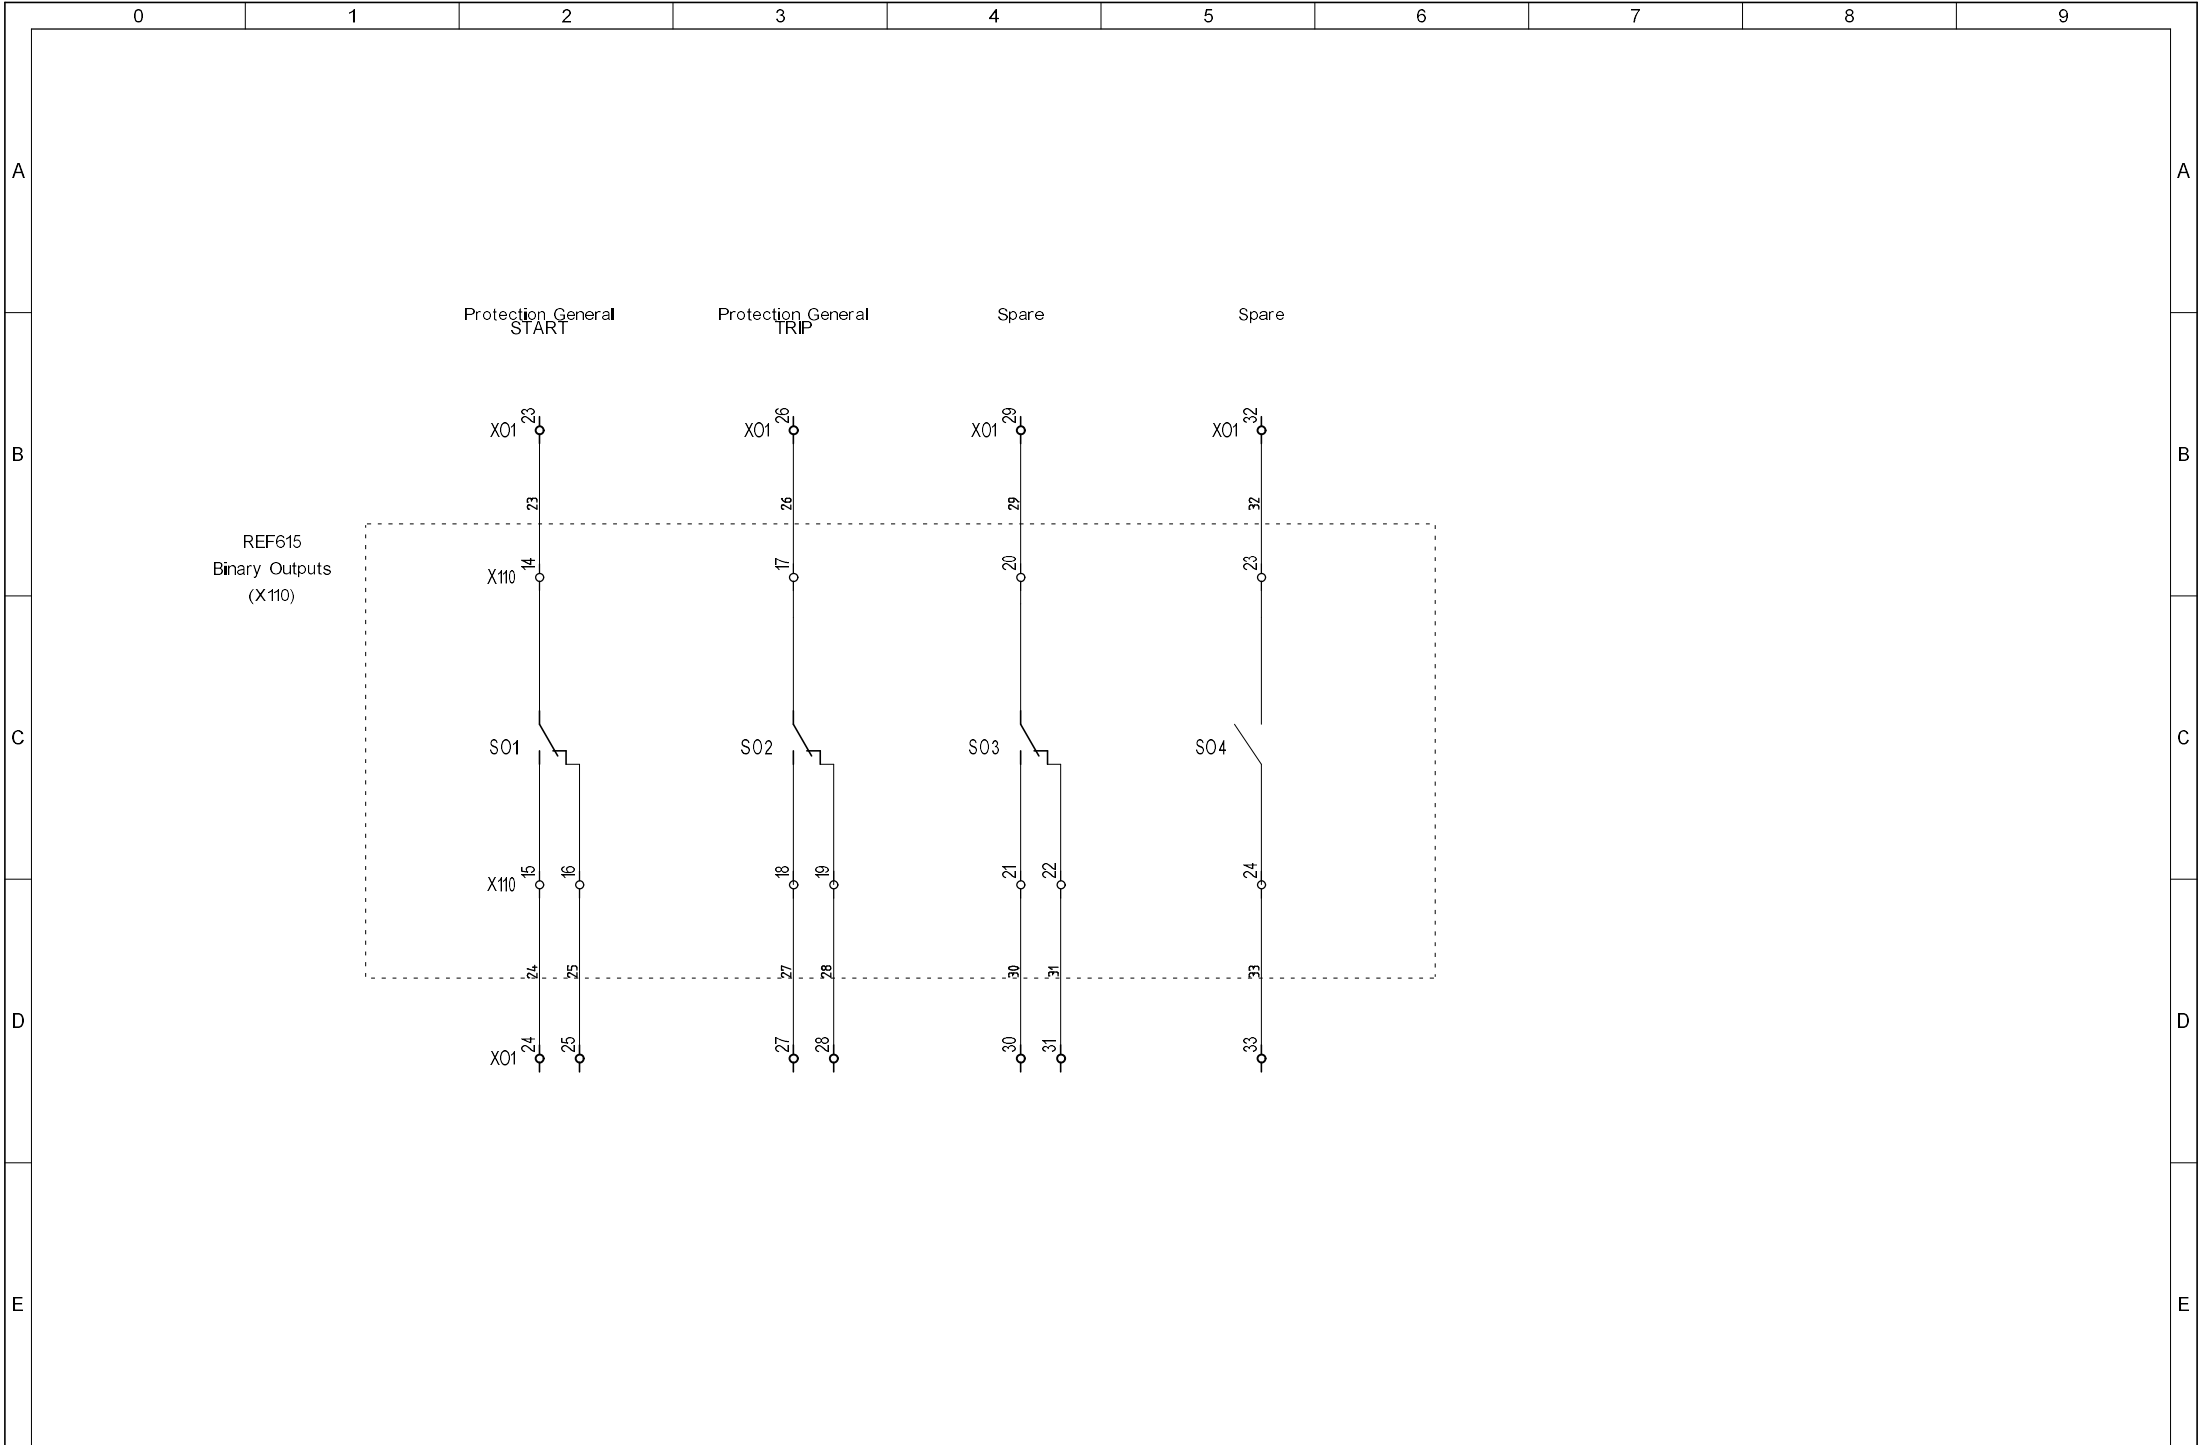


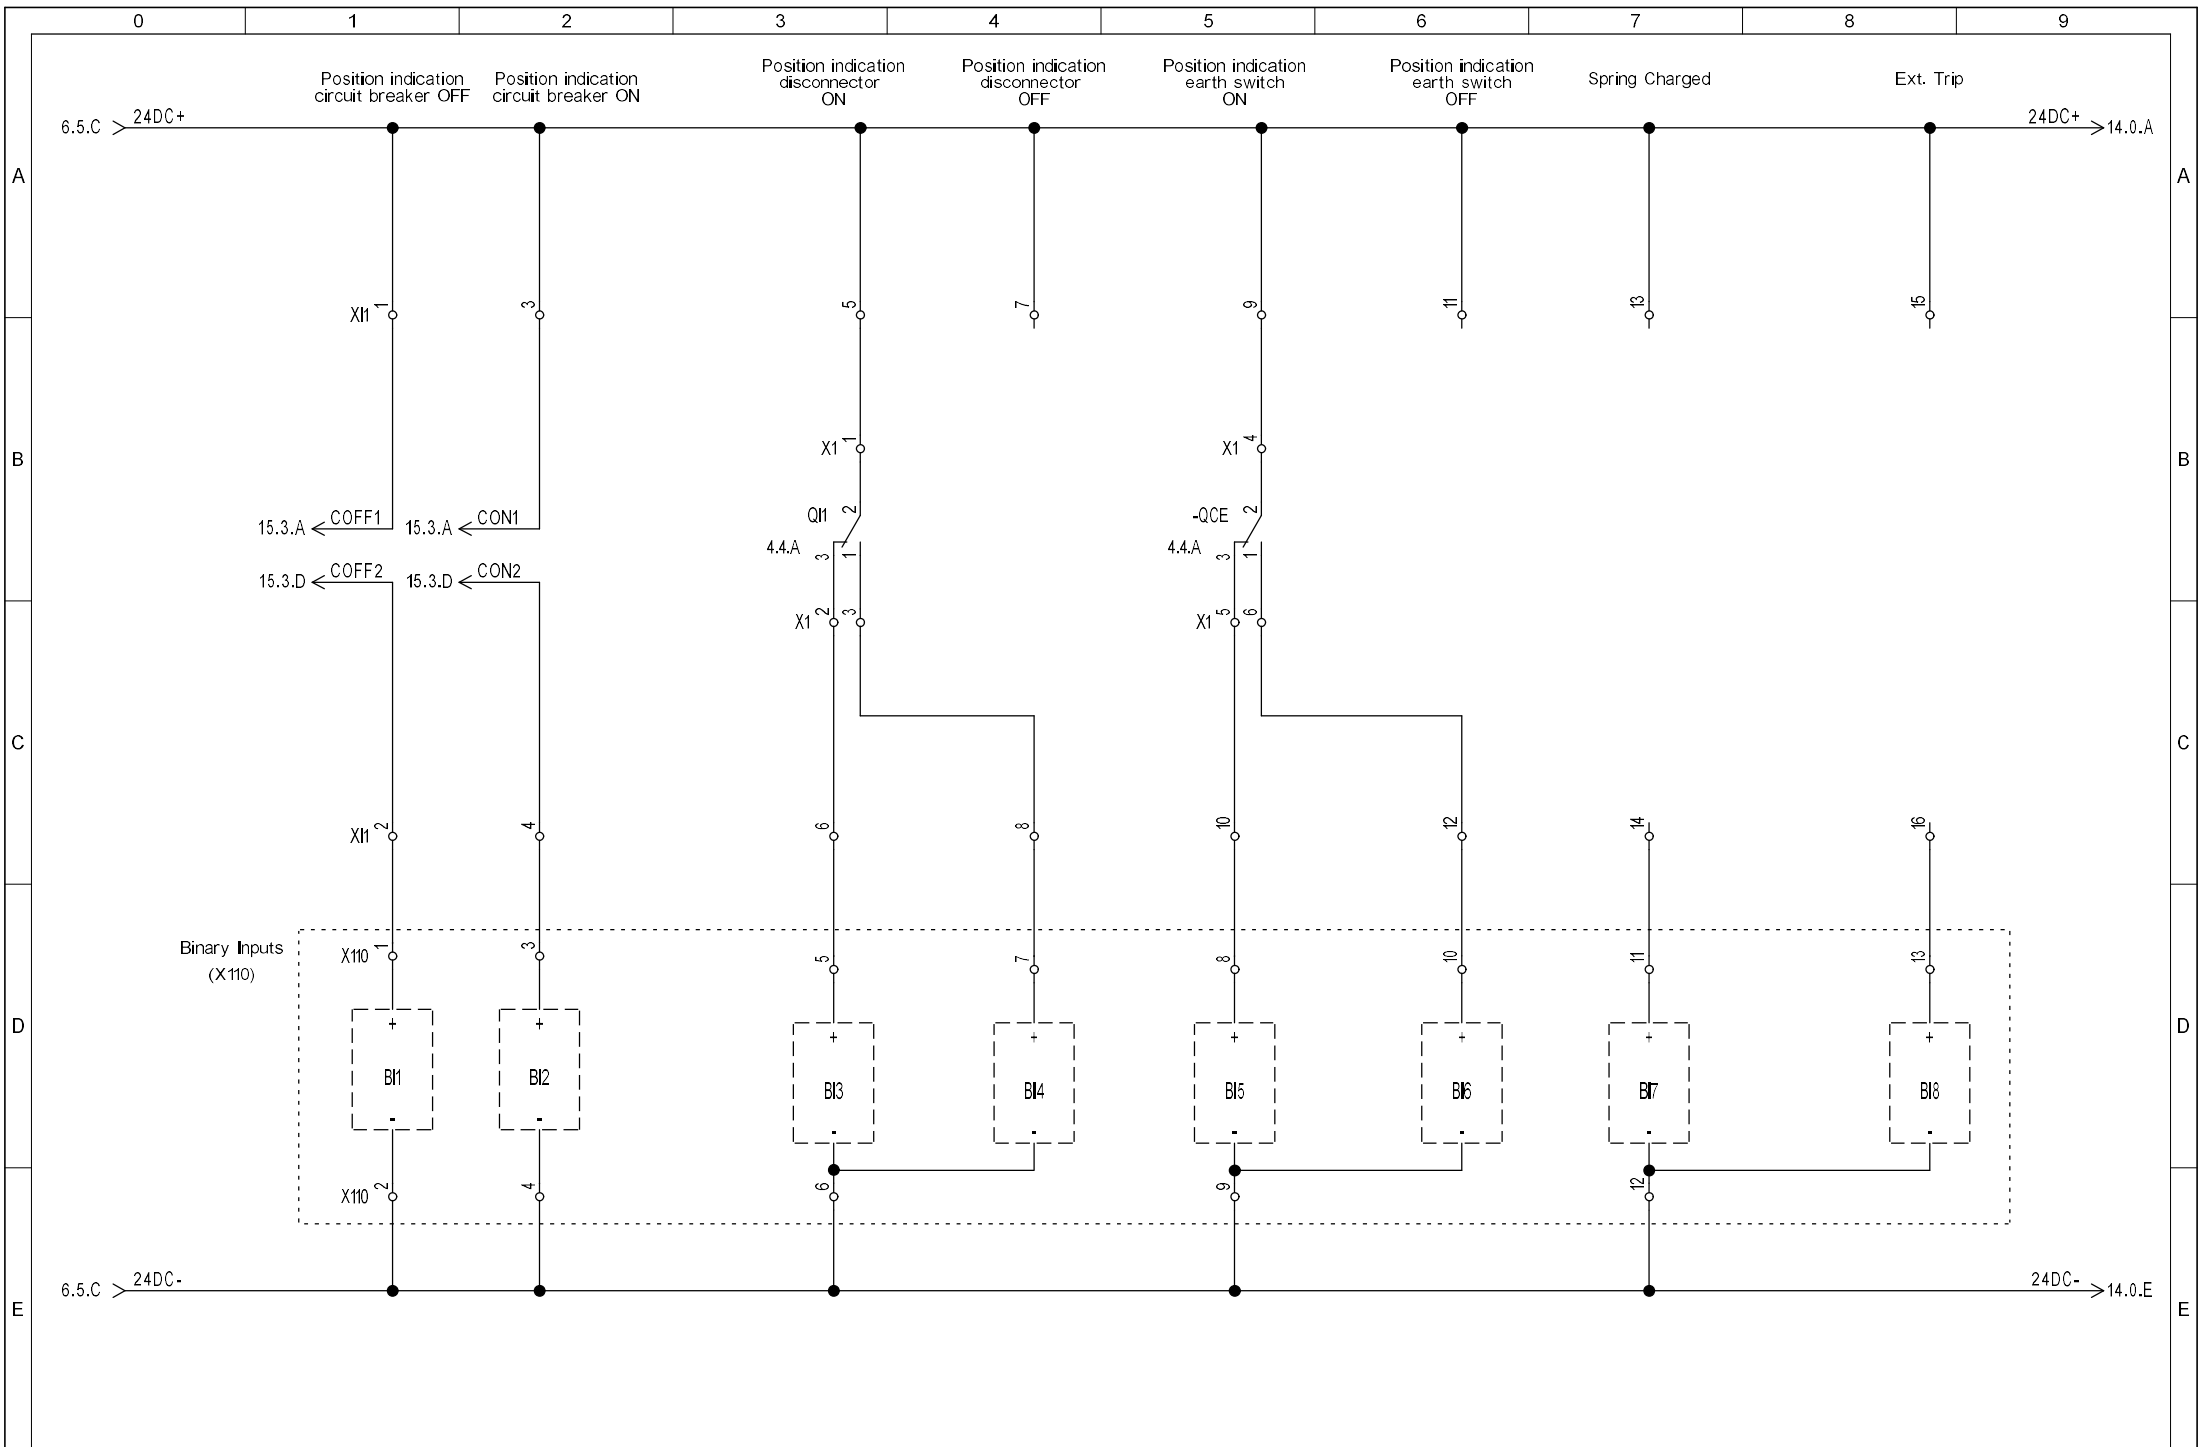


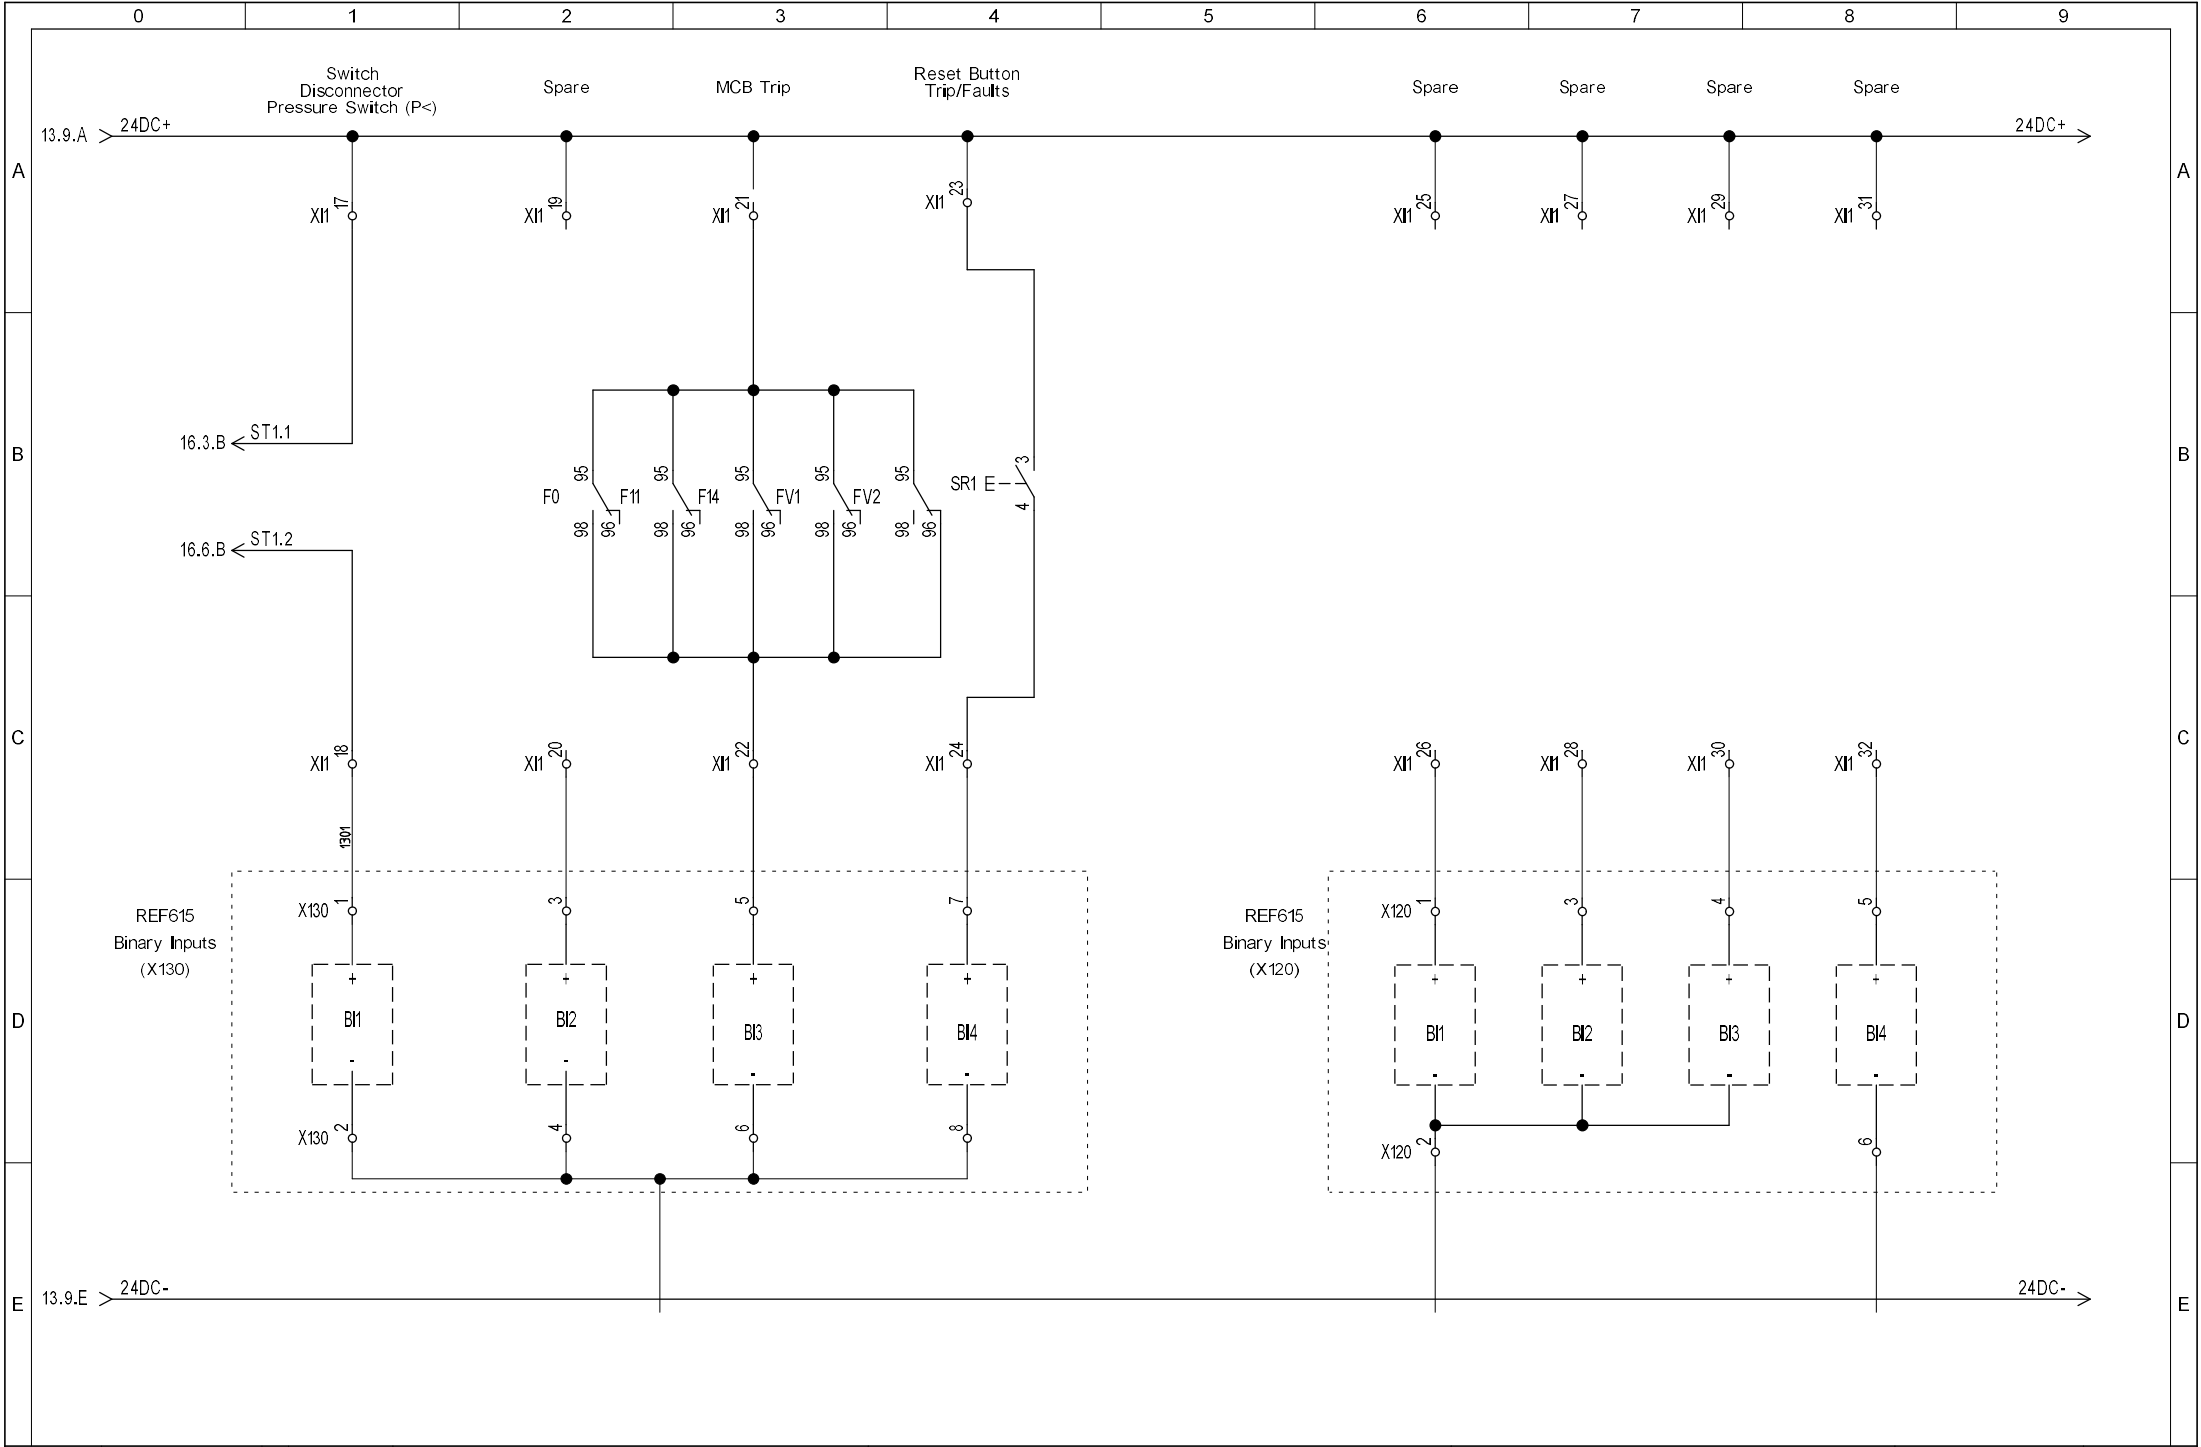


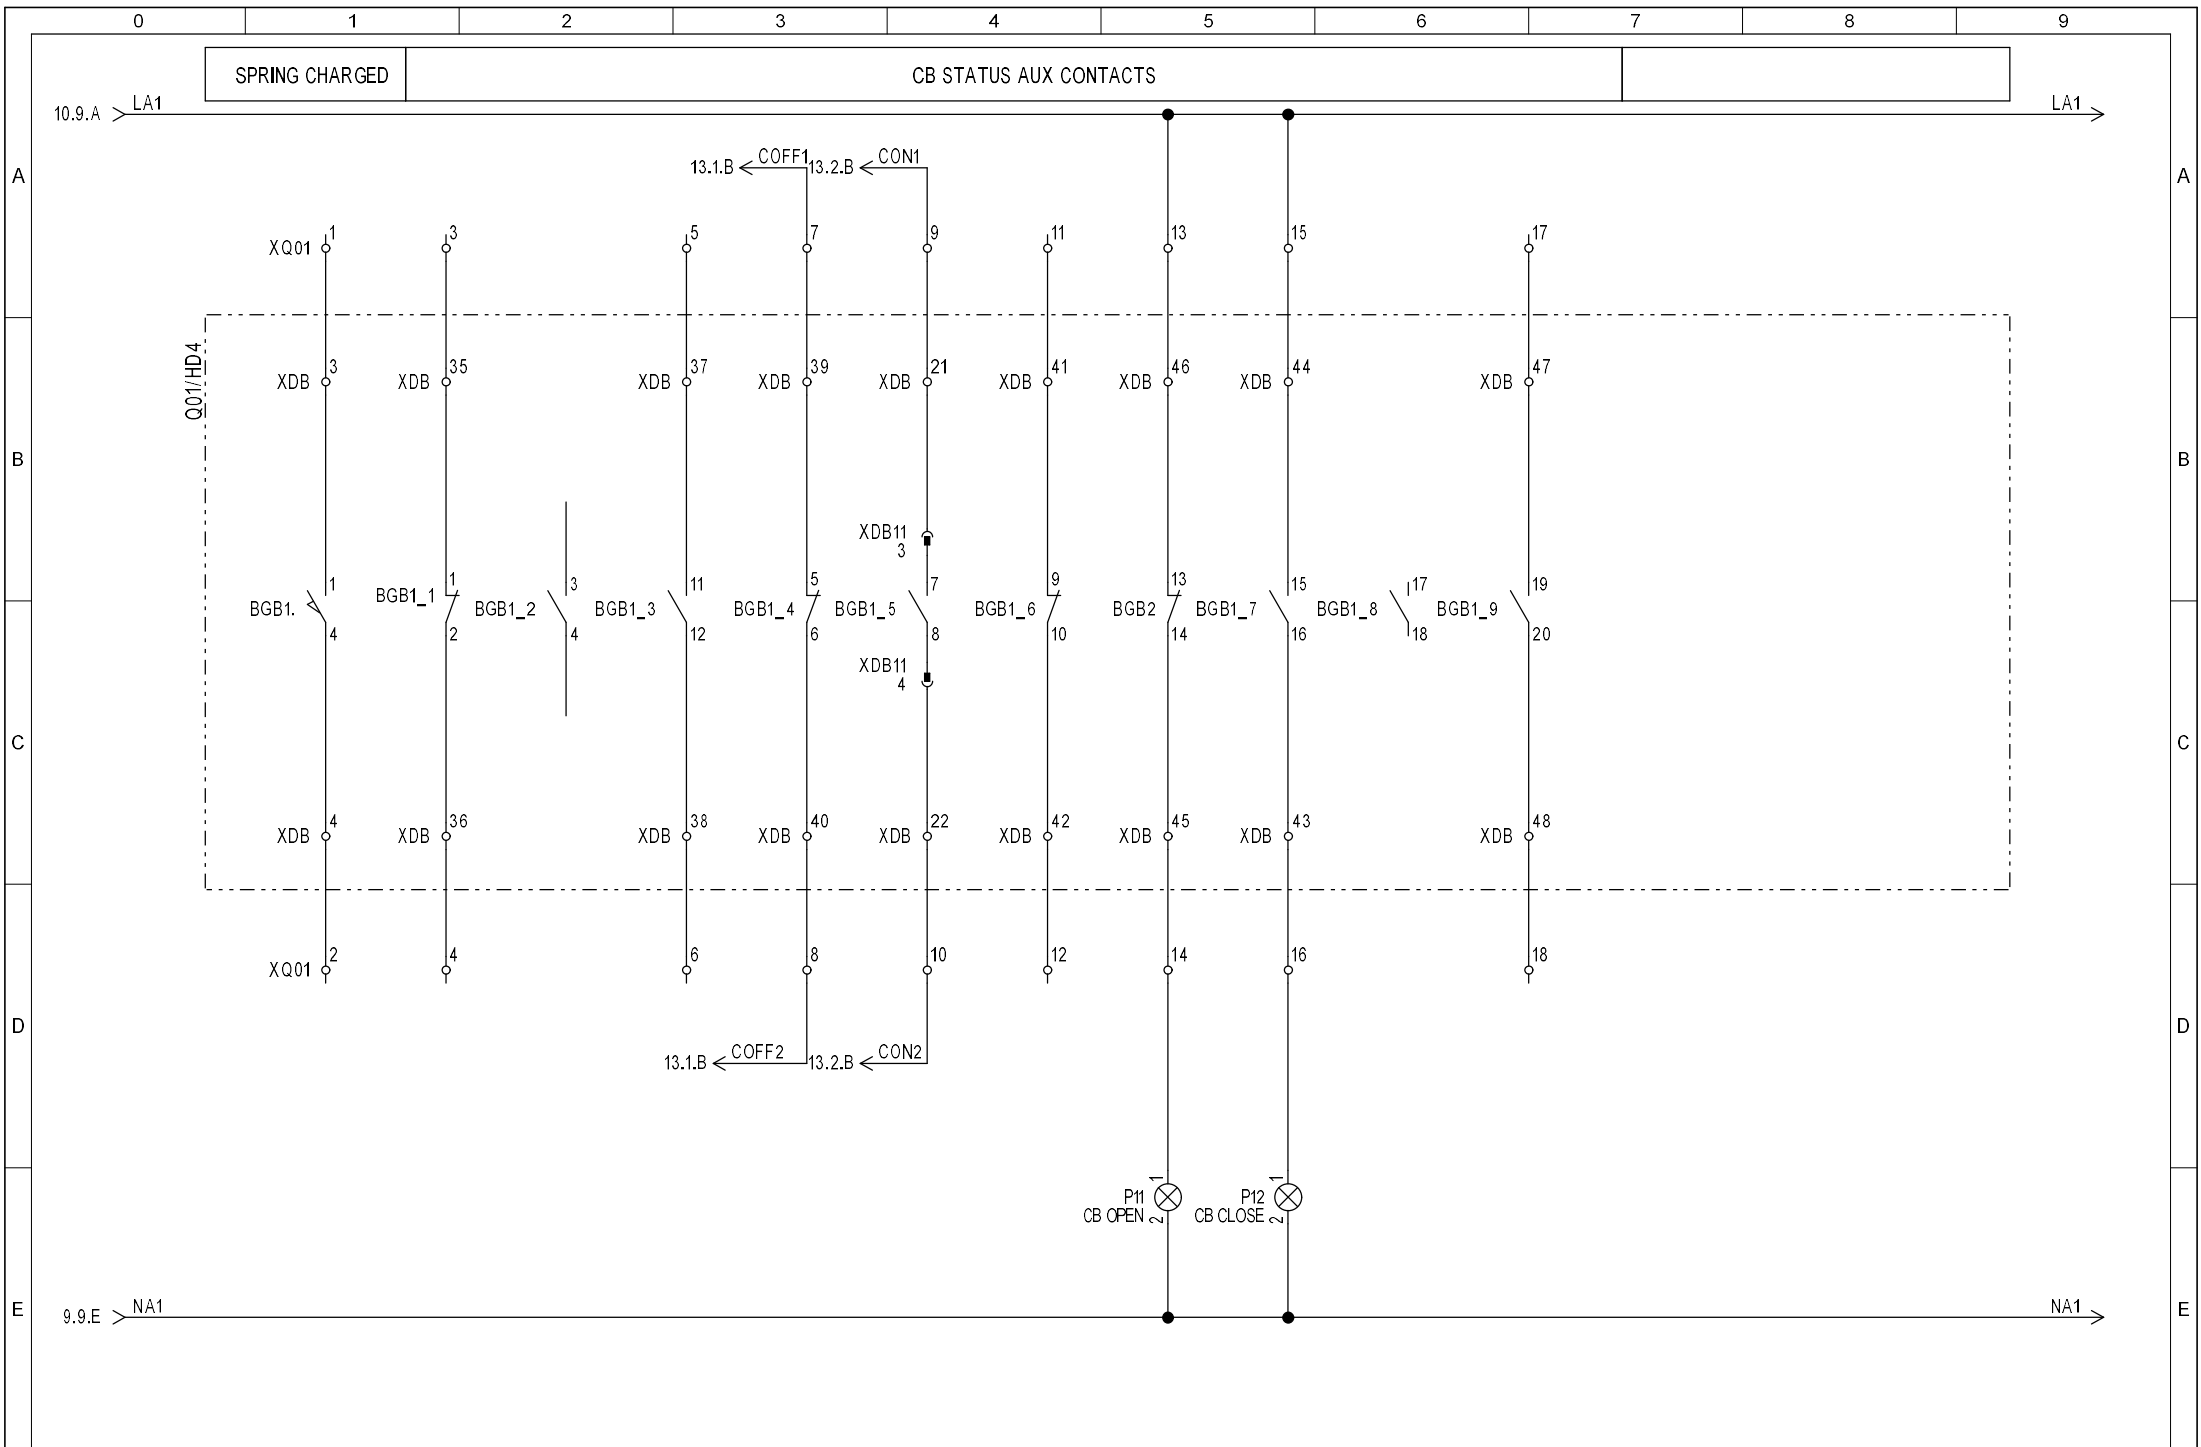


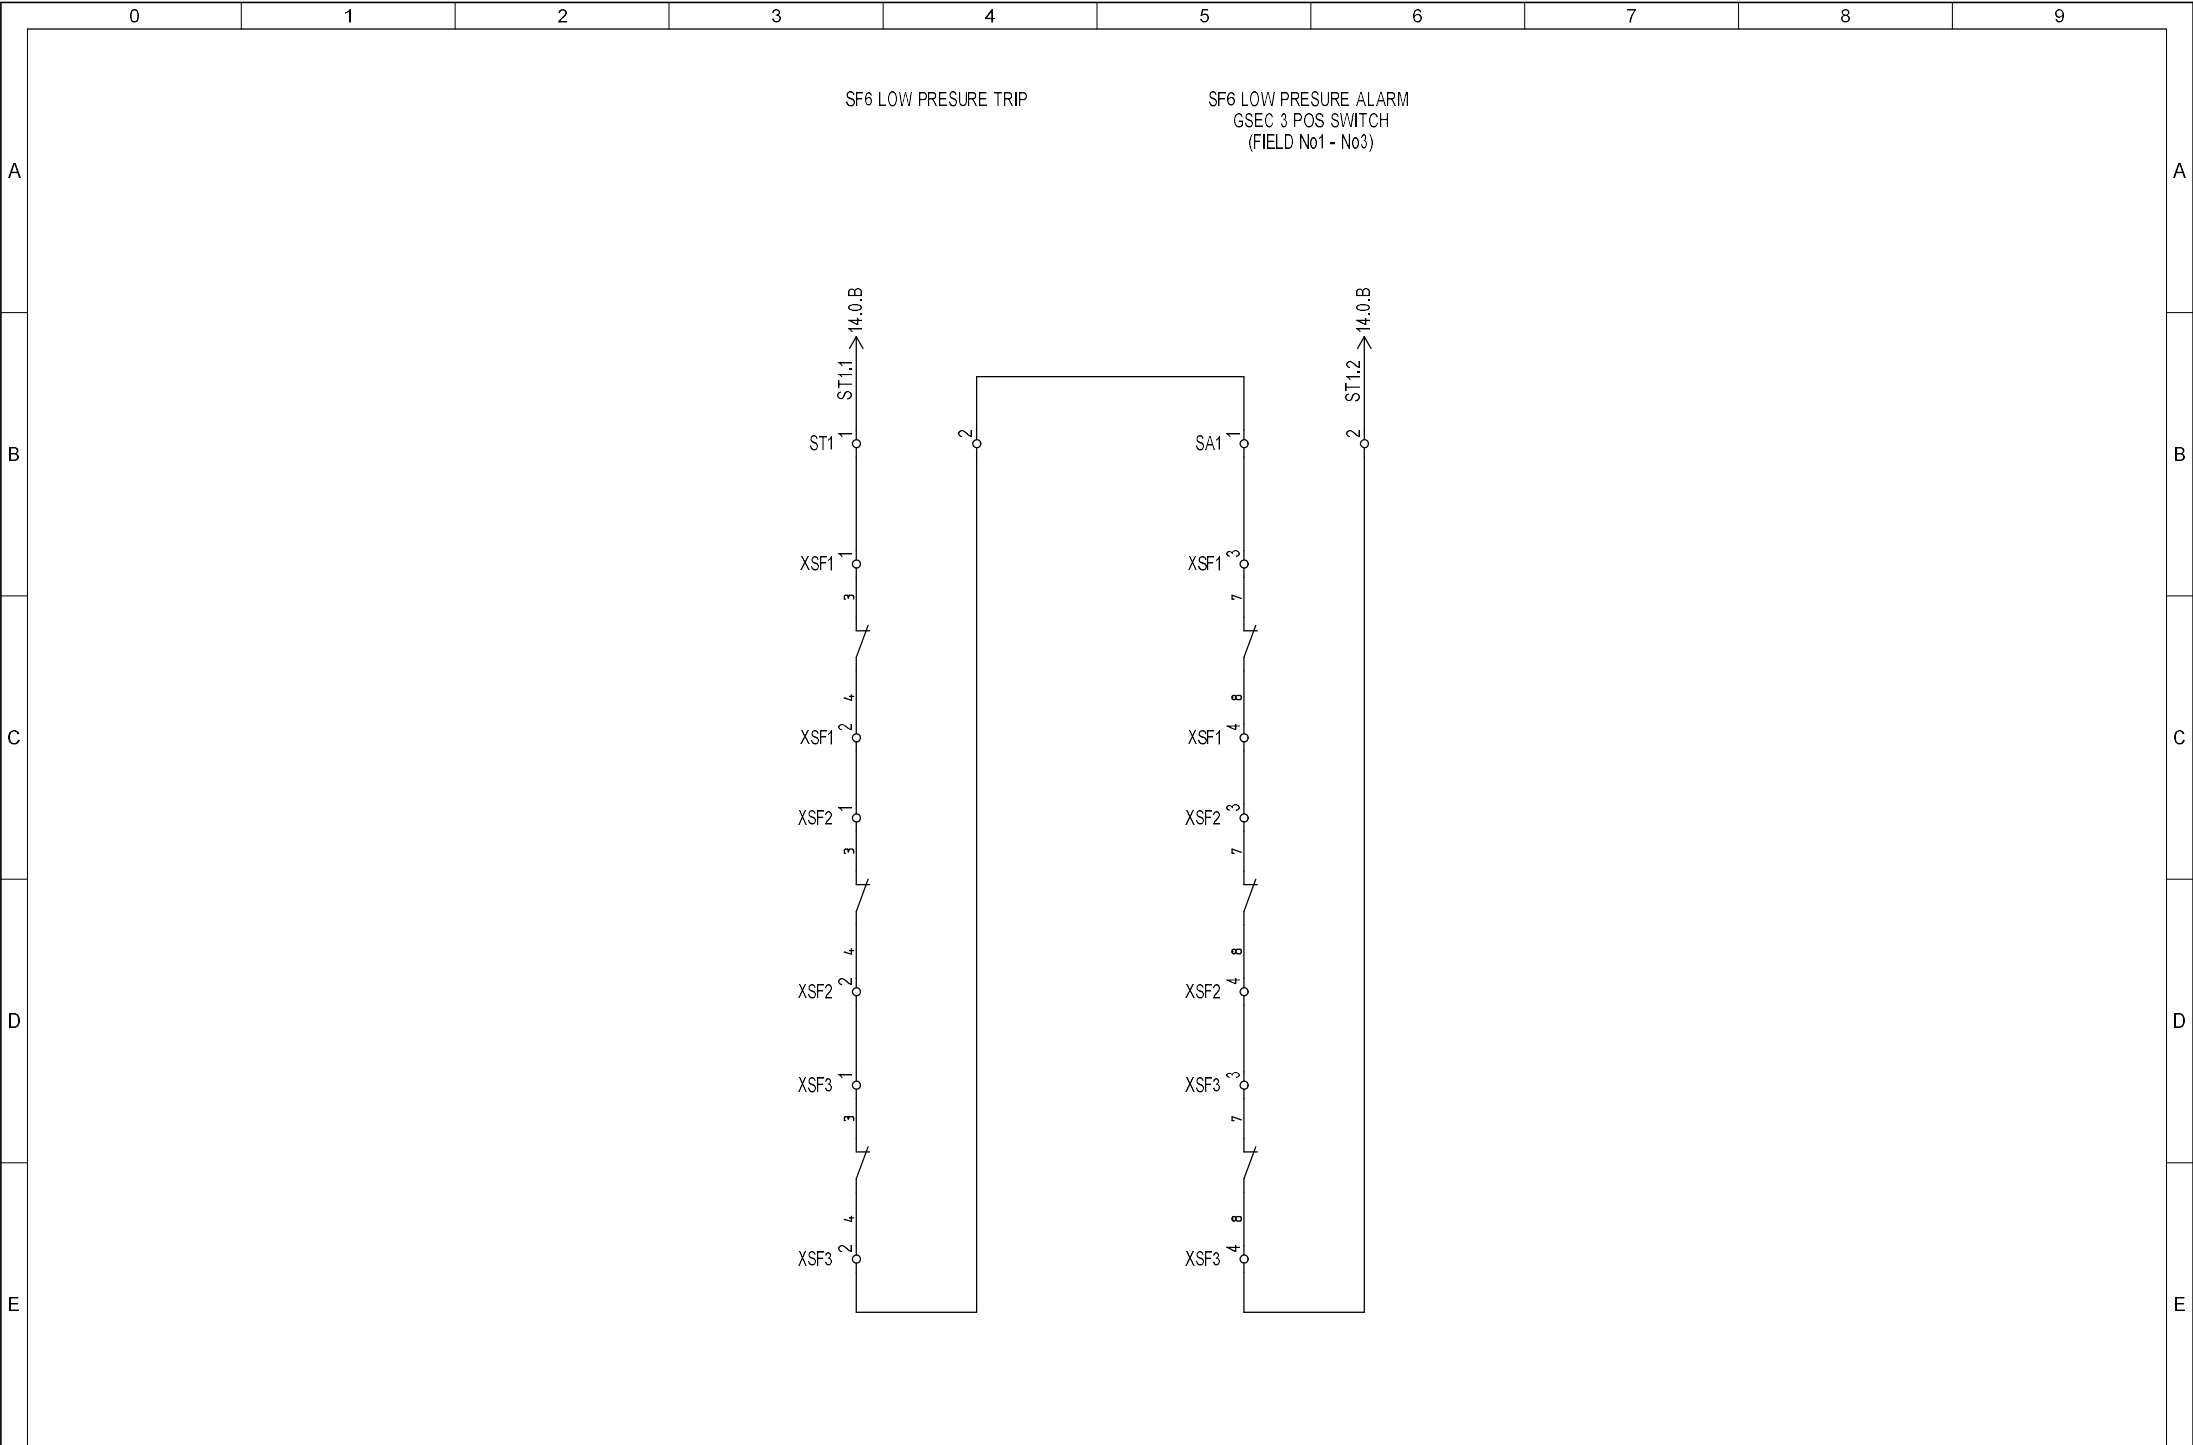


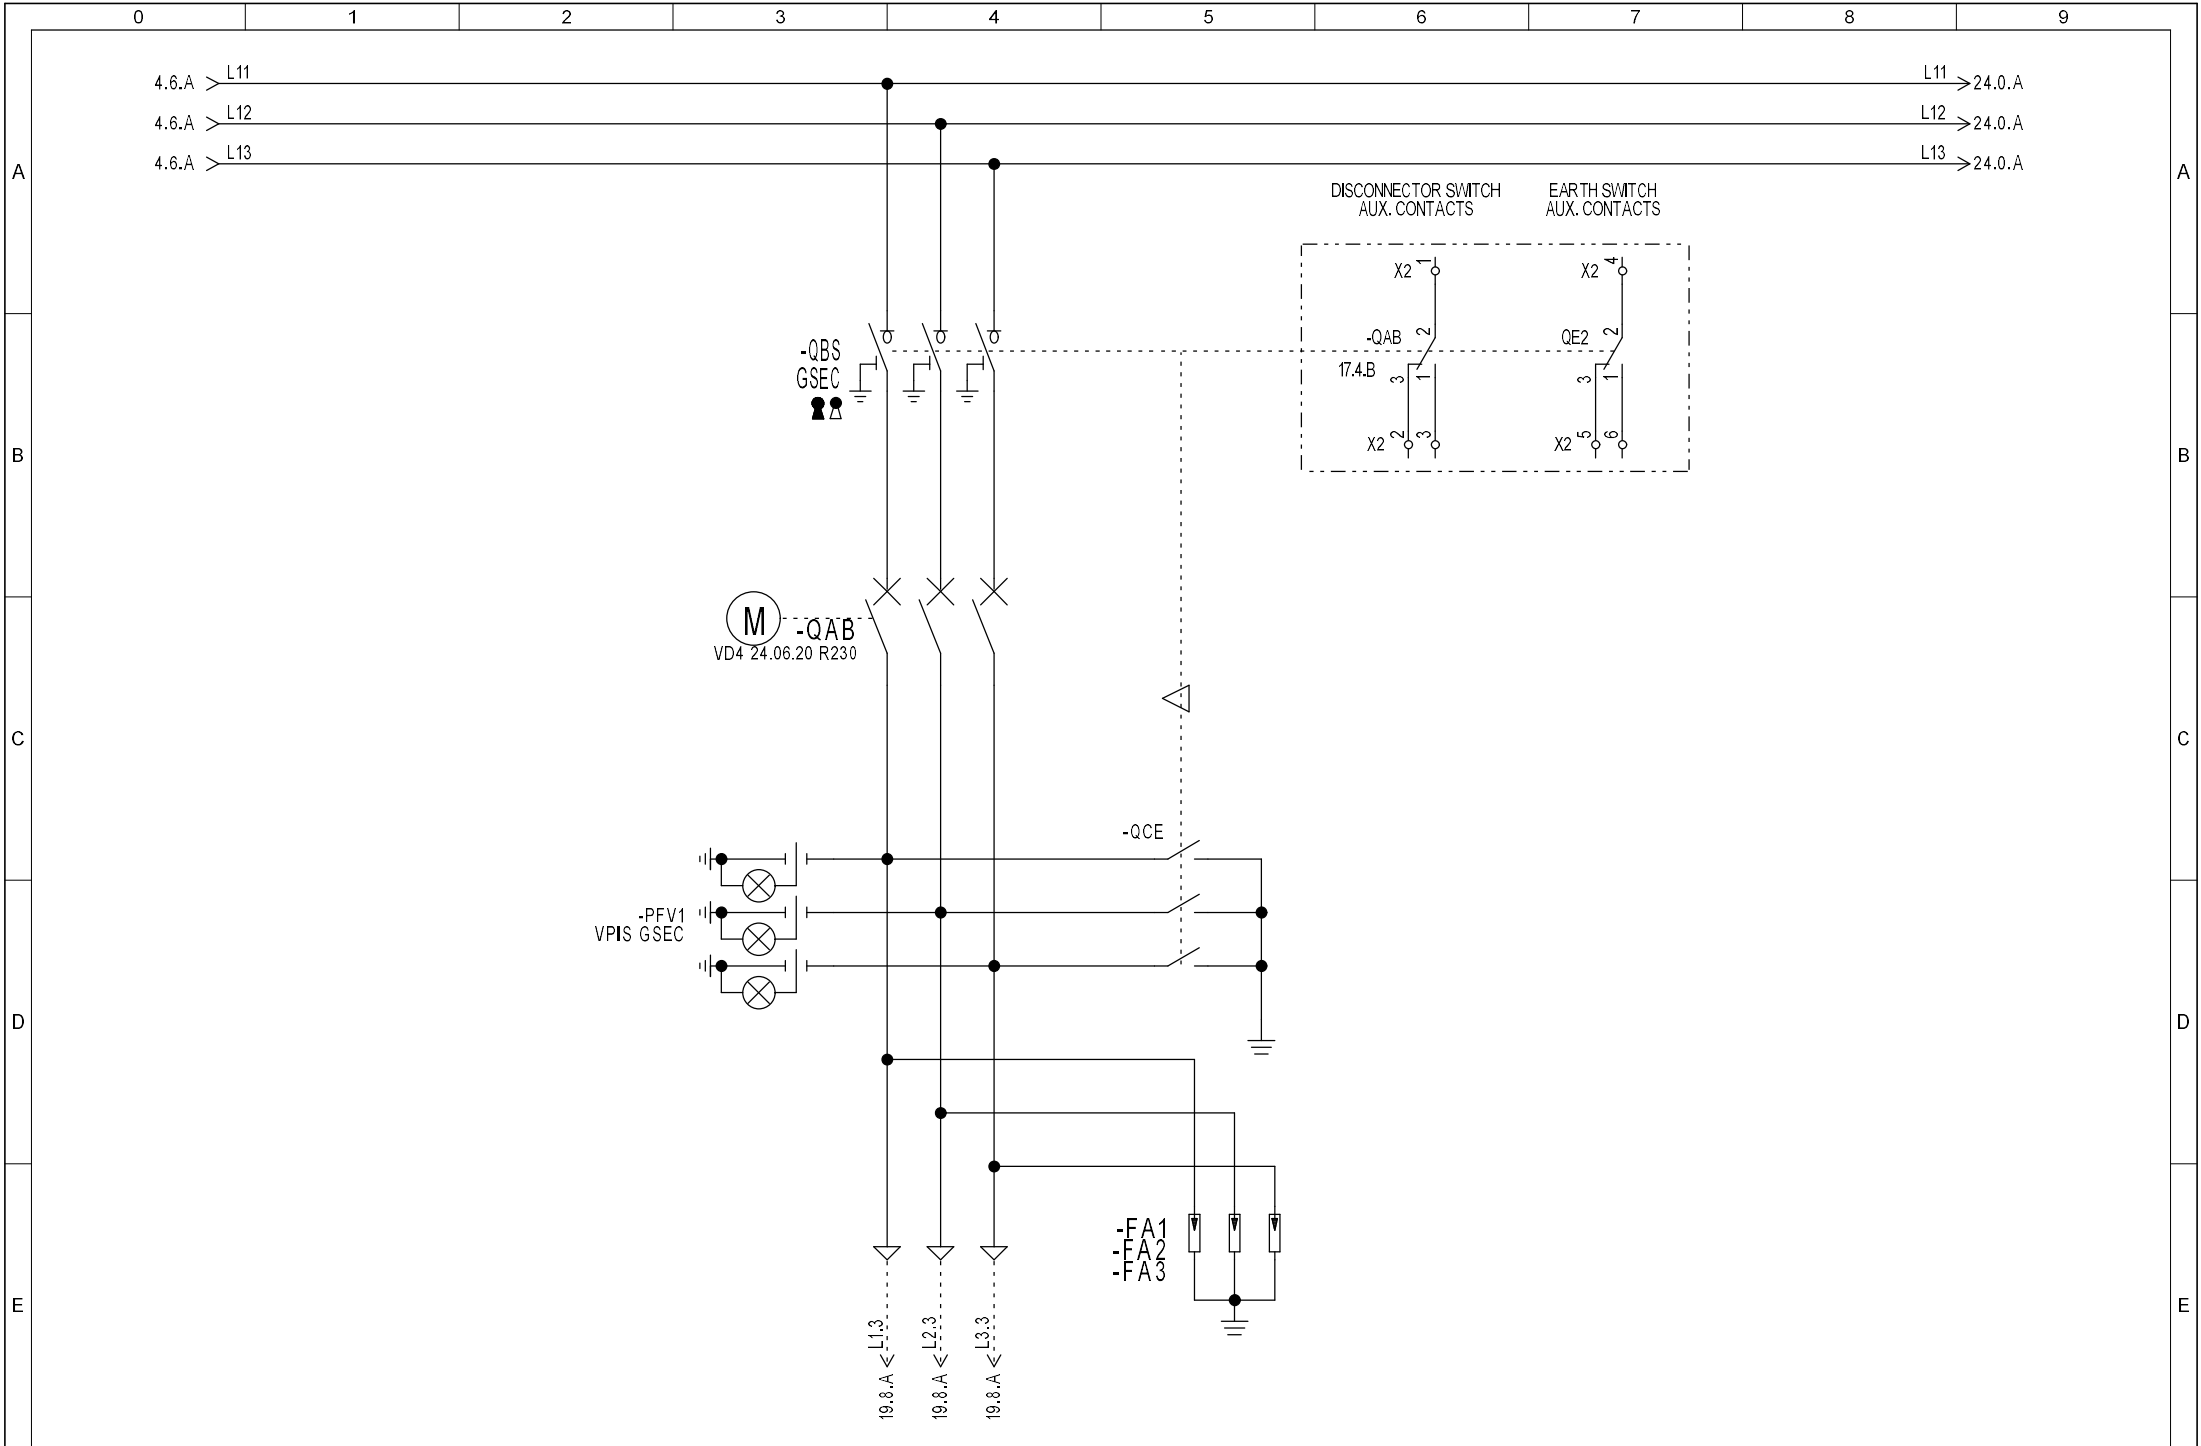


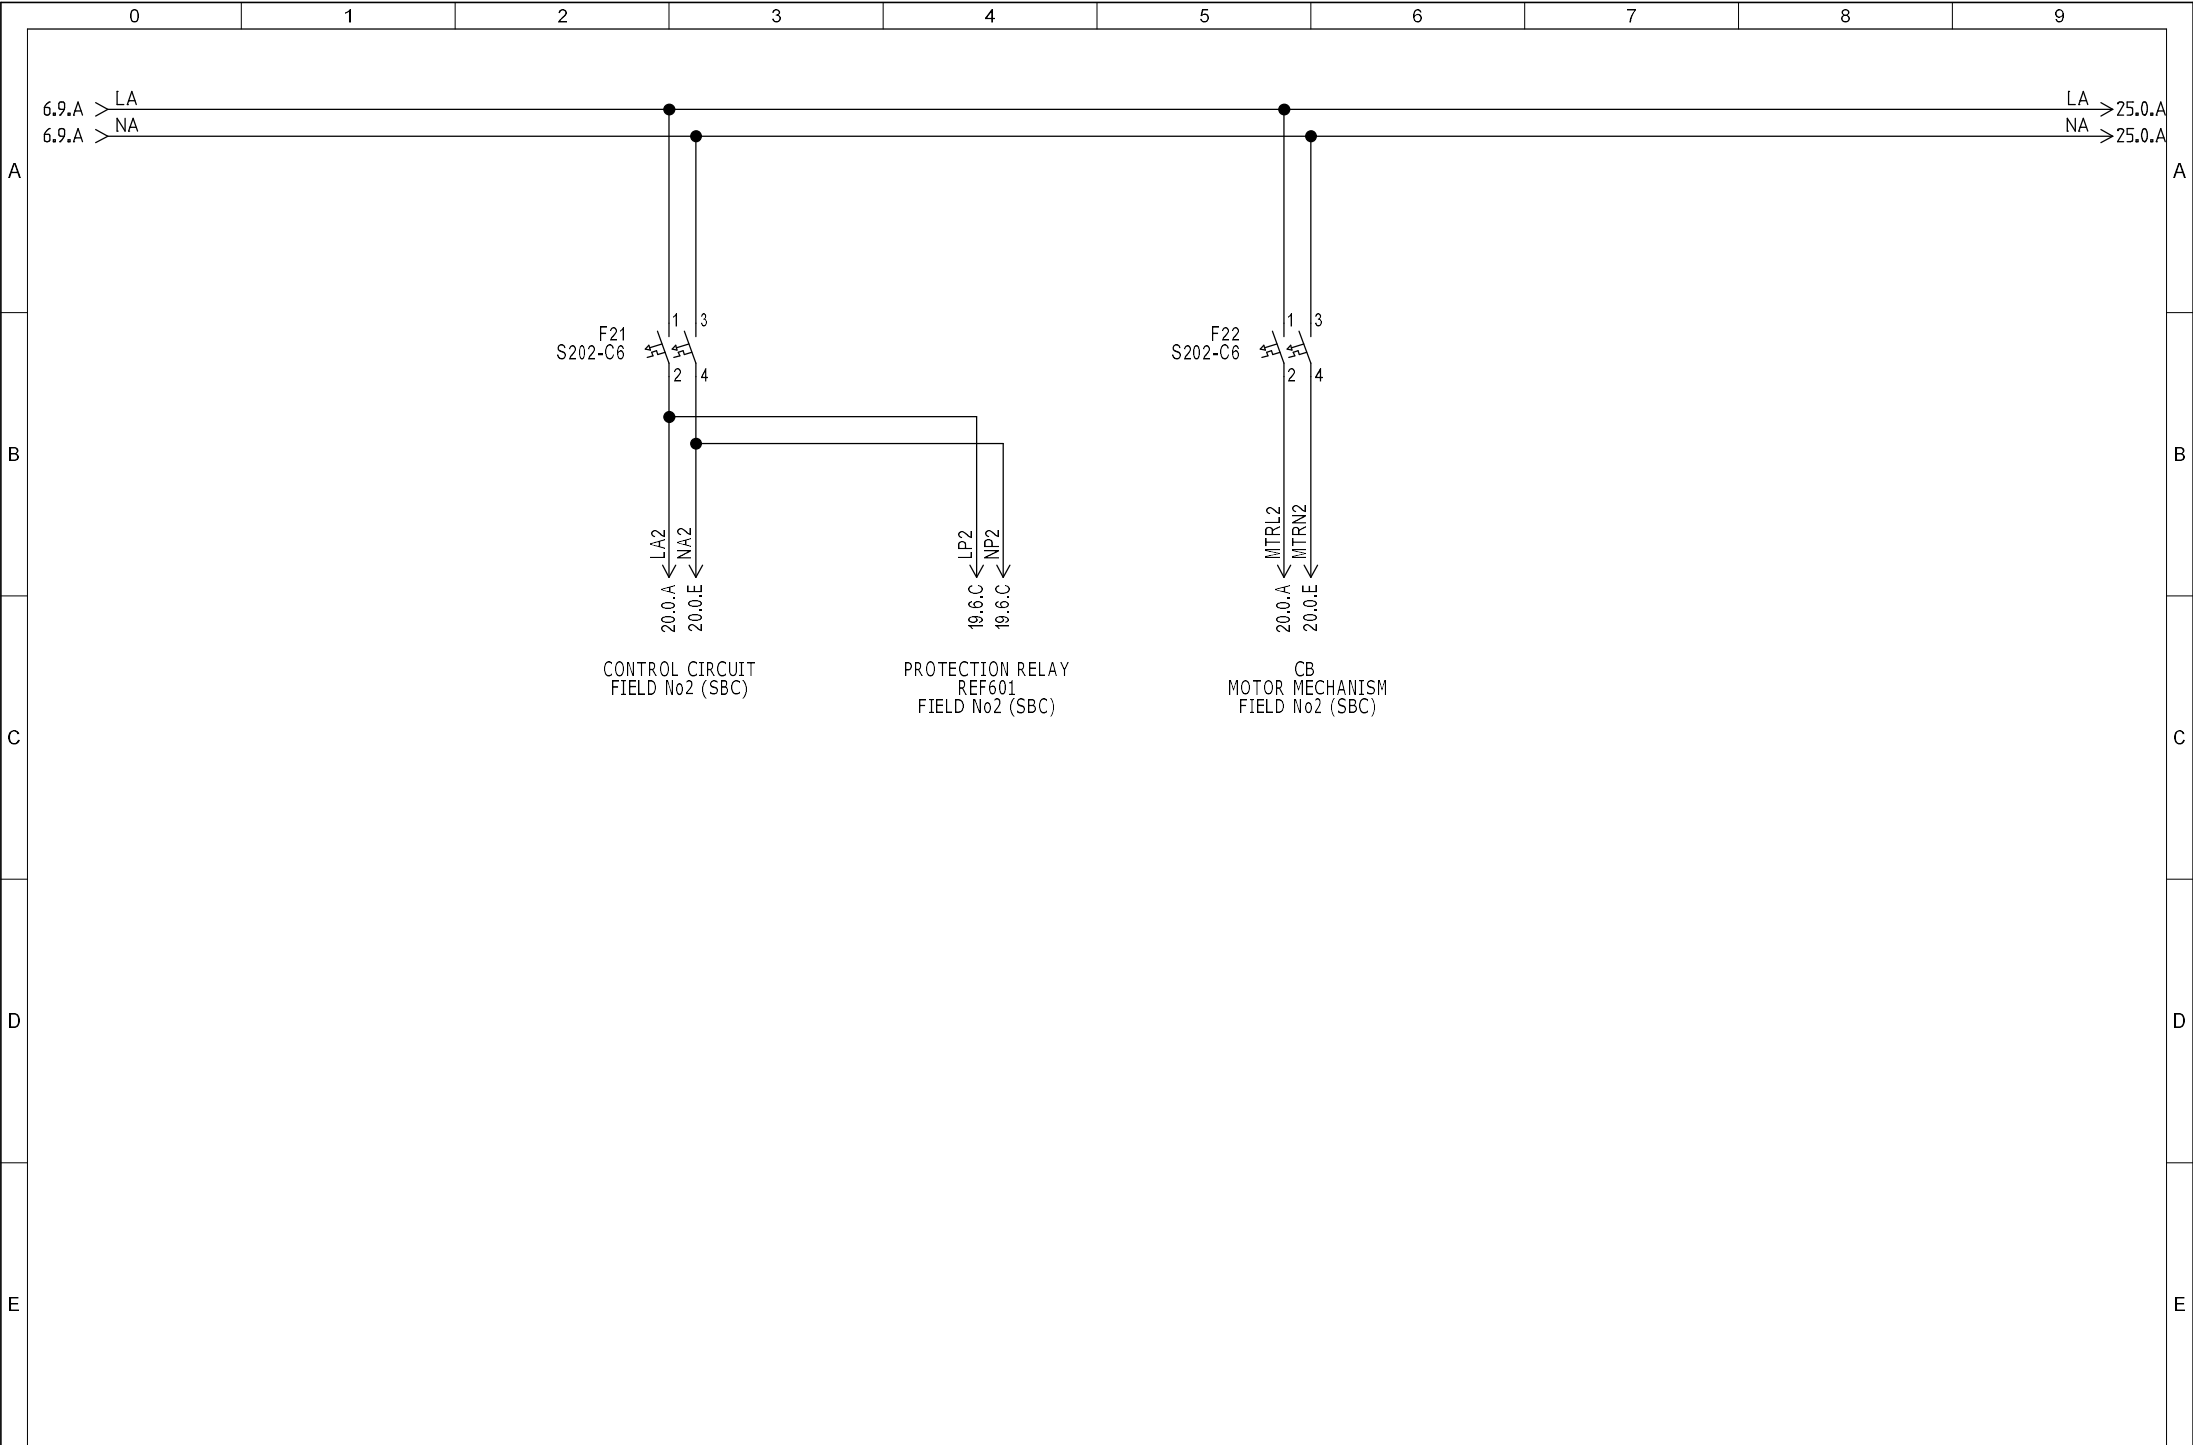


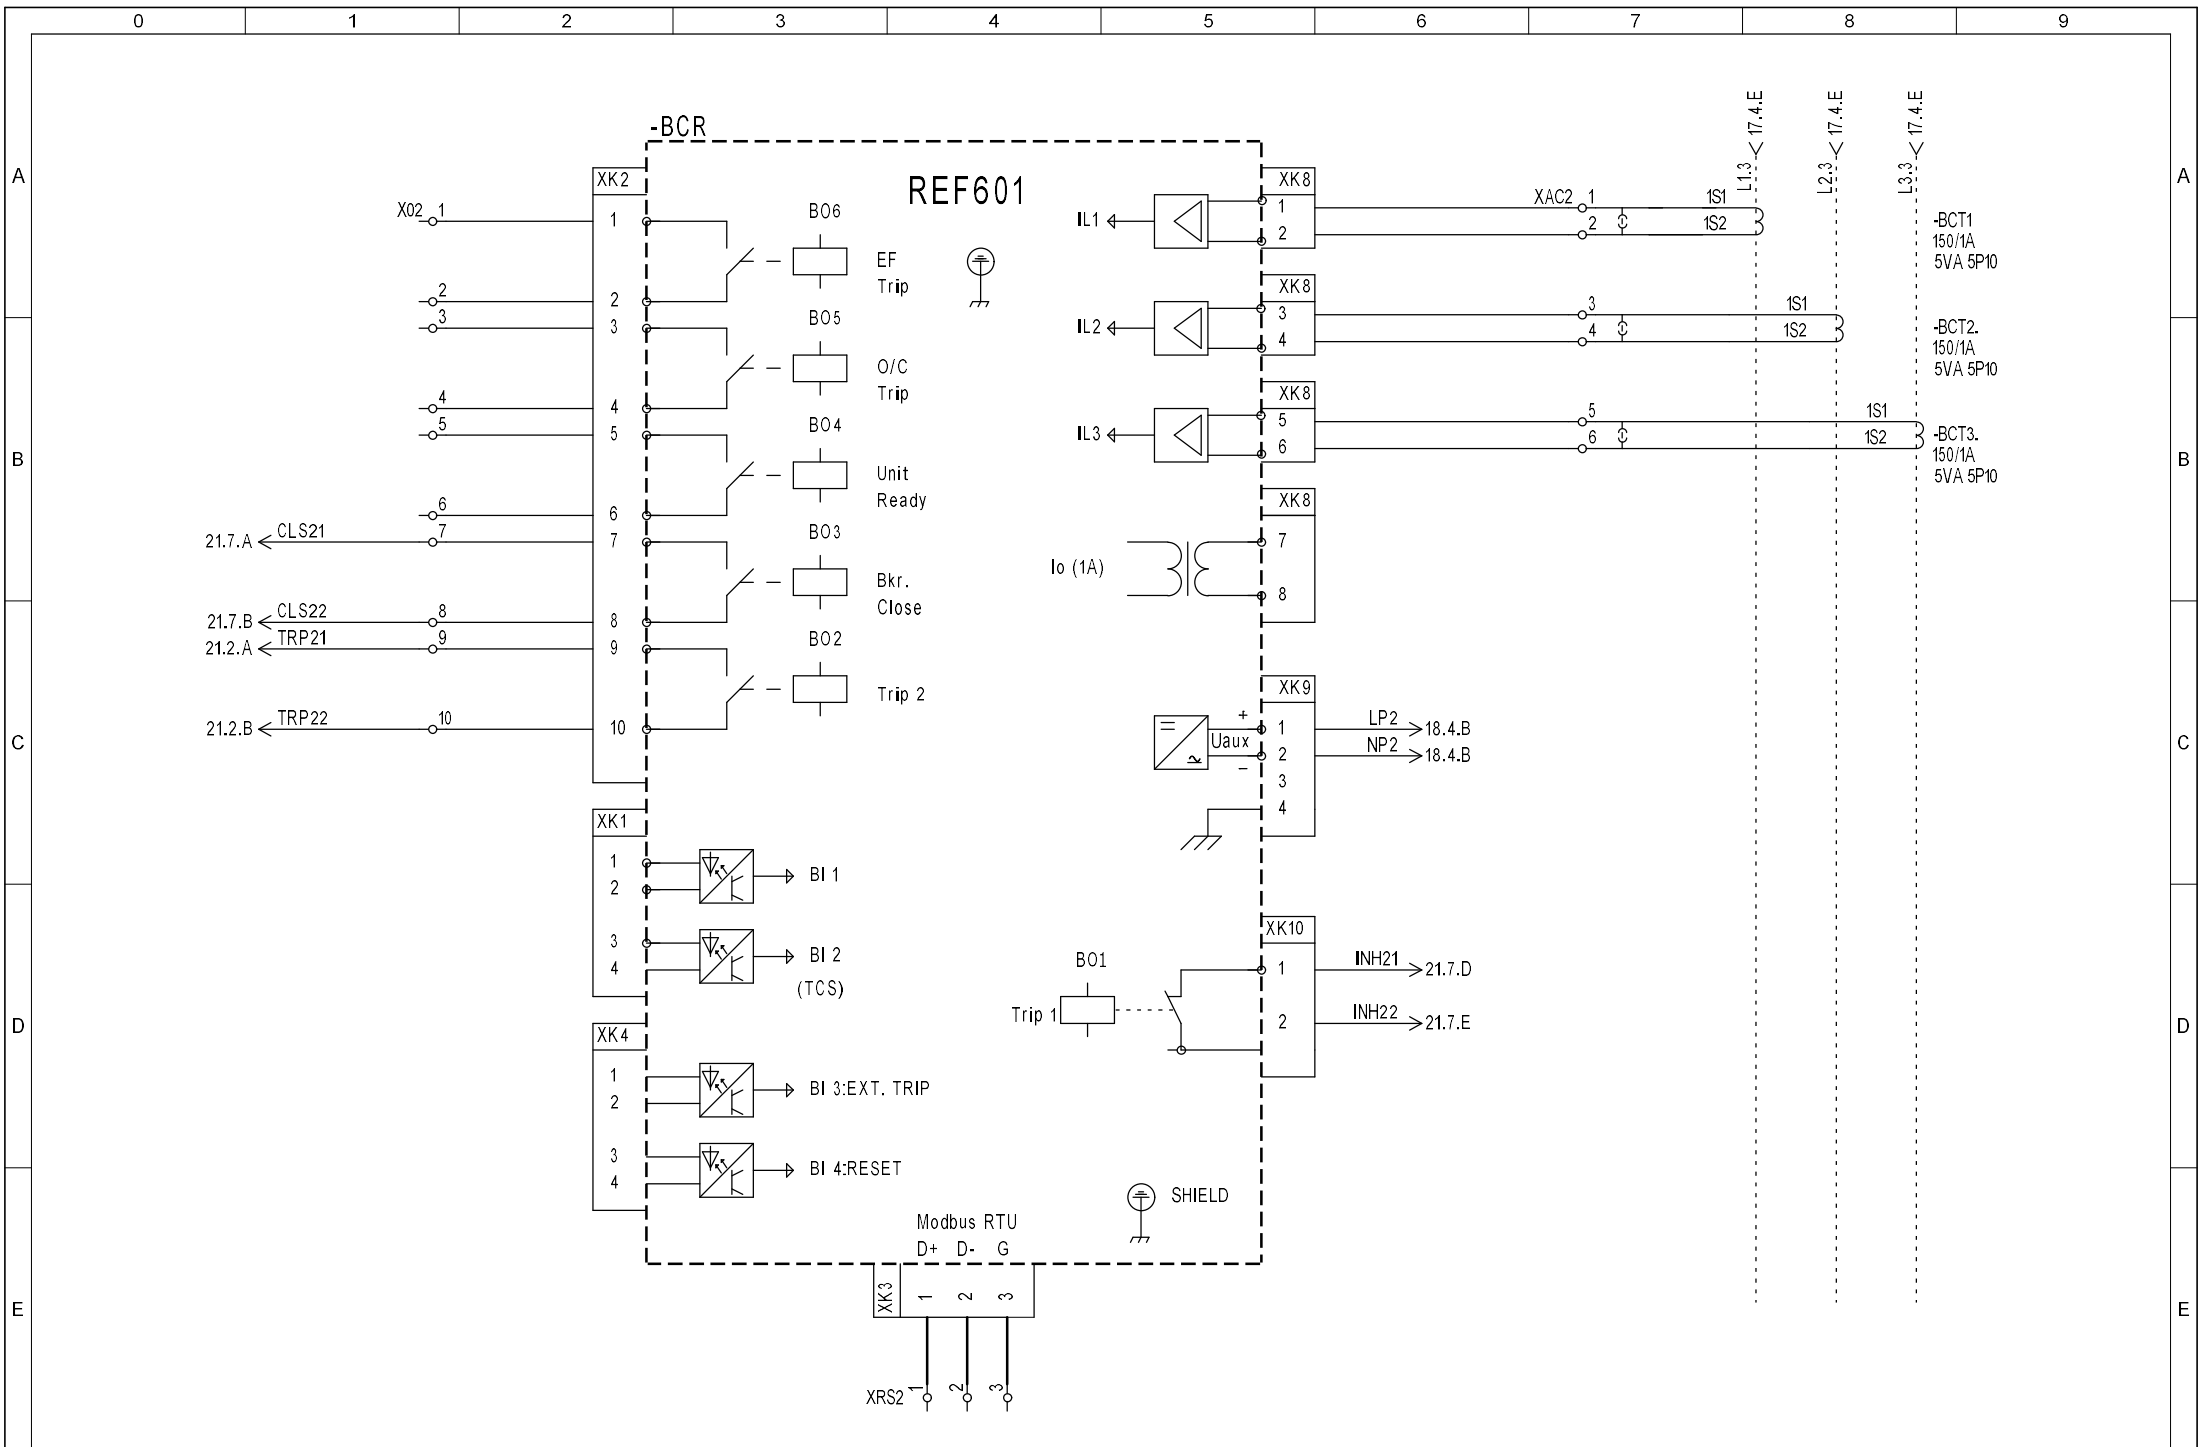


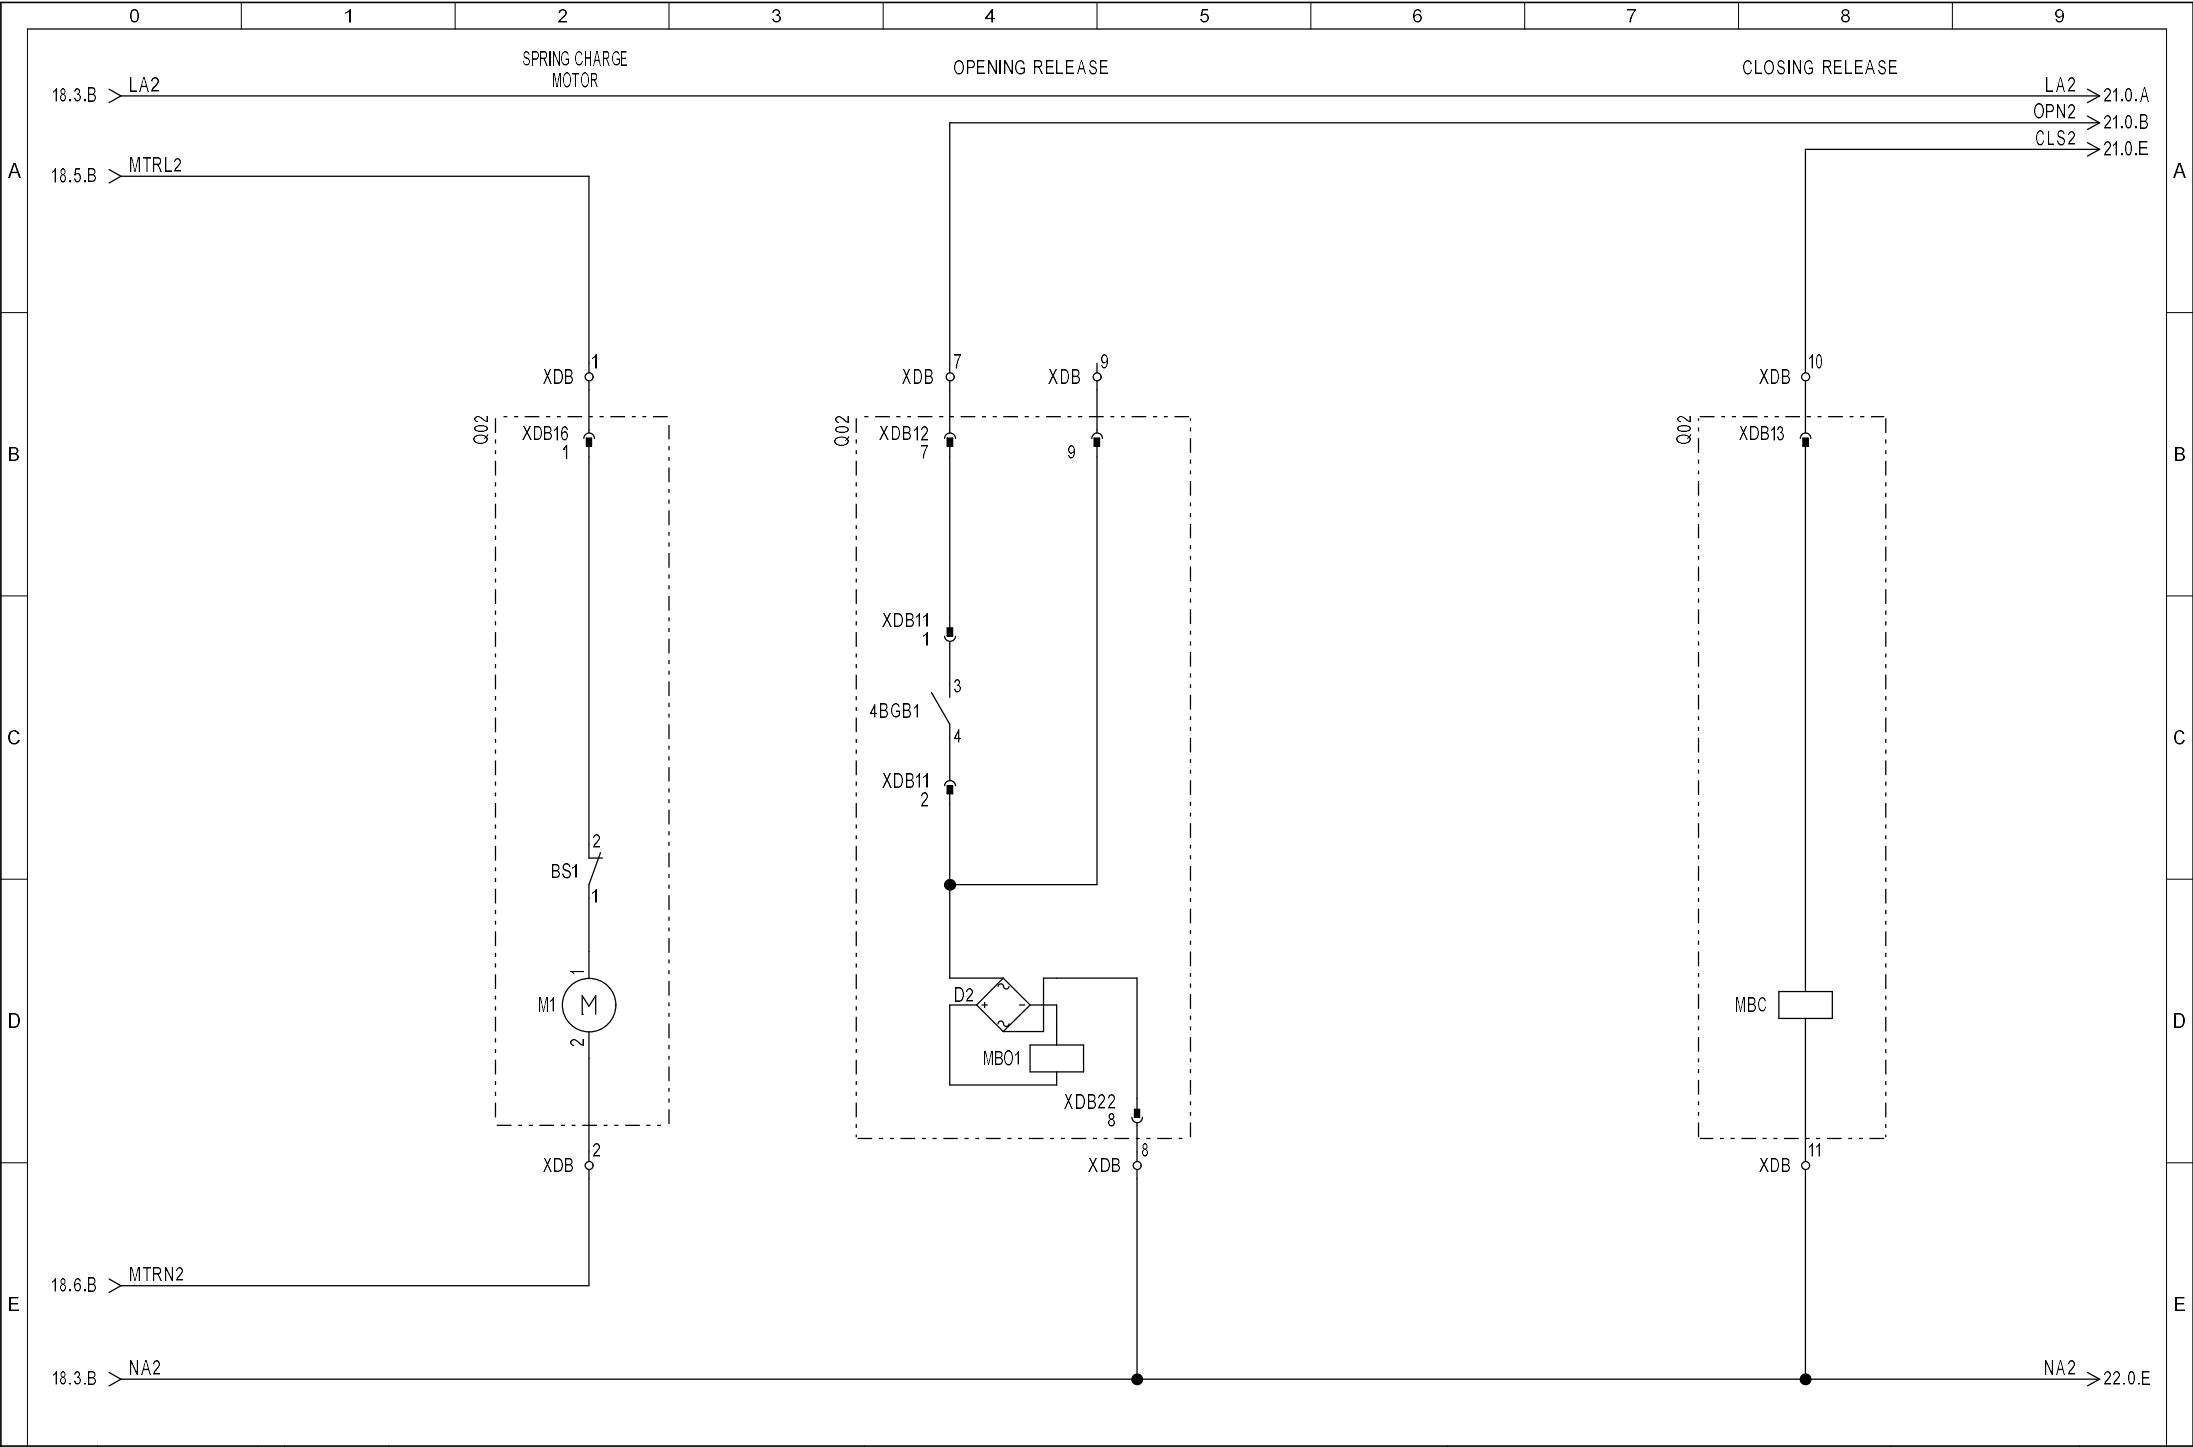


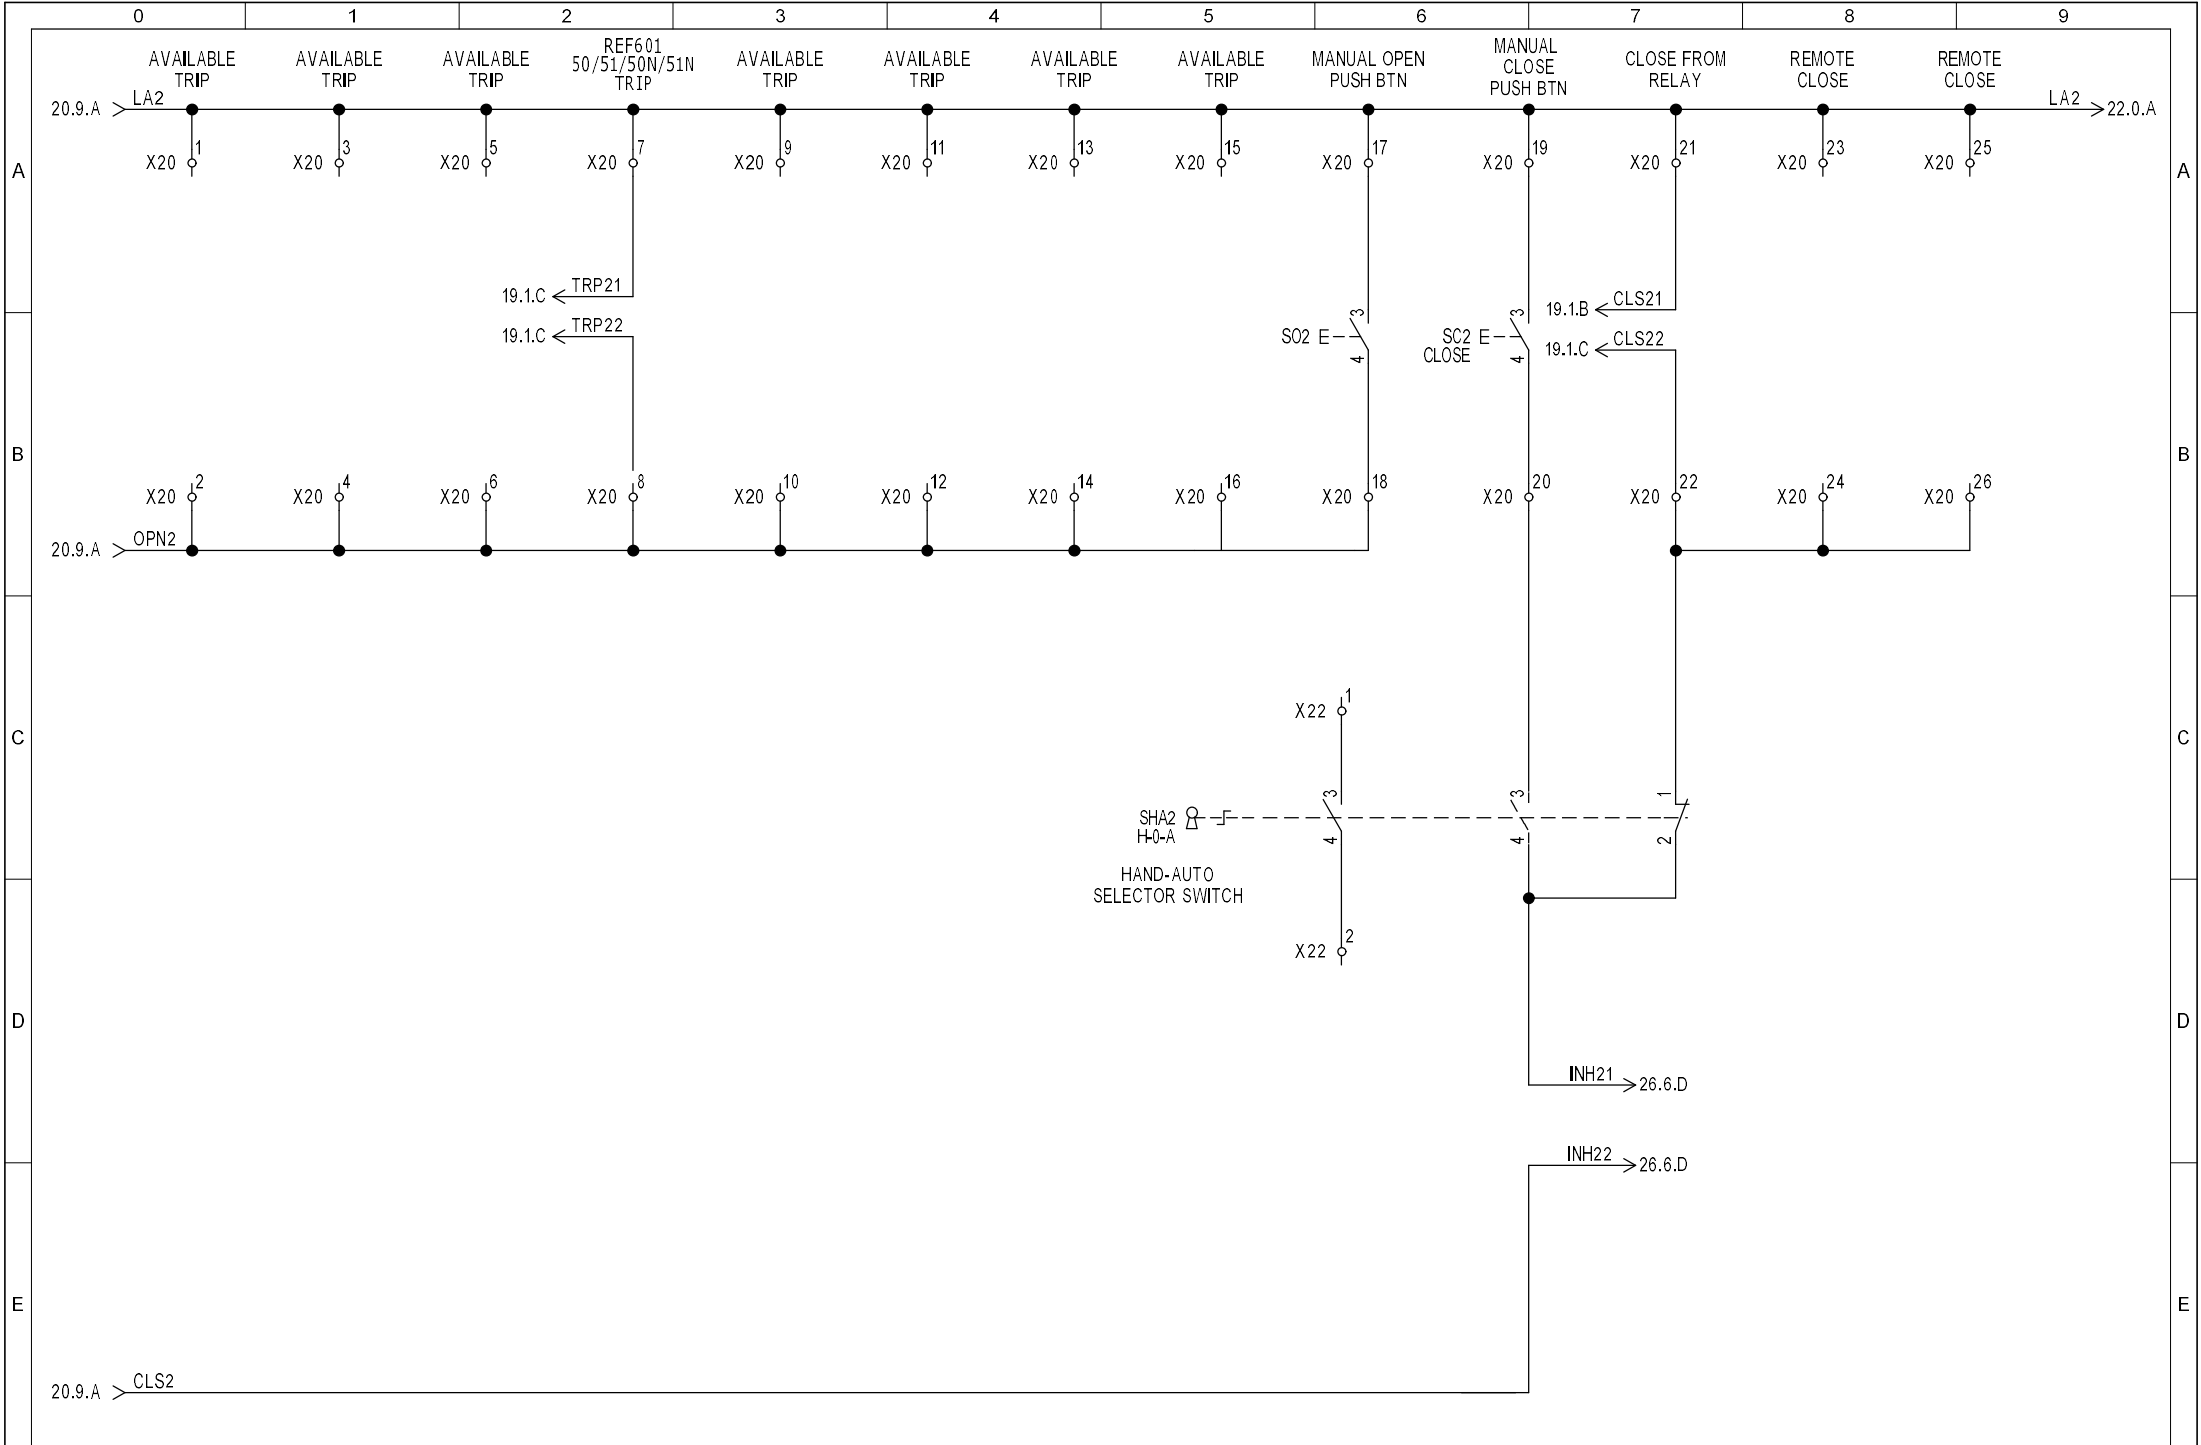


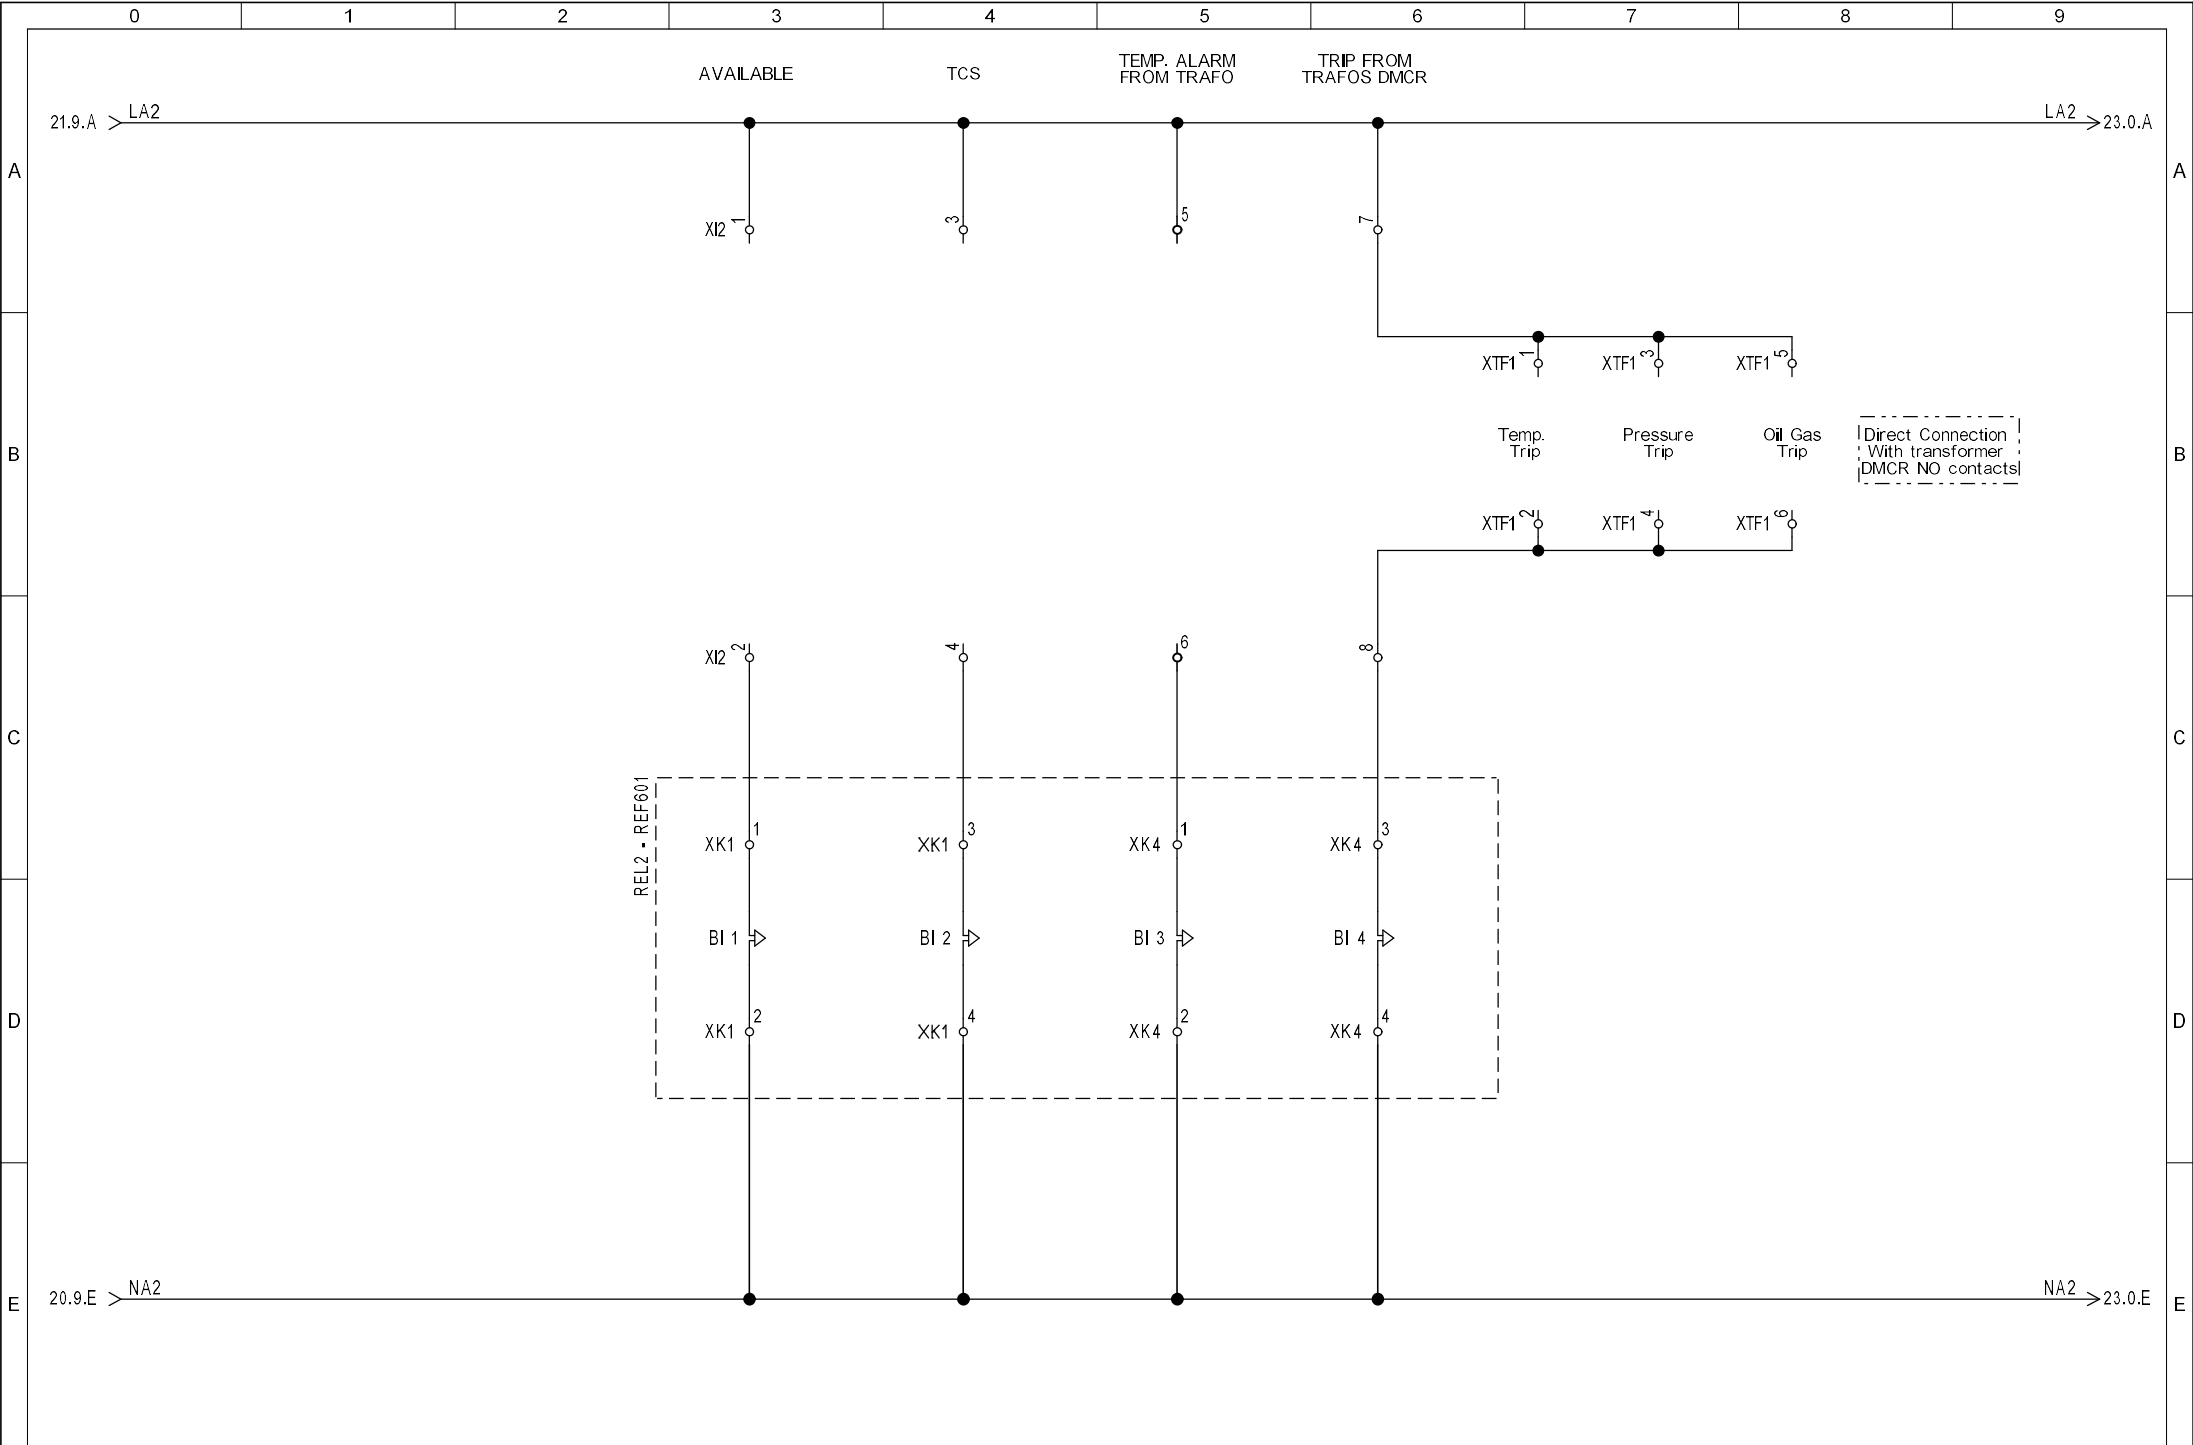


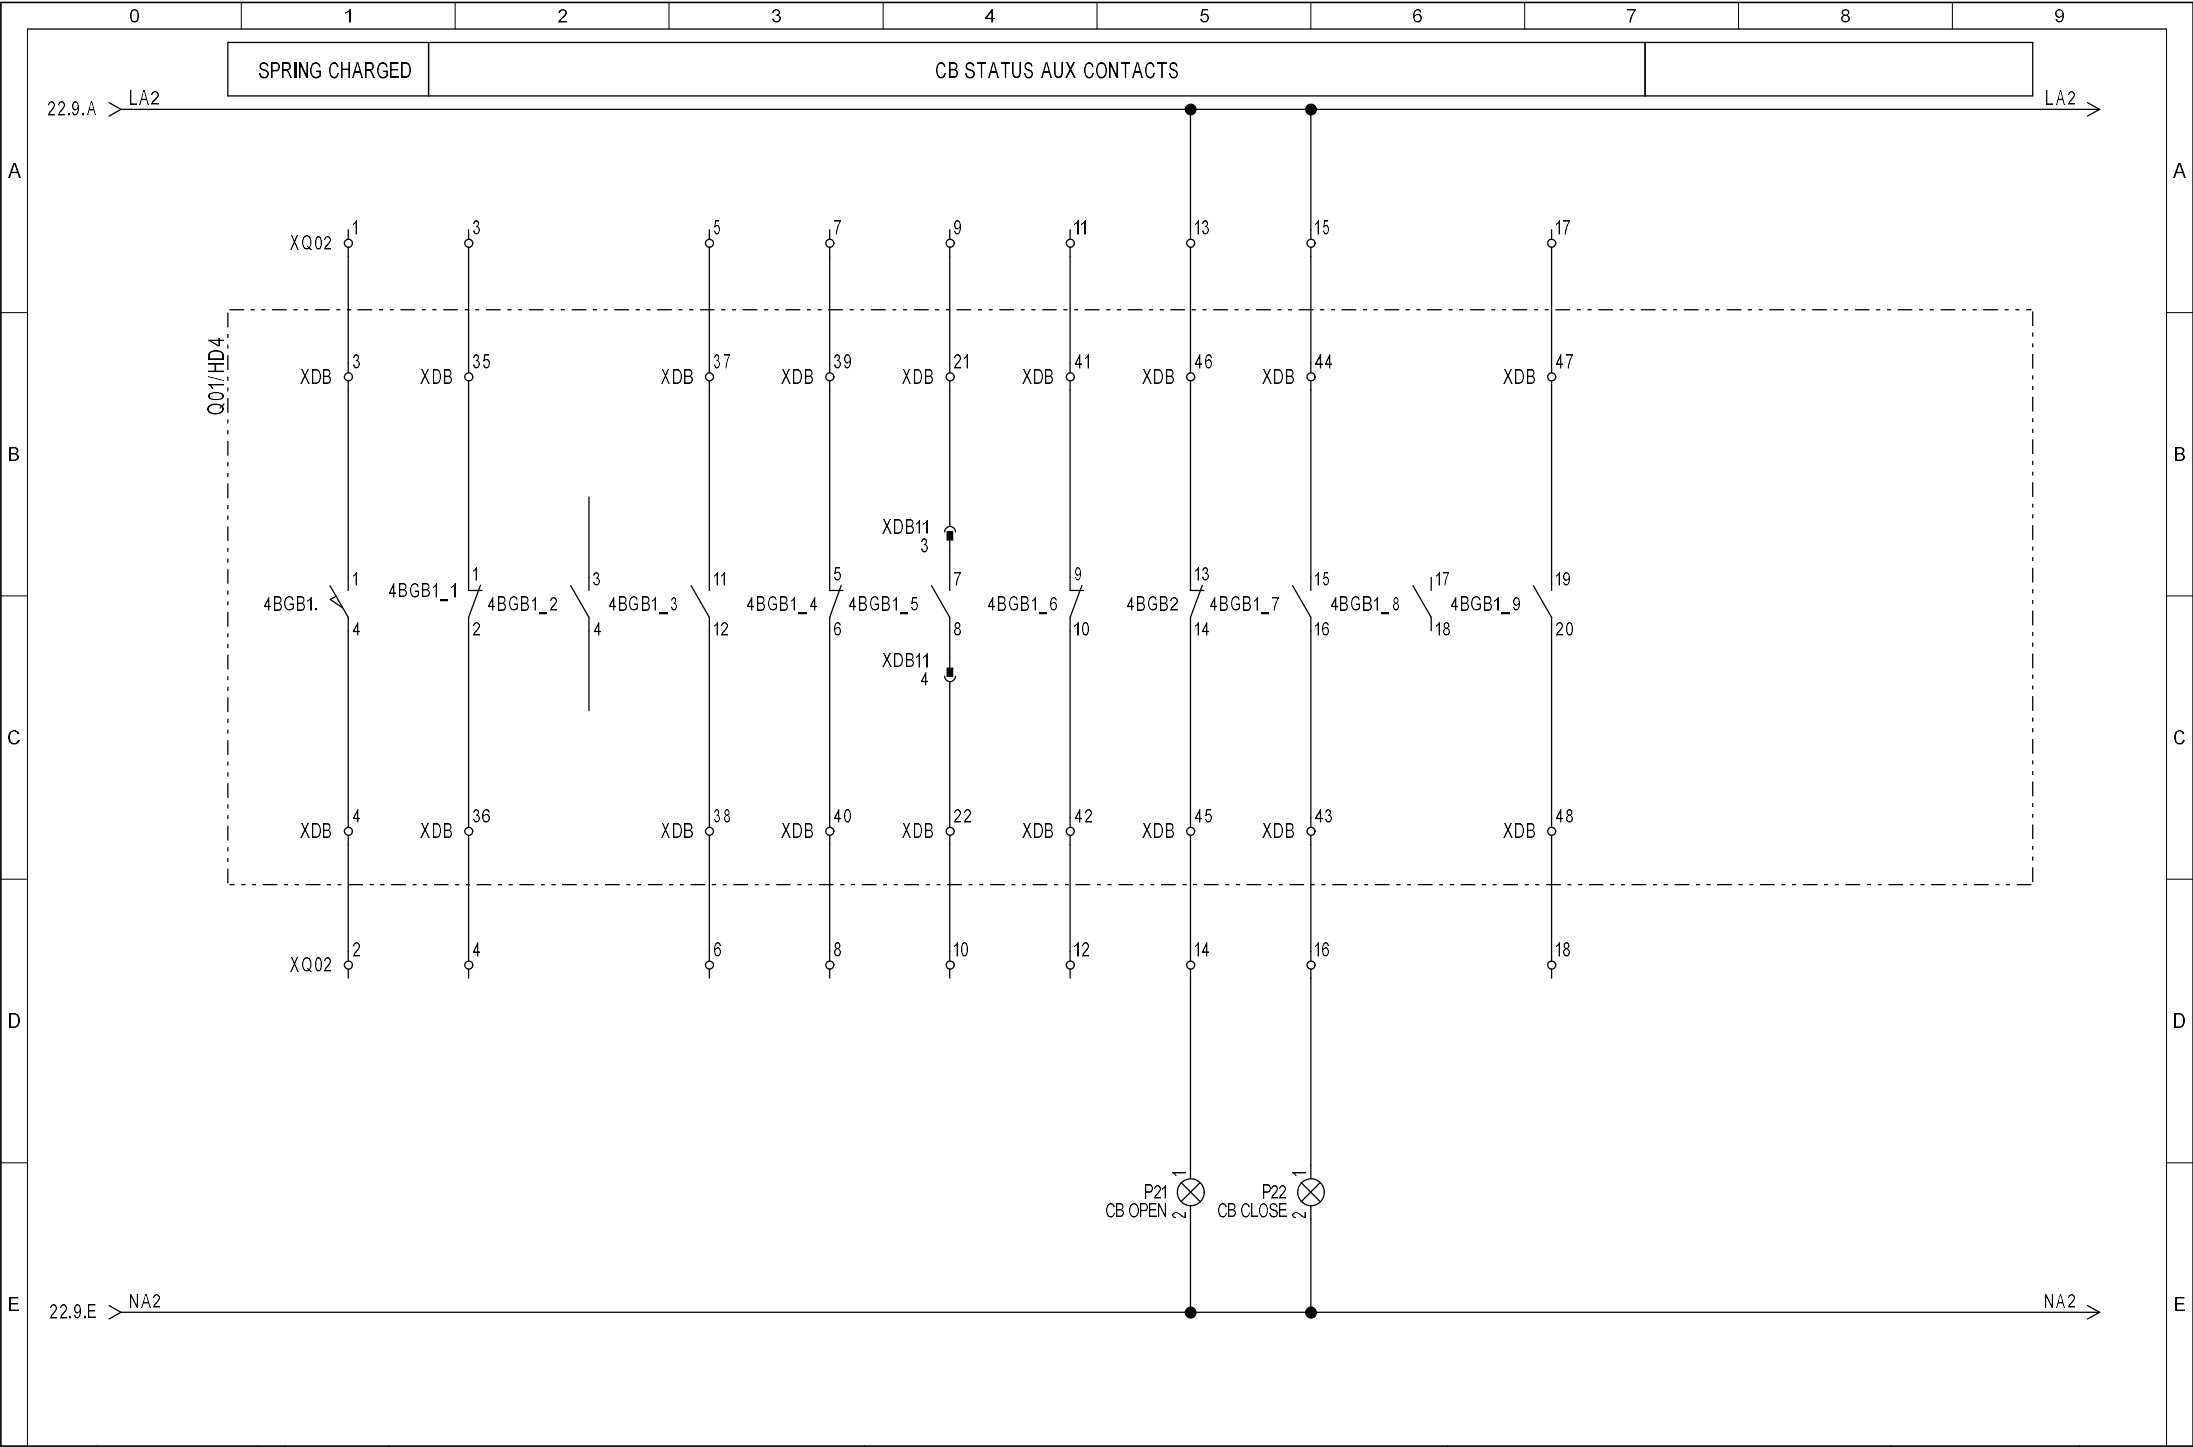


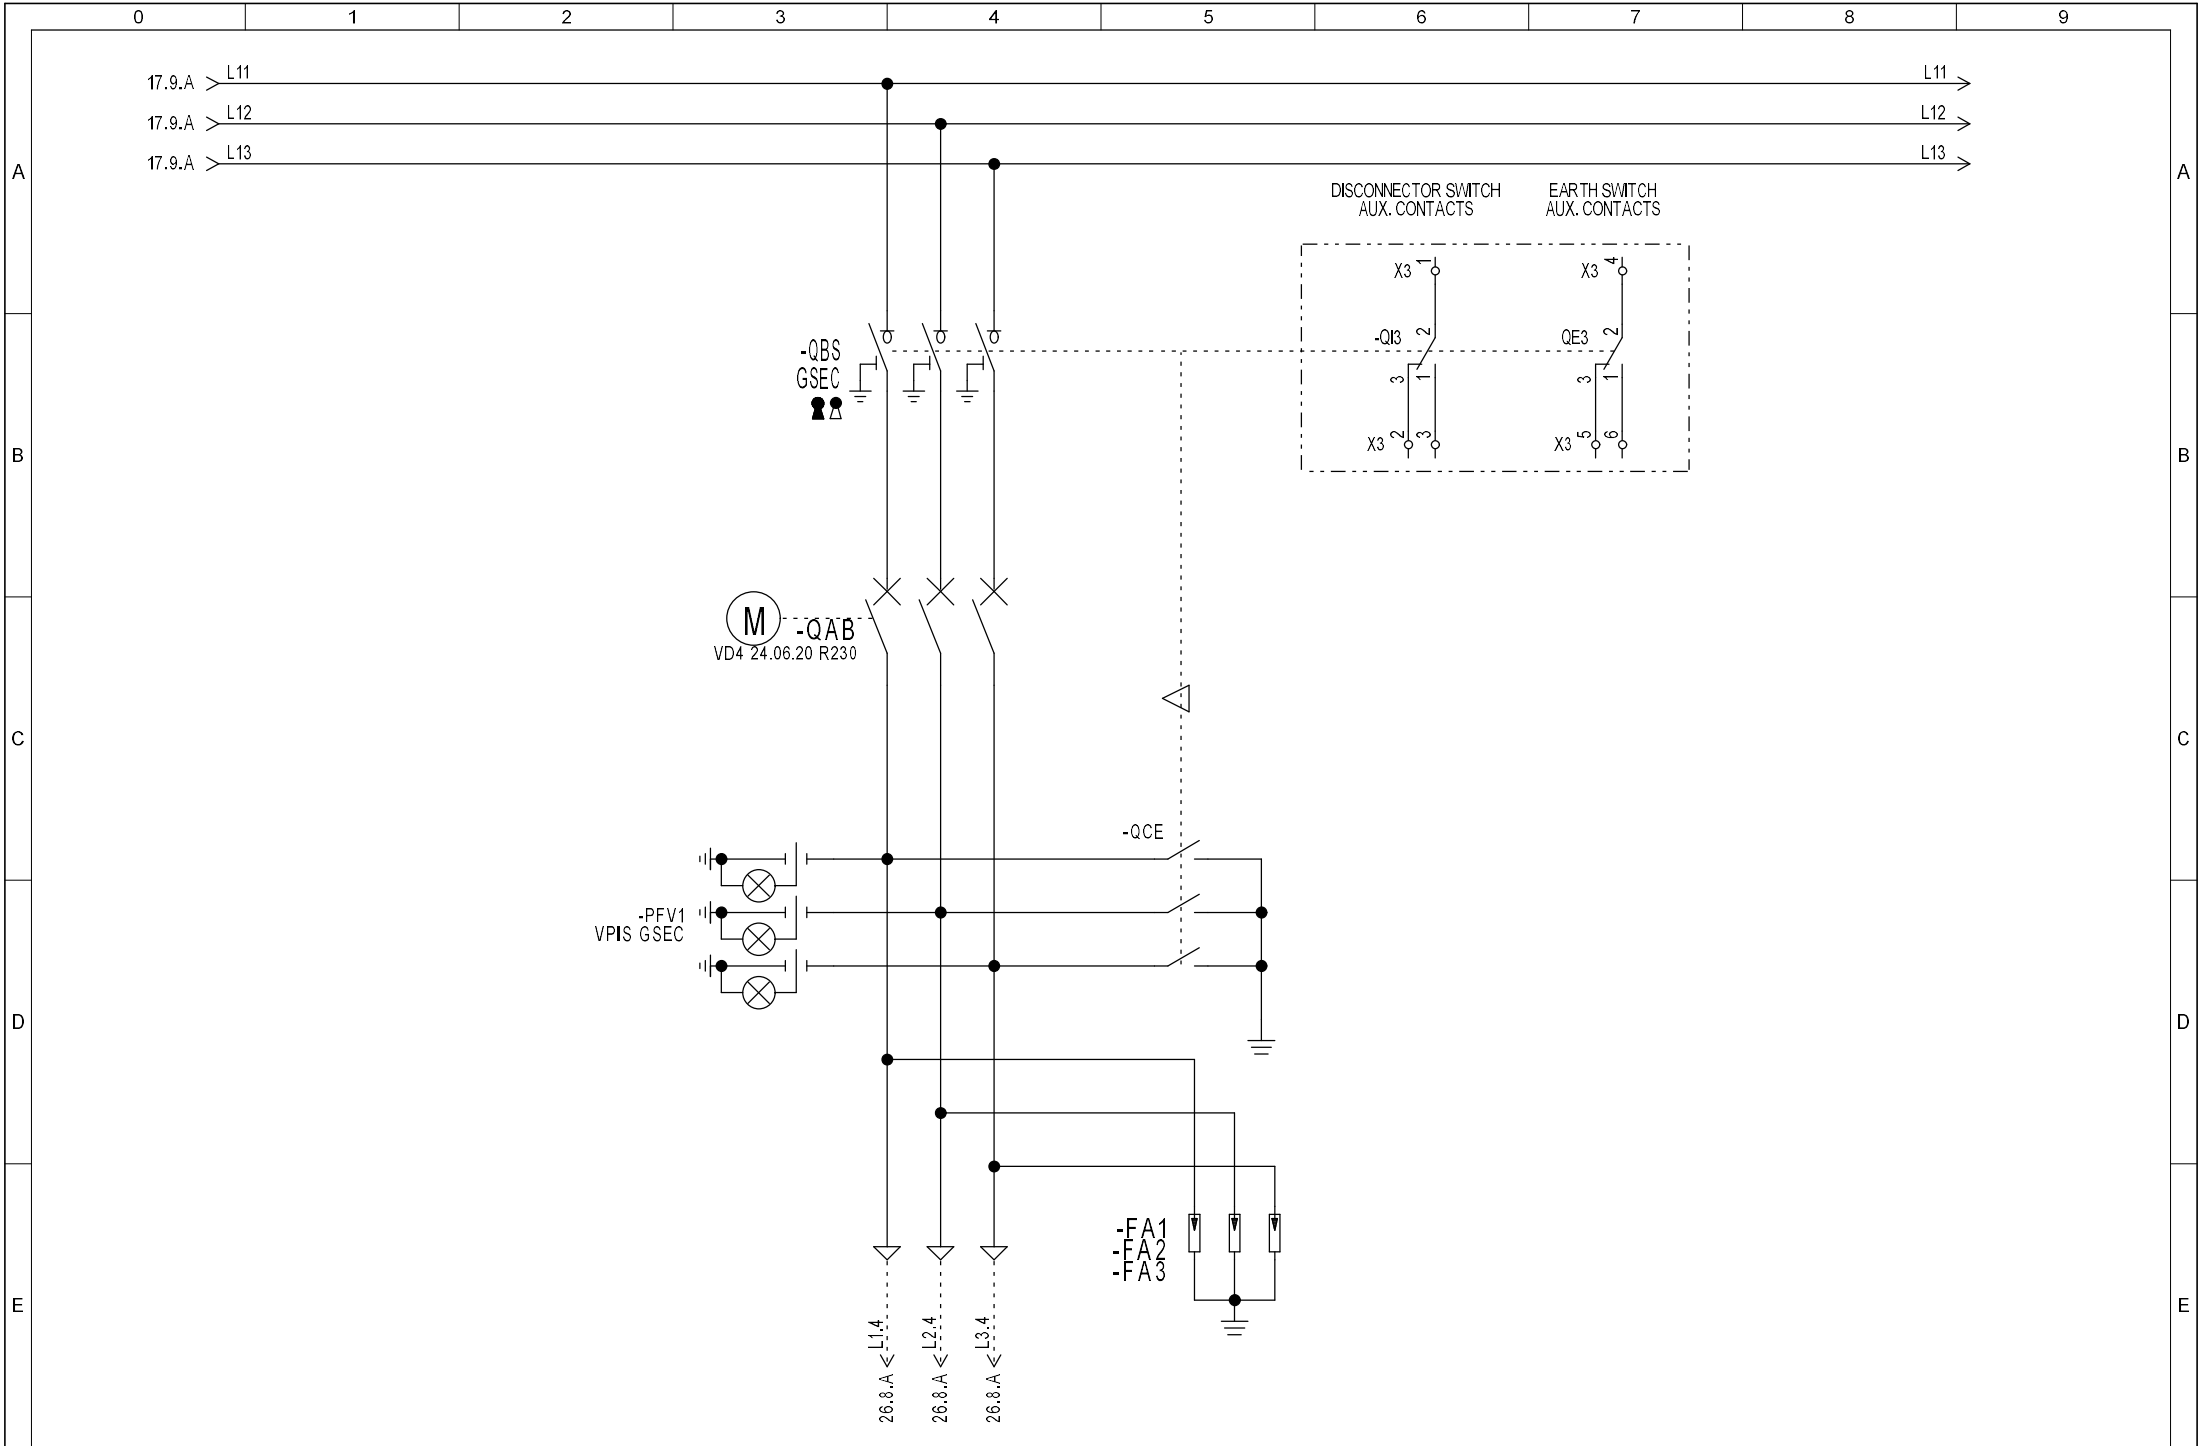


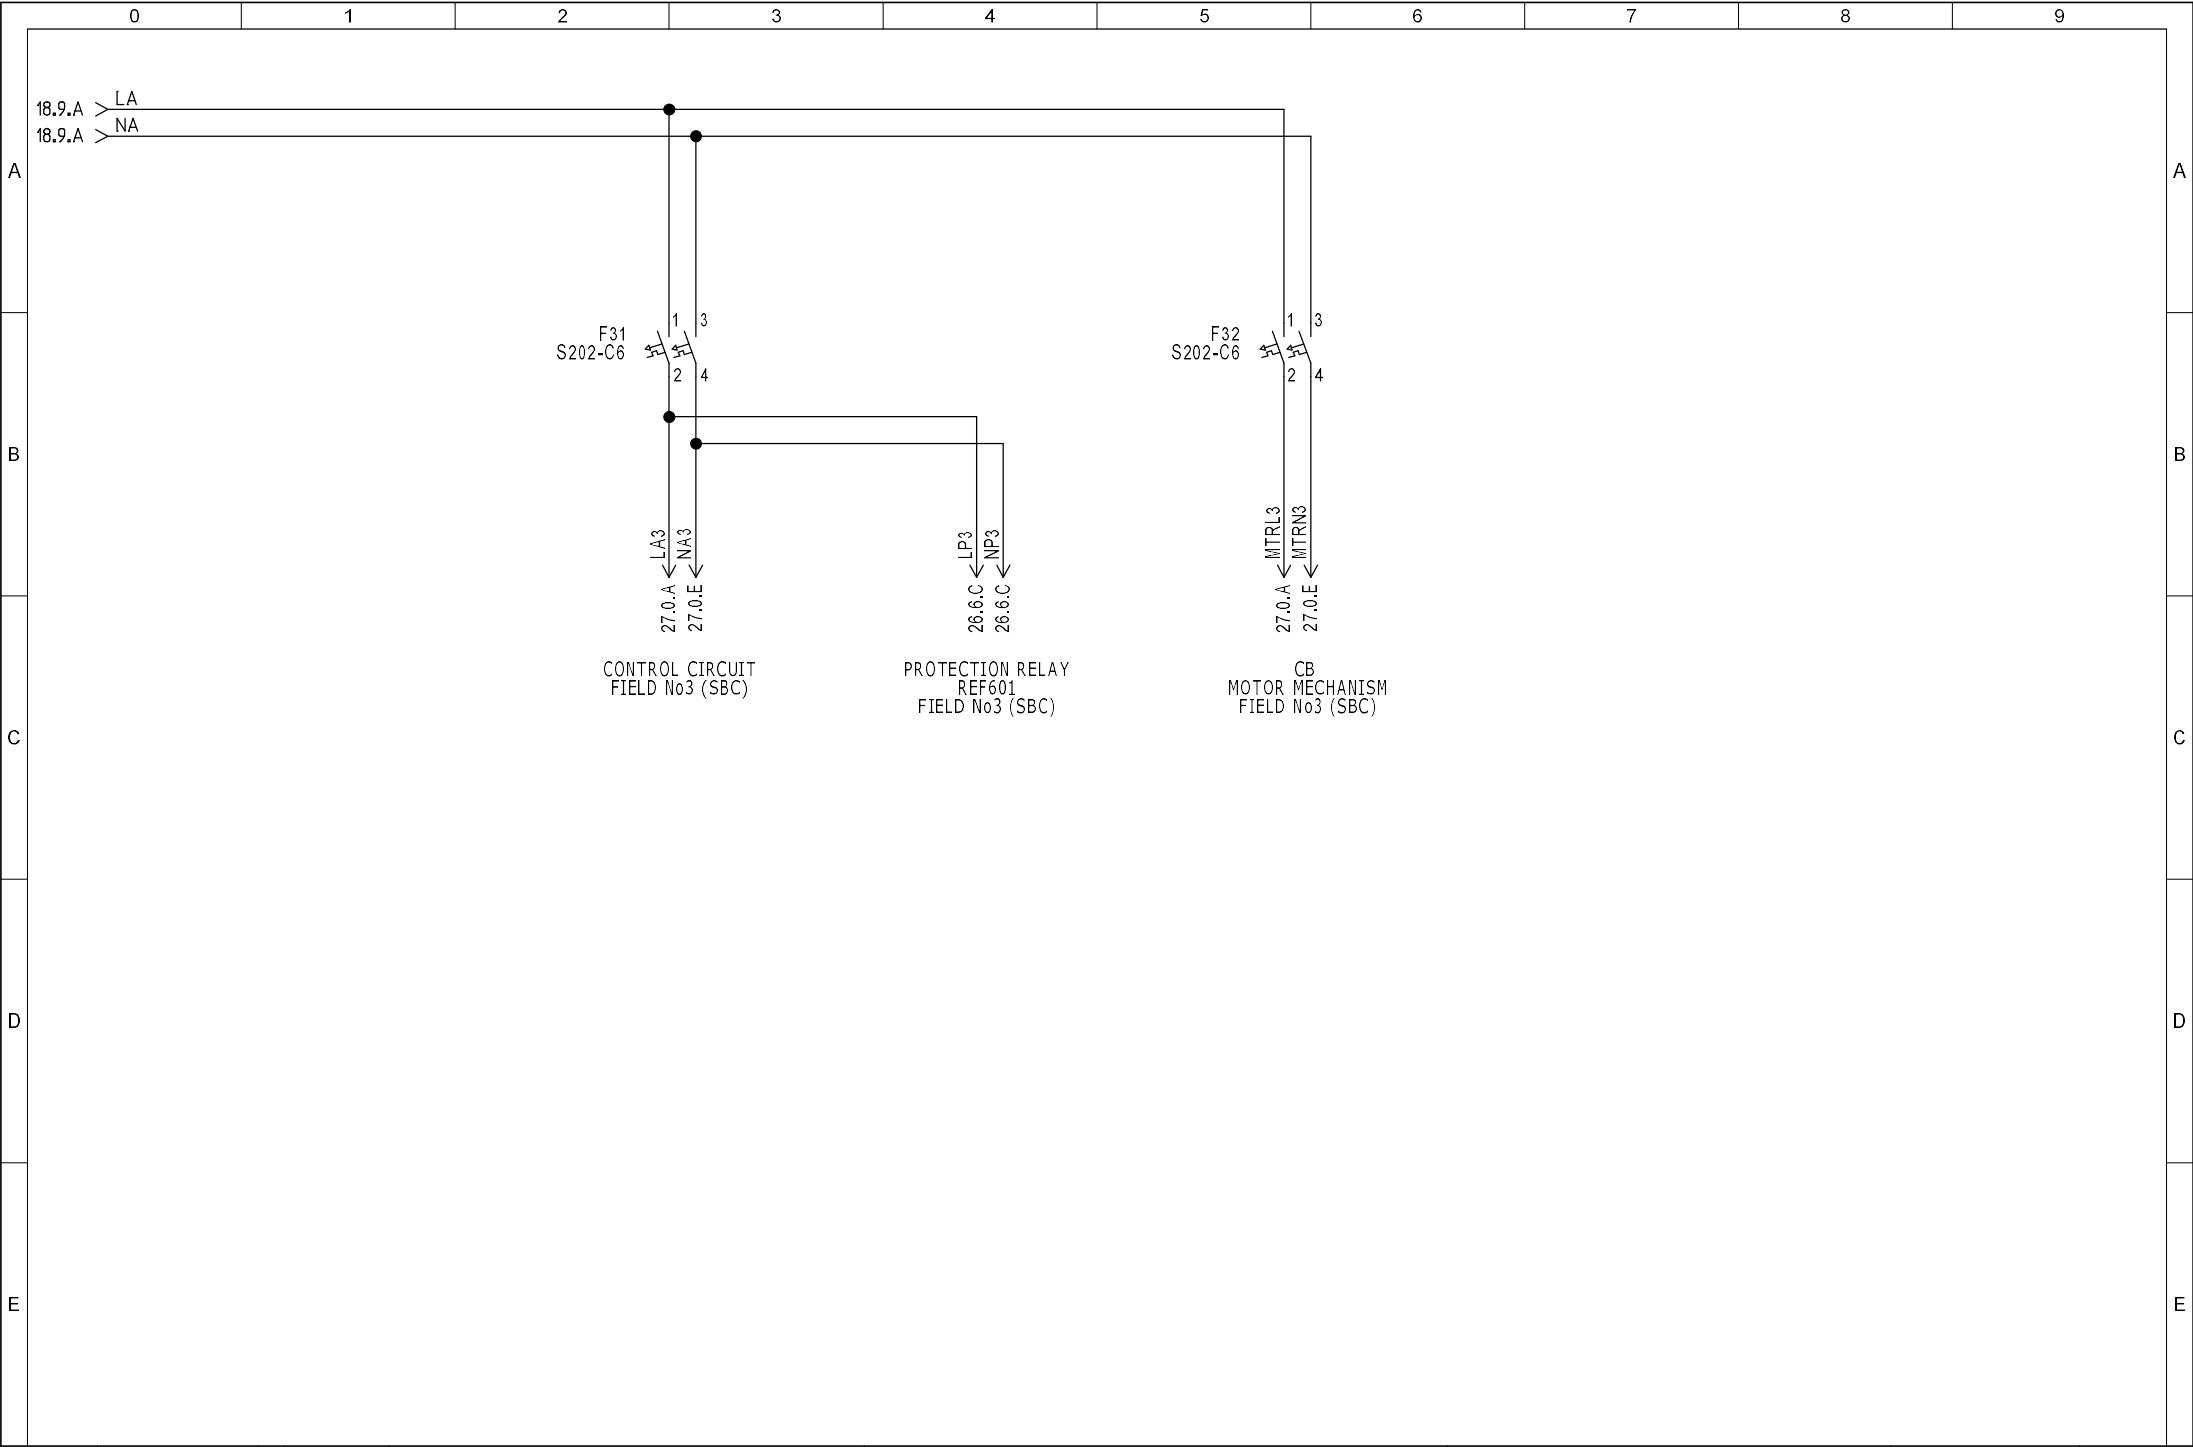


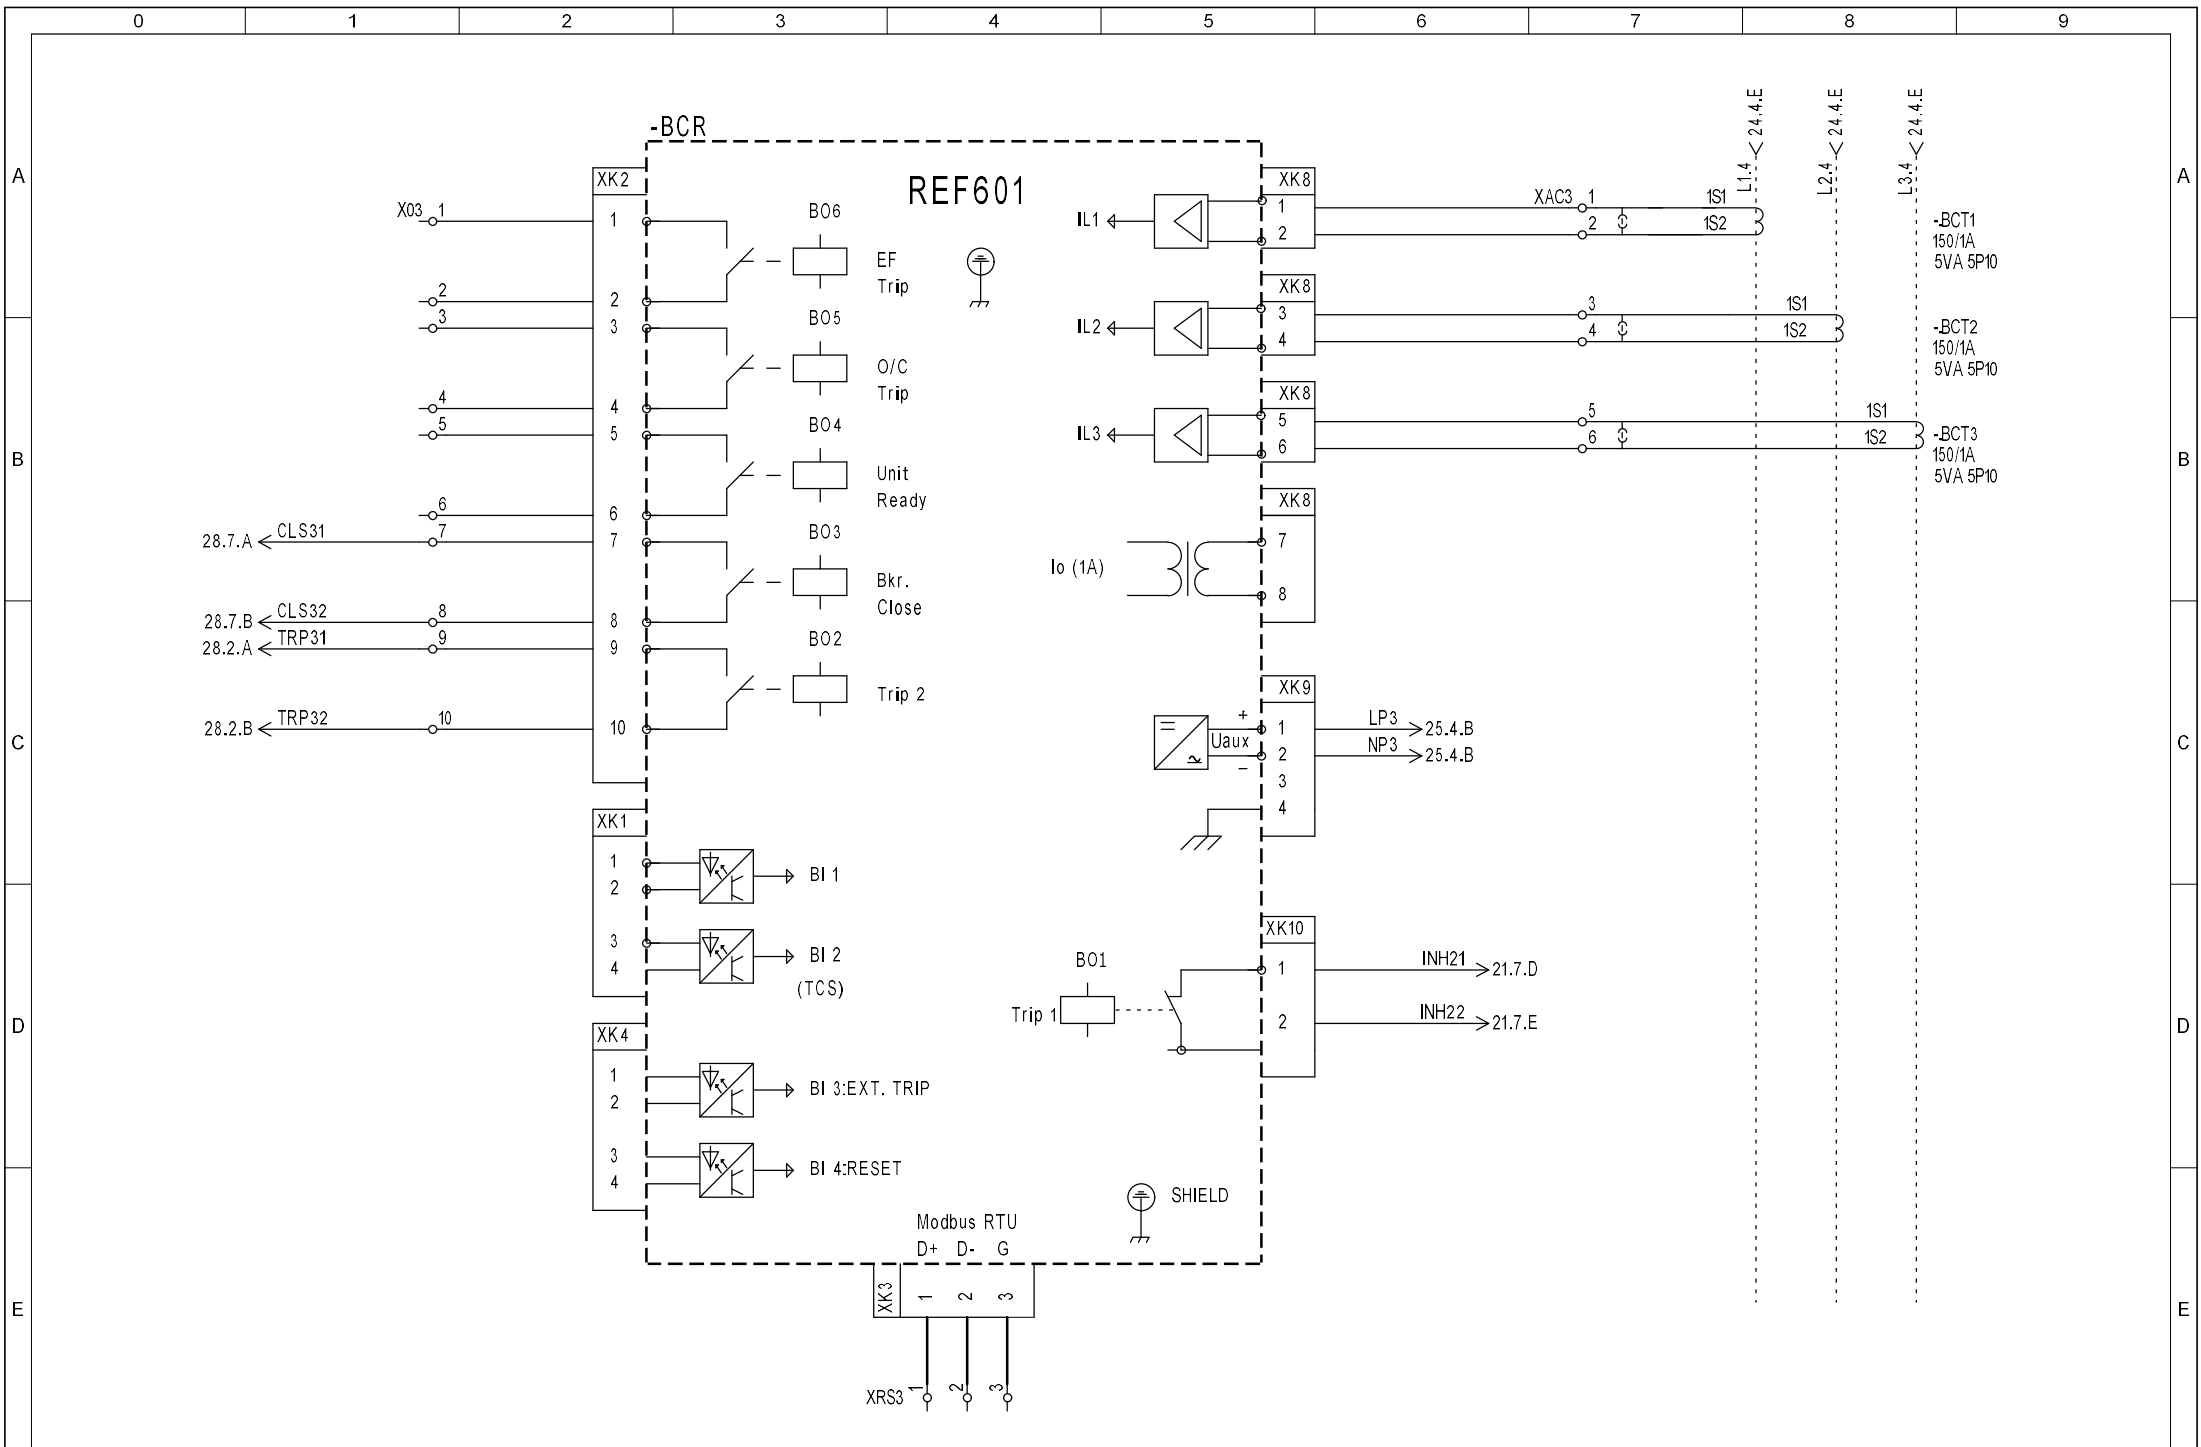

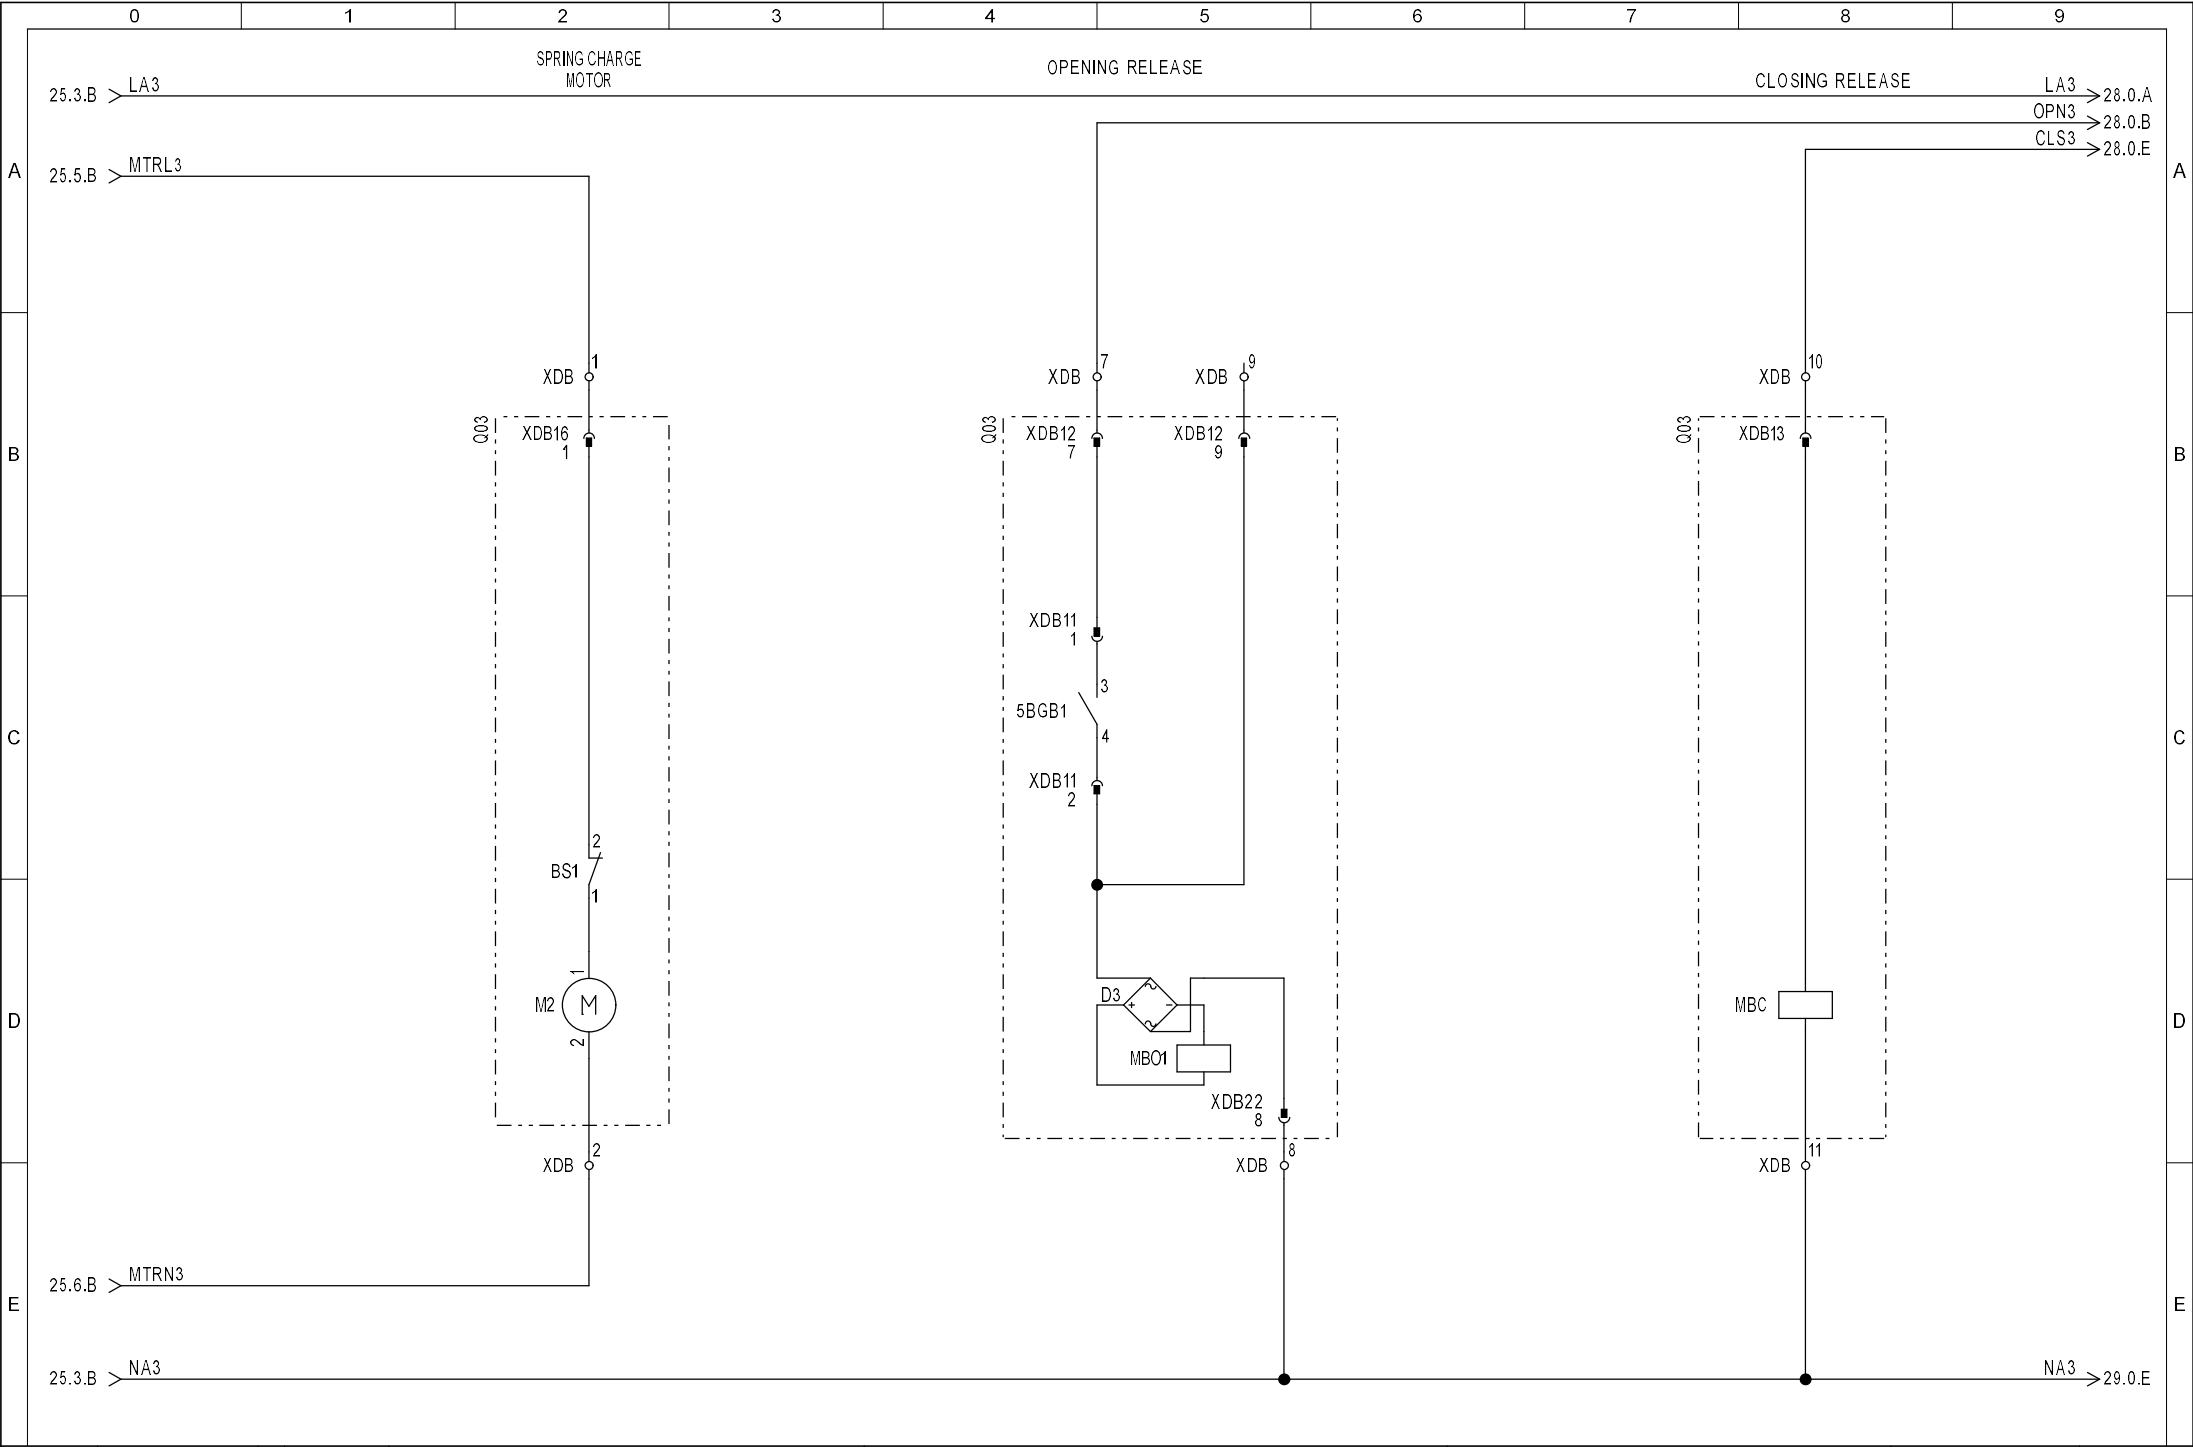

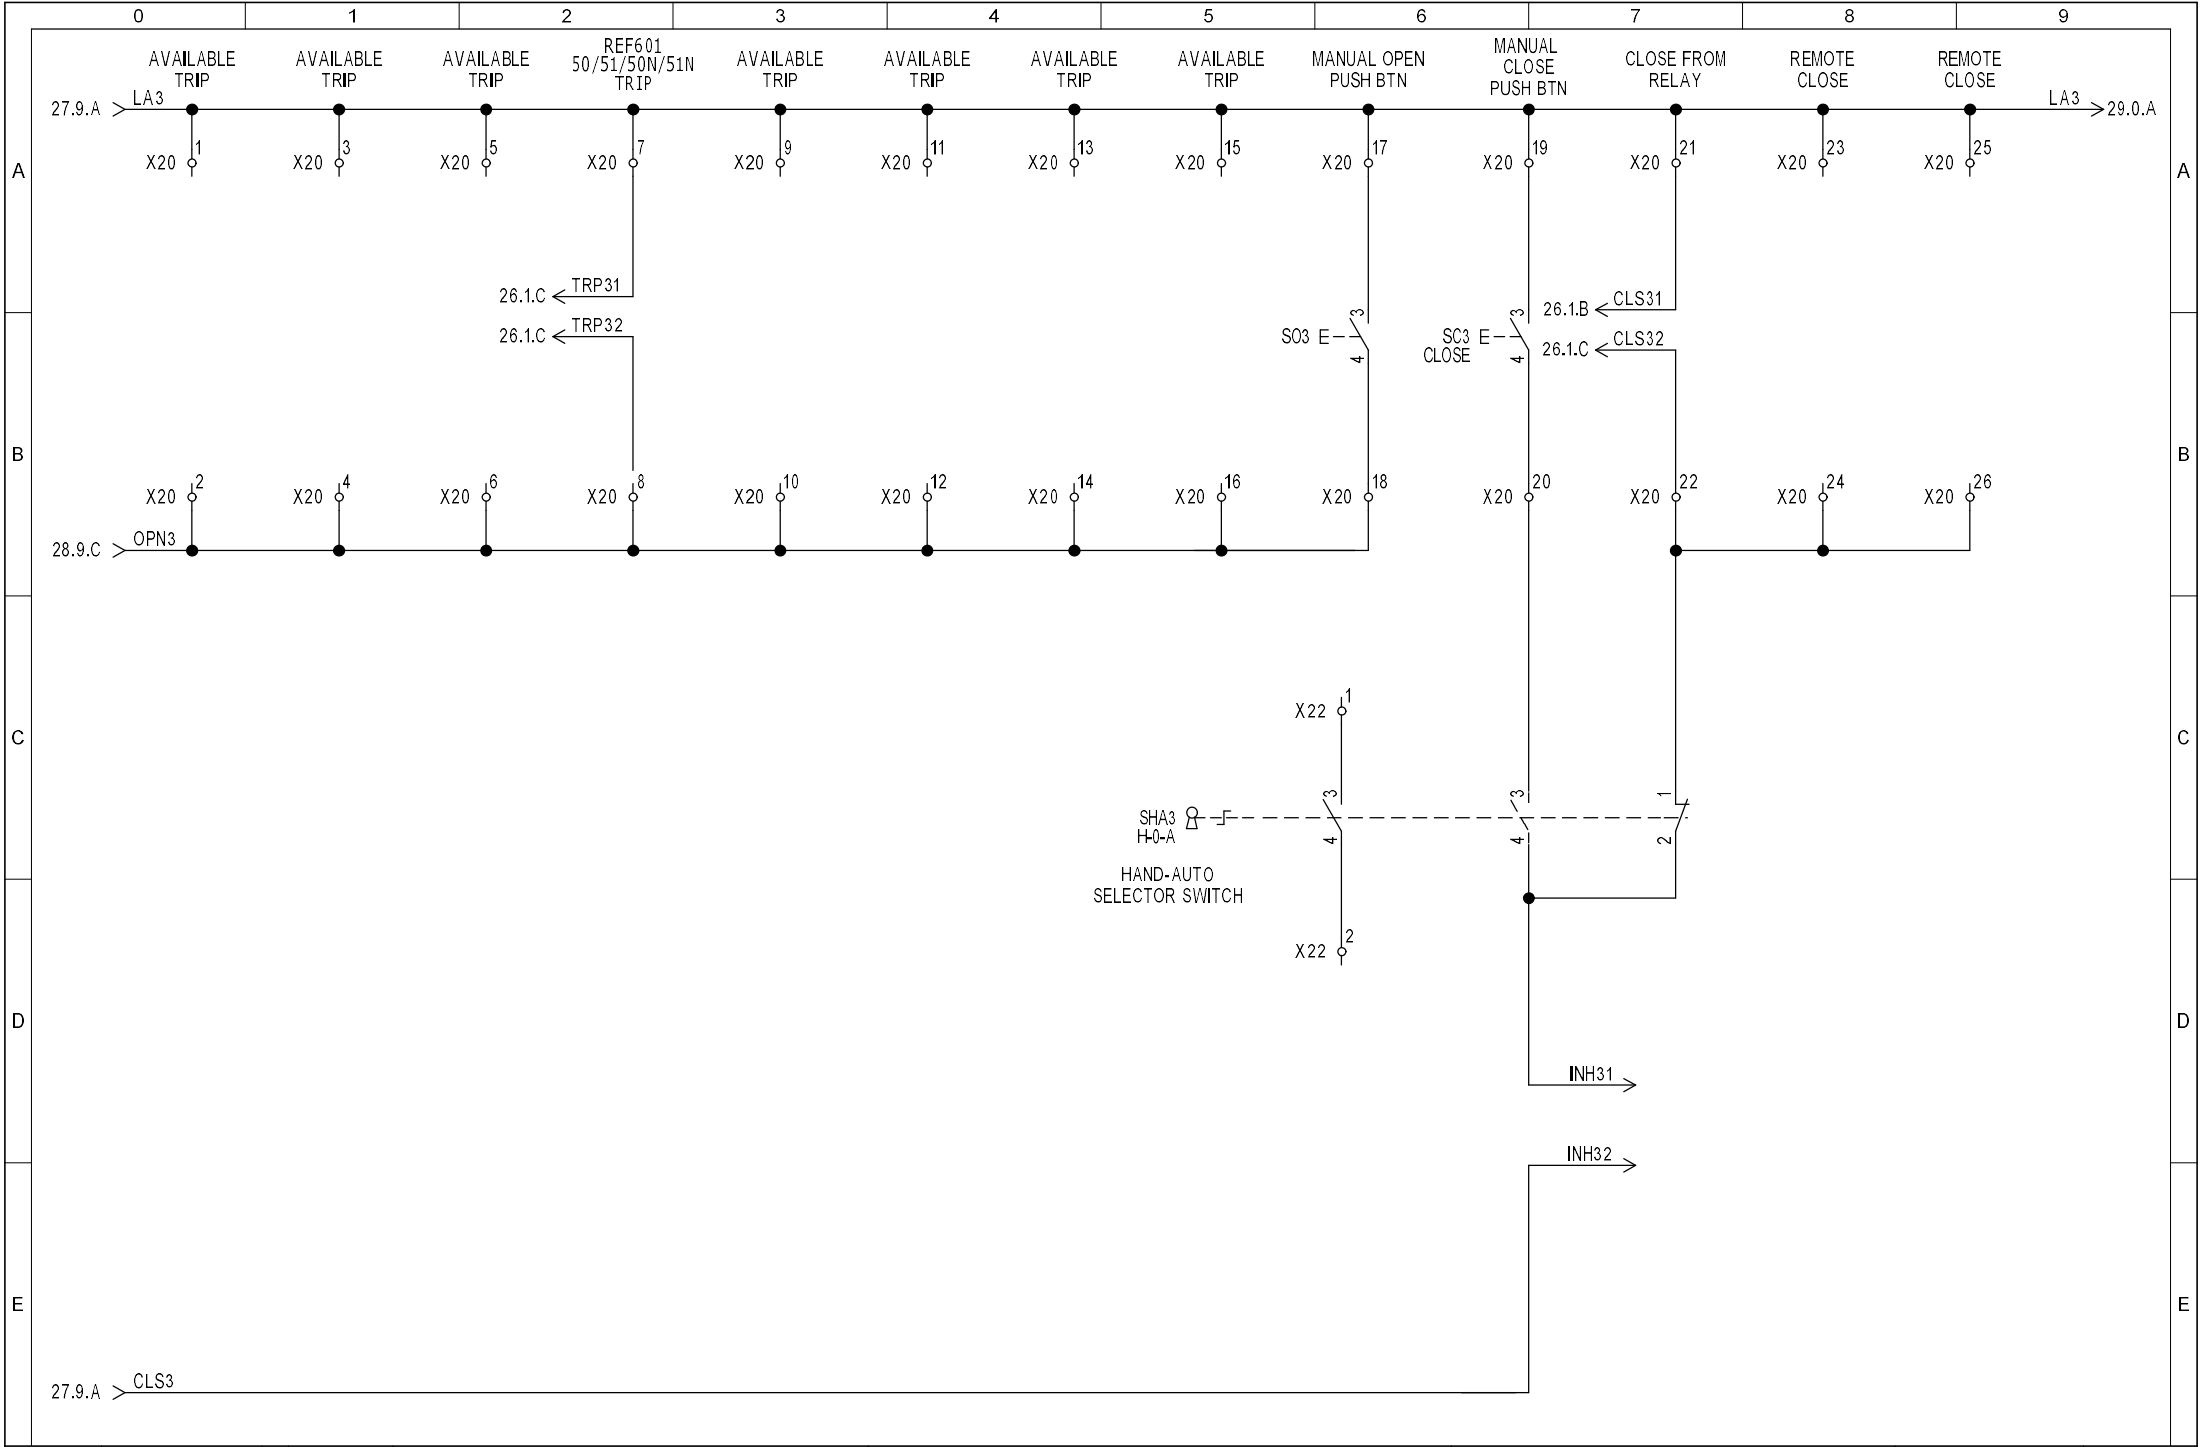

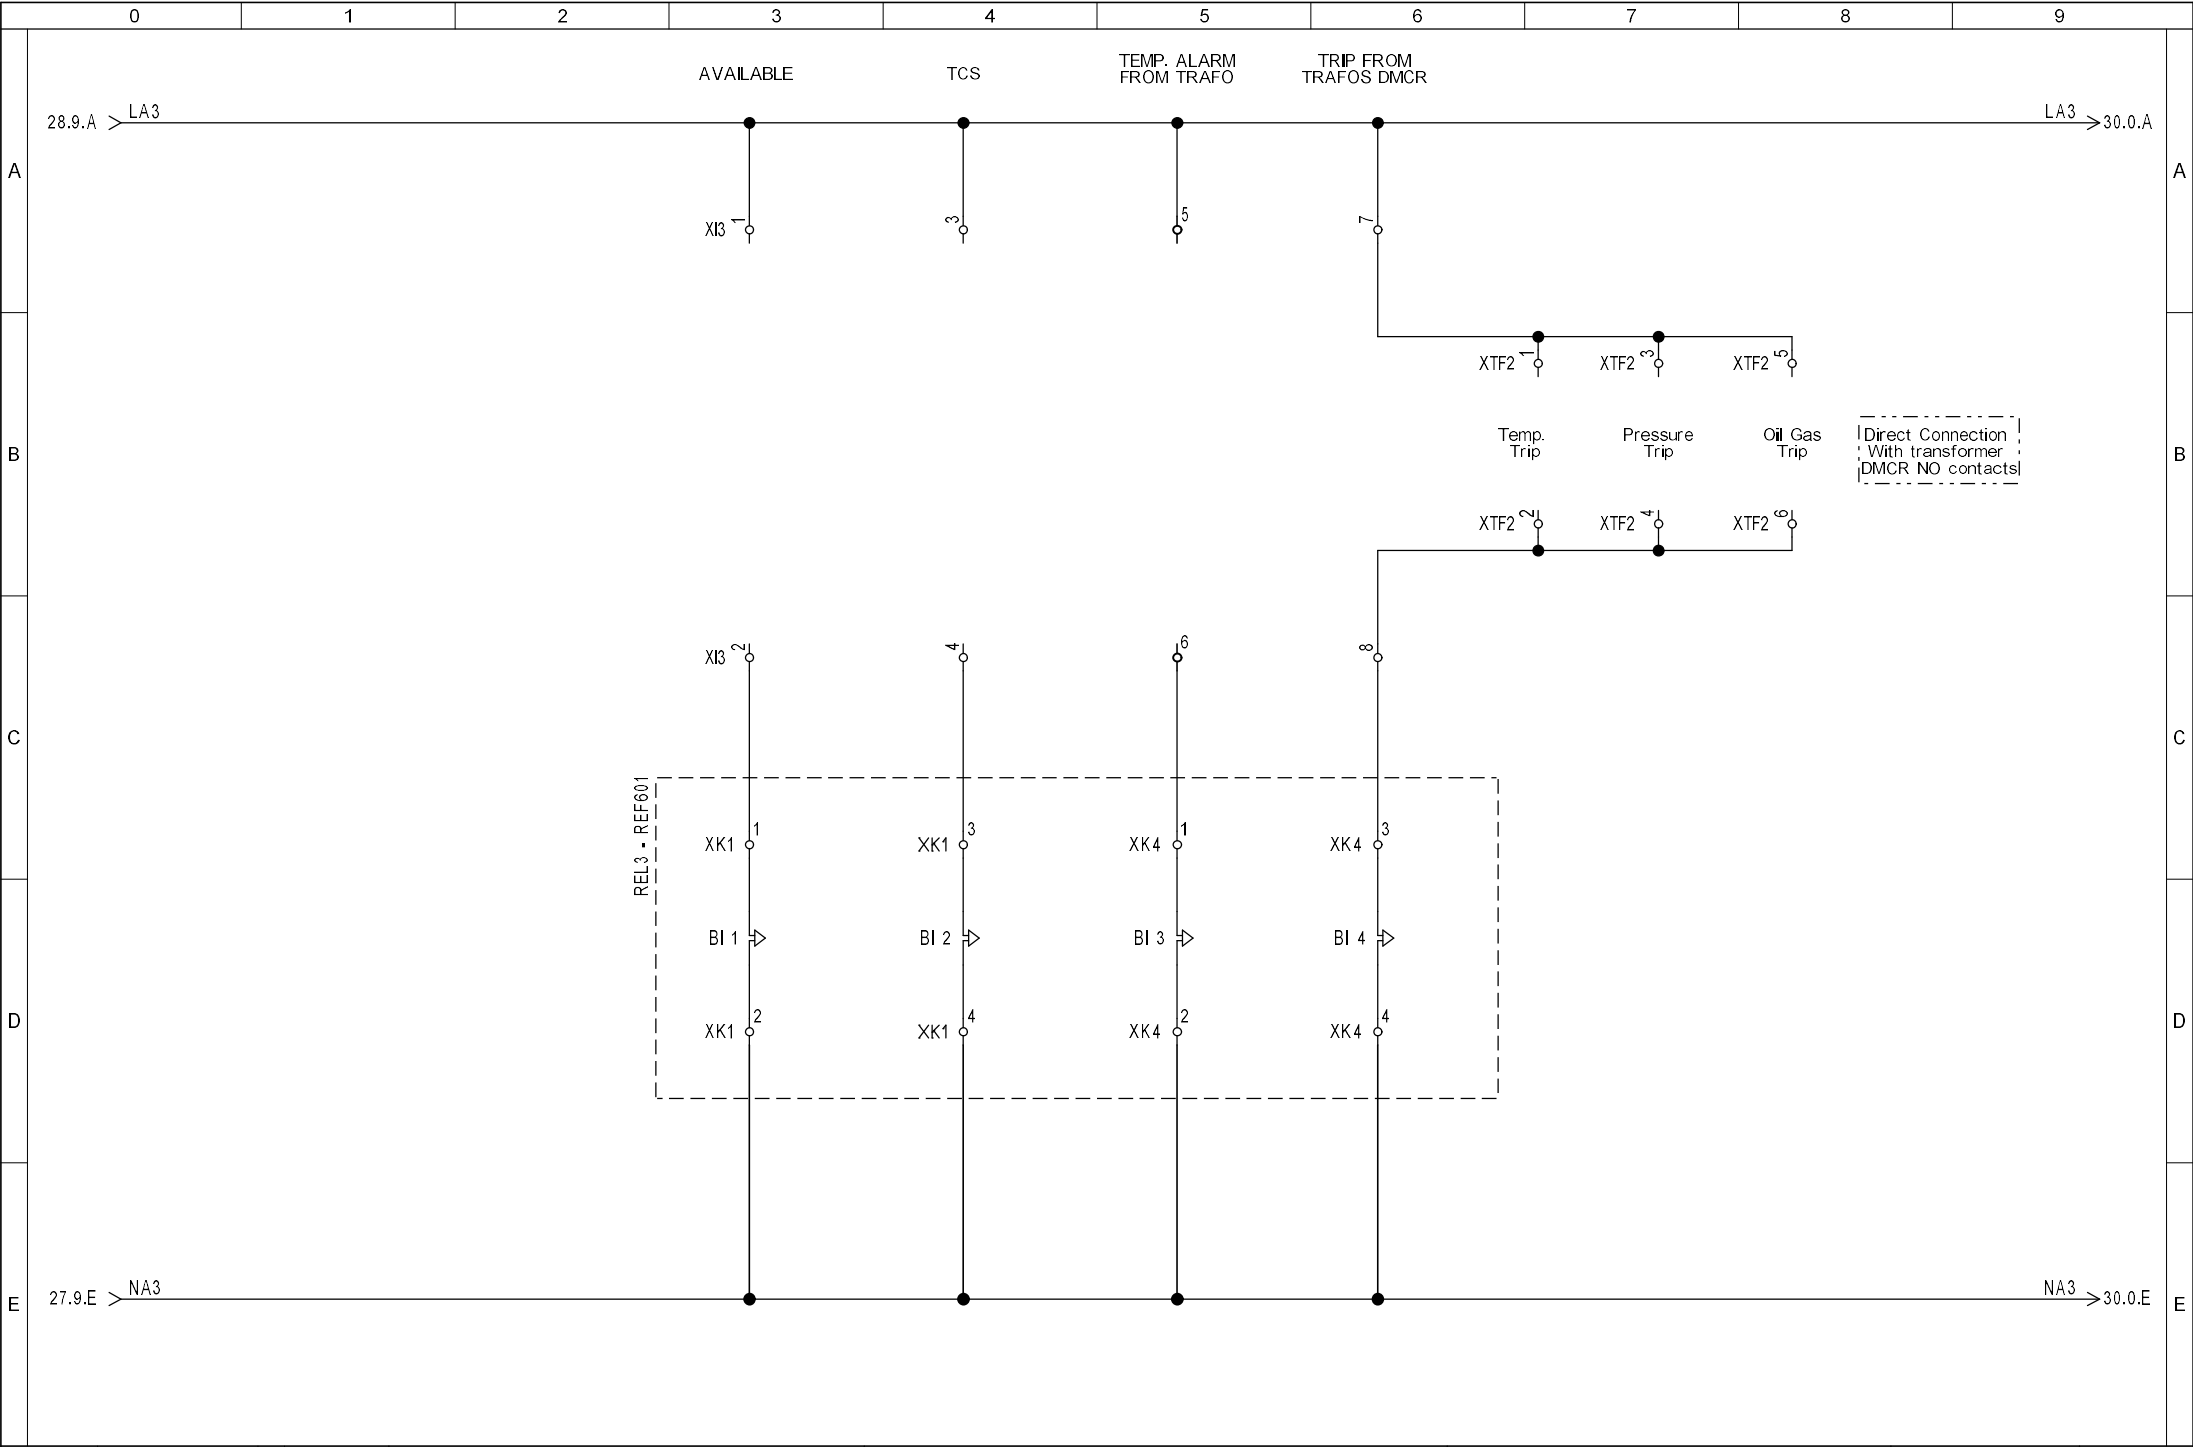

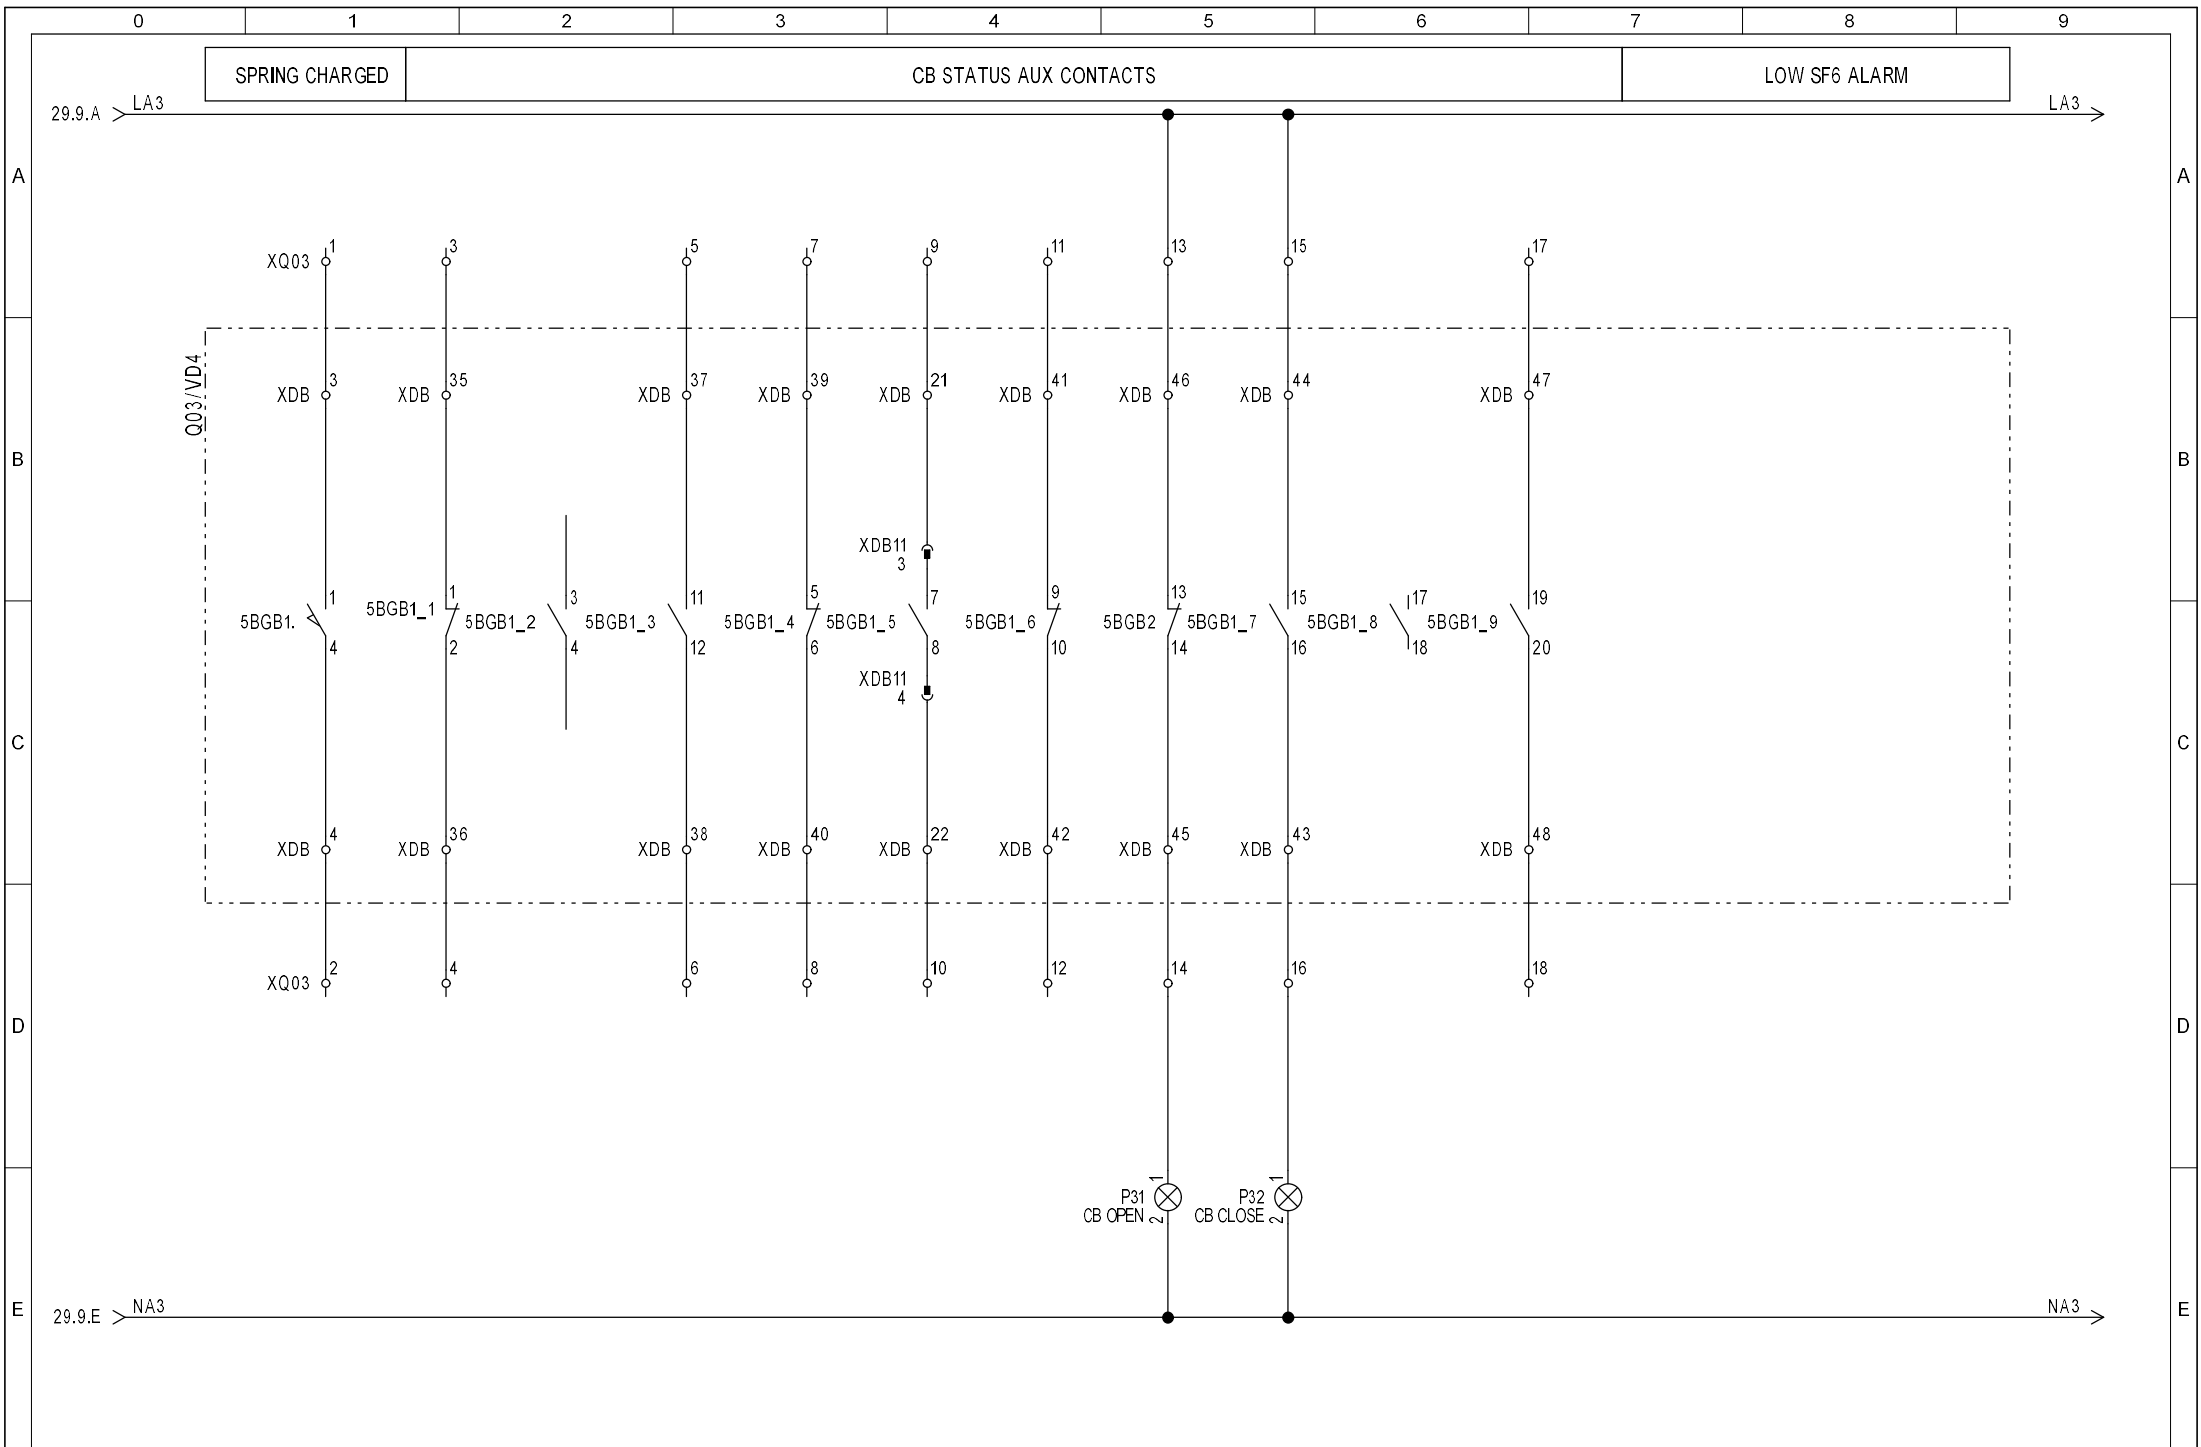

SEE FILE: ANARITA MV PANEL