


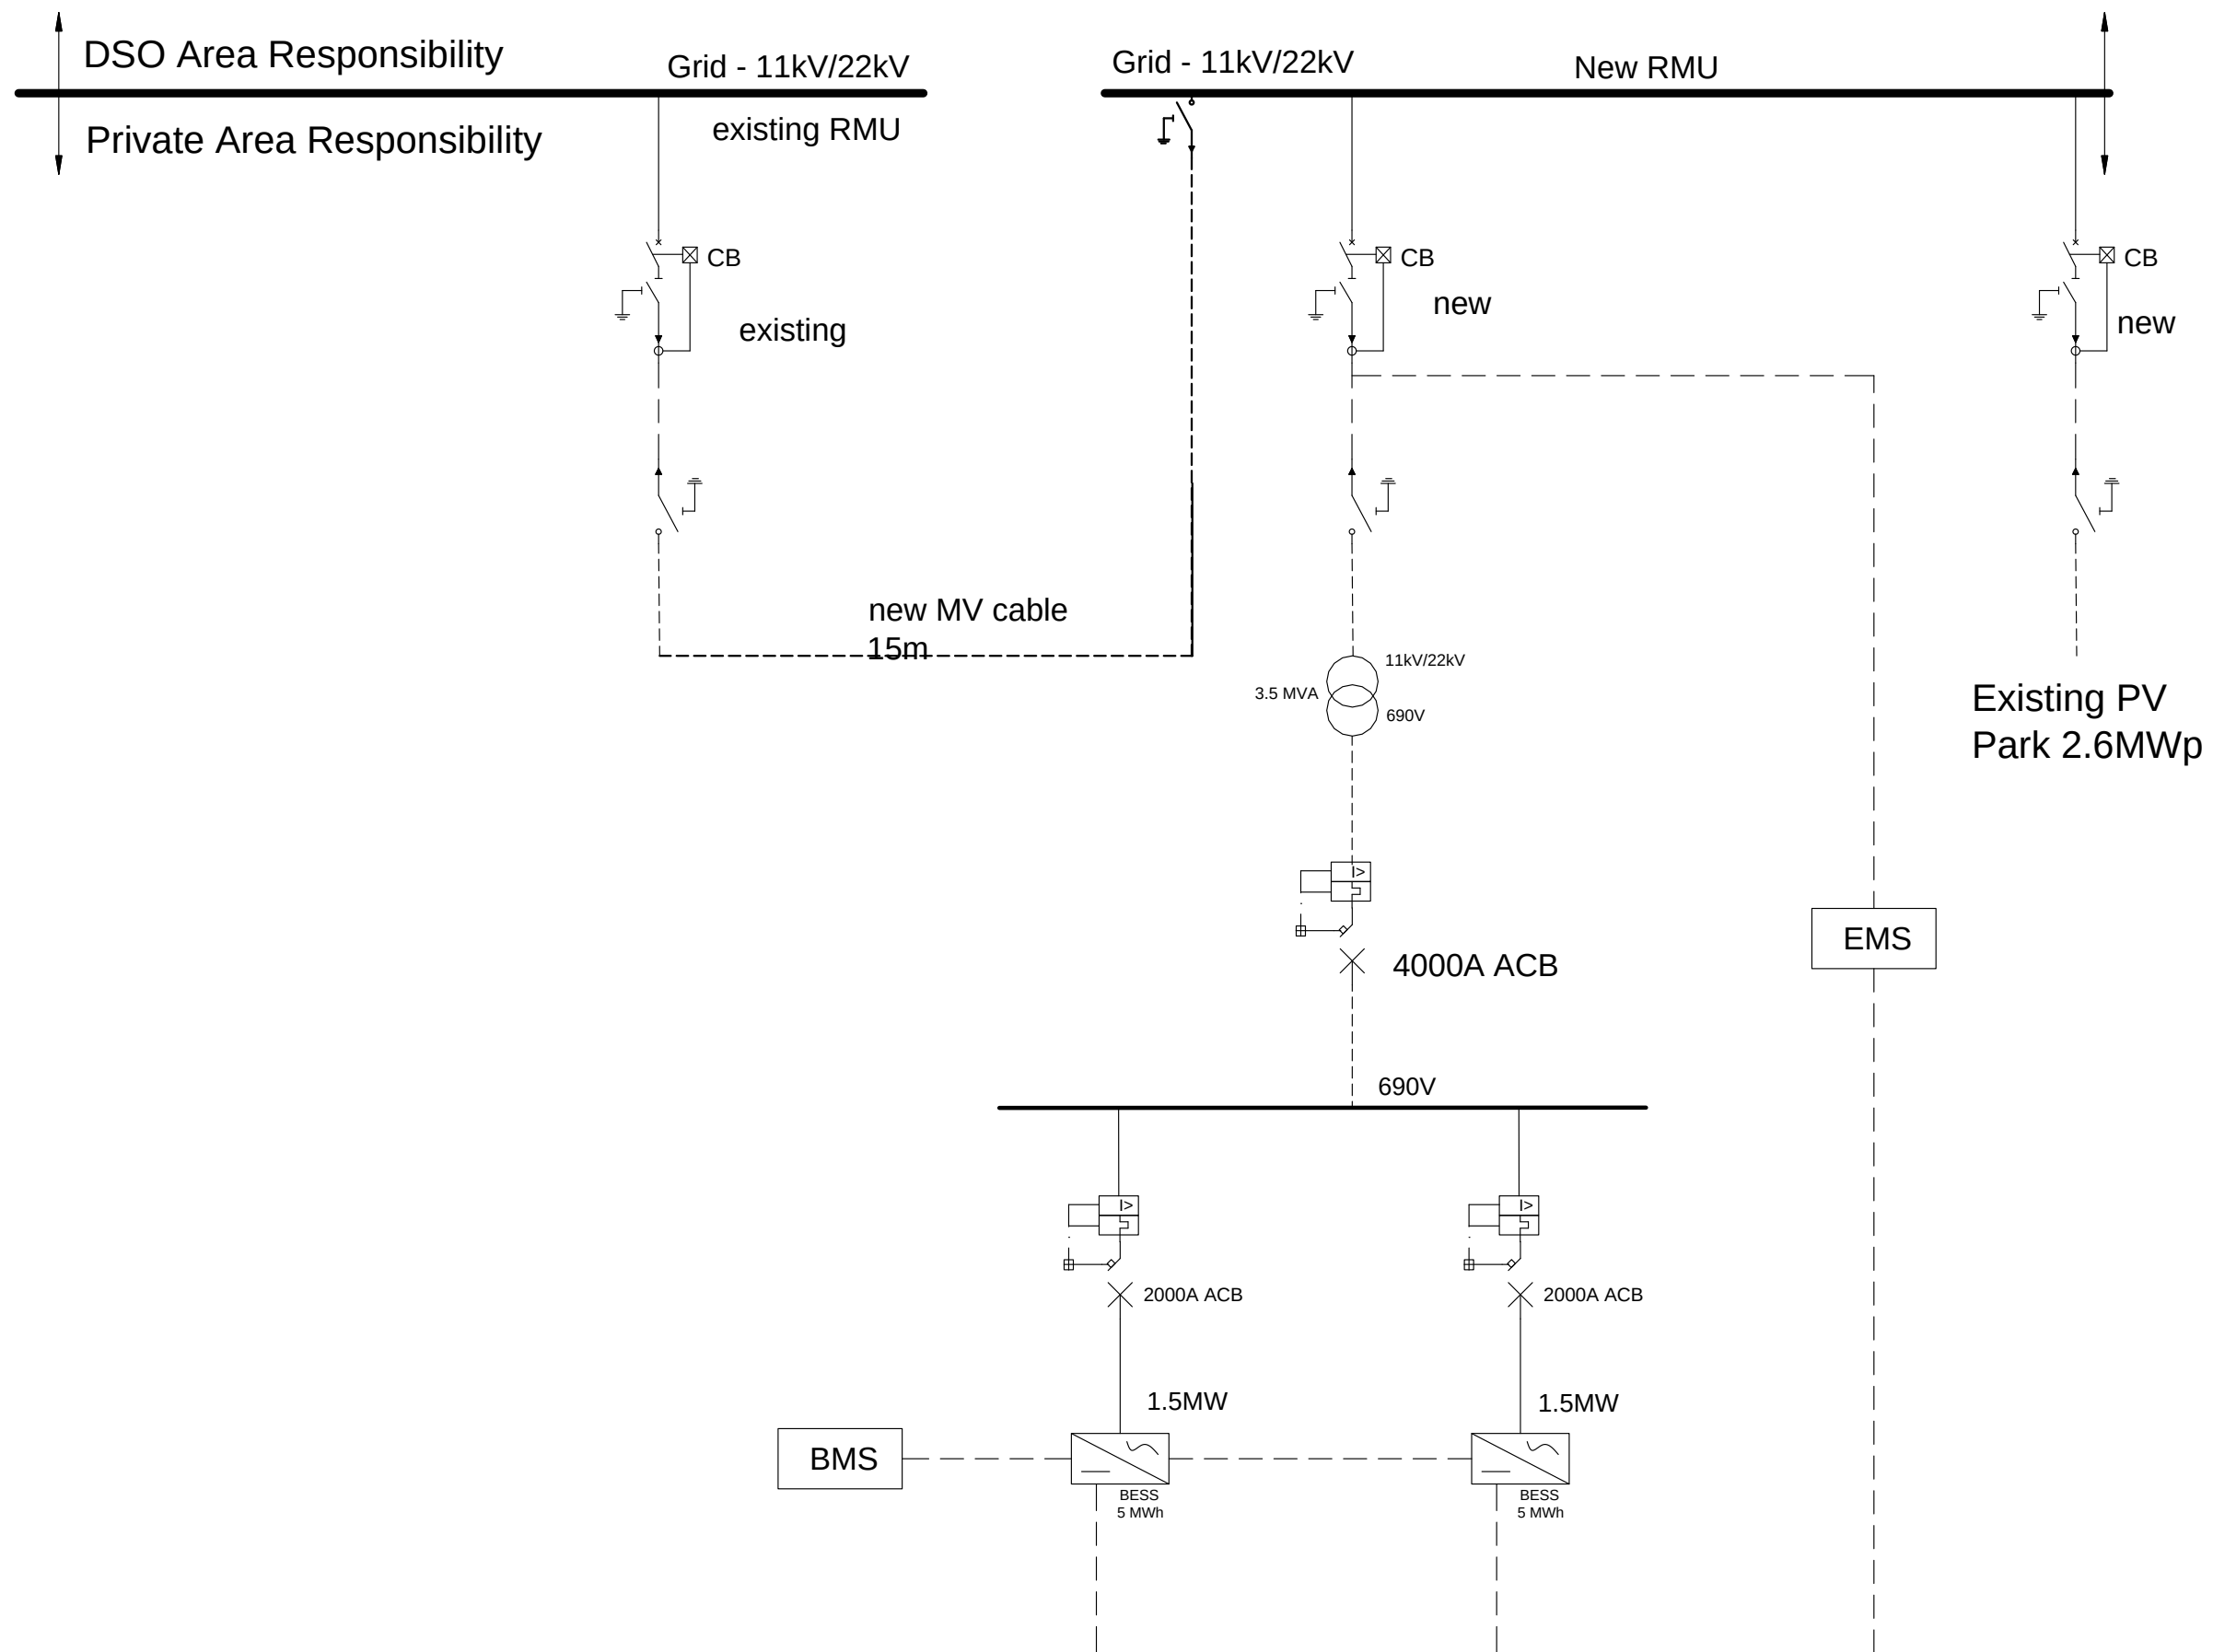

Project description:		Details:	
Dianary 1 2.6MWp		Dianary 1 - BESS	
Design firm:		Design by:	Design date:
Iacovos Charalambous		Iacovos Charalambous	07/11/2025
Client:		Revision by:	Revision date:
Abio Power LTD			Sheet No.: