


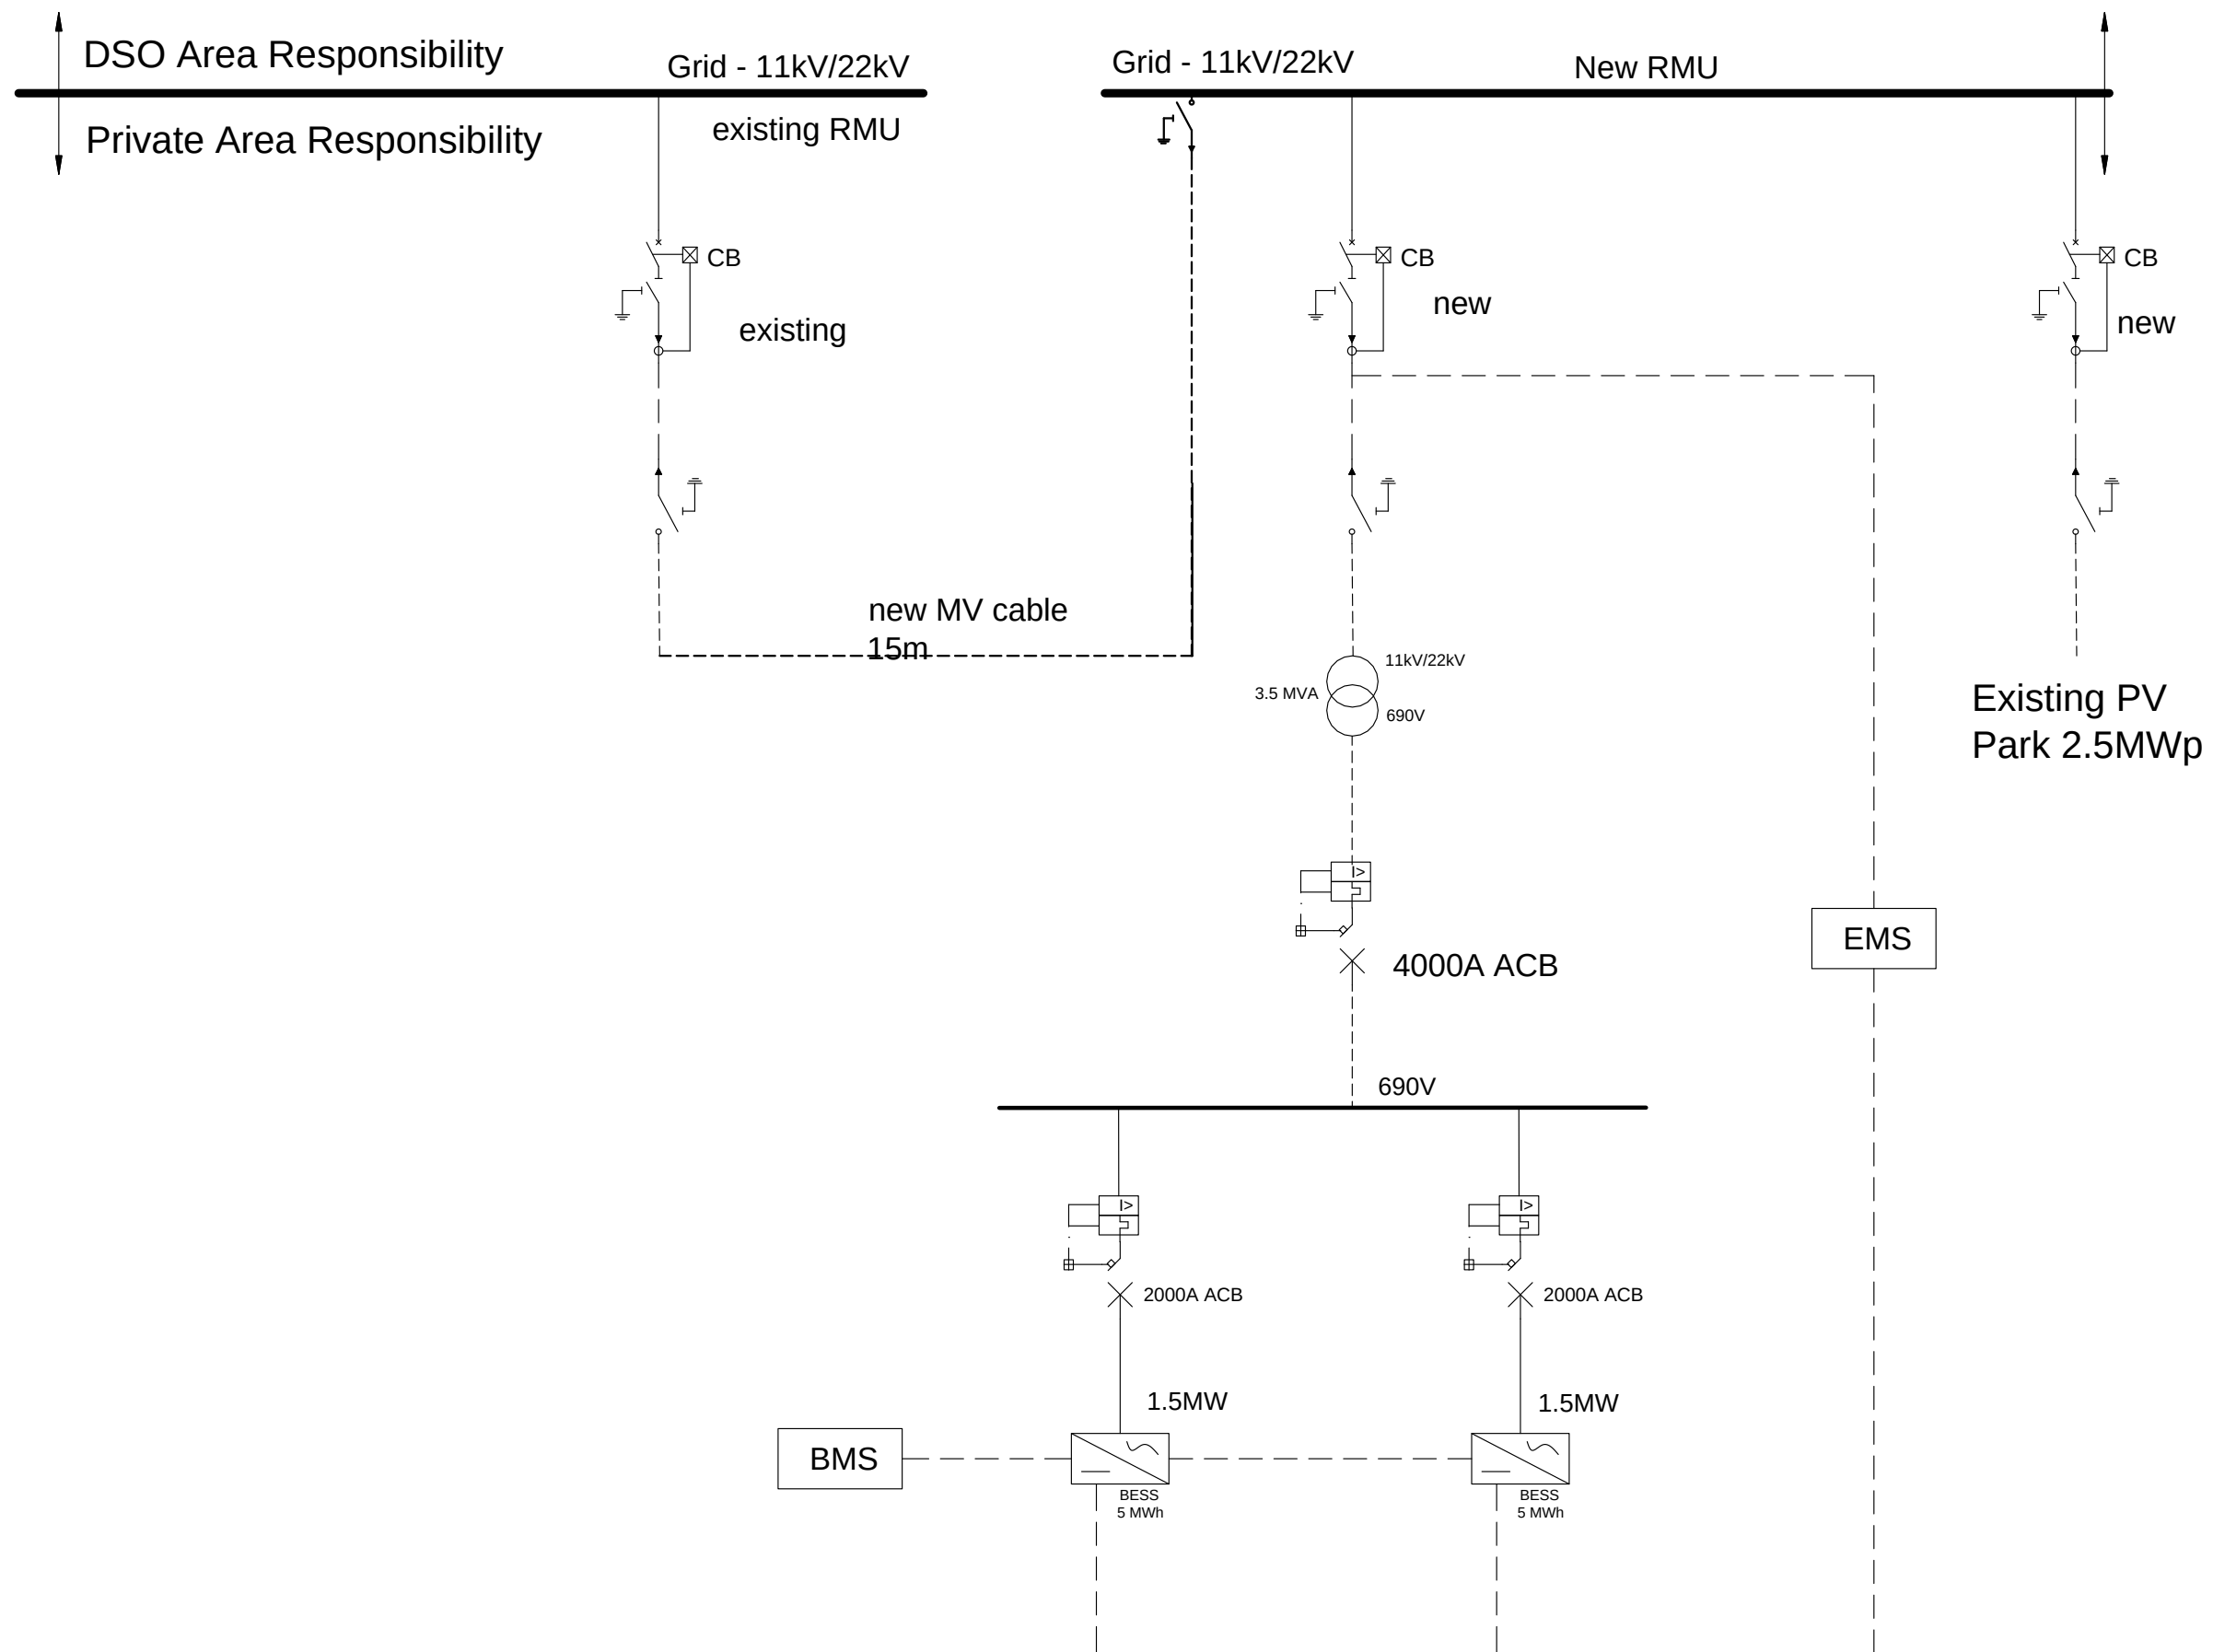

Project description: SOLARTECH 3 2.5MWp		Details: SOLARTECH 3 - BESS	
Design firm: Iacovos Charalambous		Design by: Iacovos Charalambous	Design date: 07/11/2025
Client: Abio Power LTD		Revision by:	Revision date: Sheet No.: