


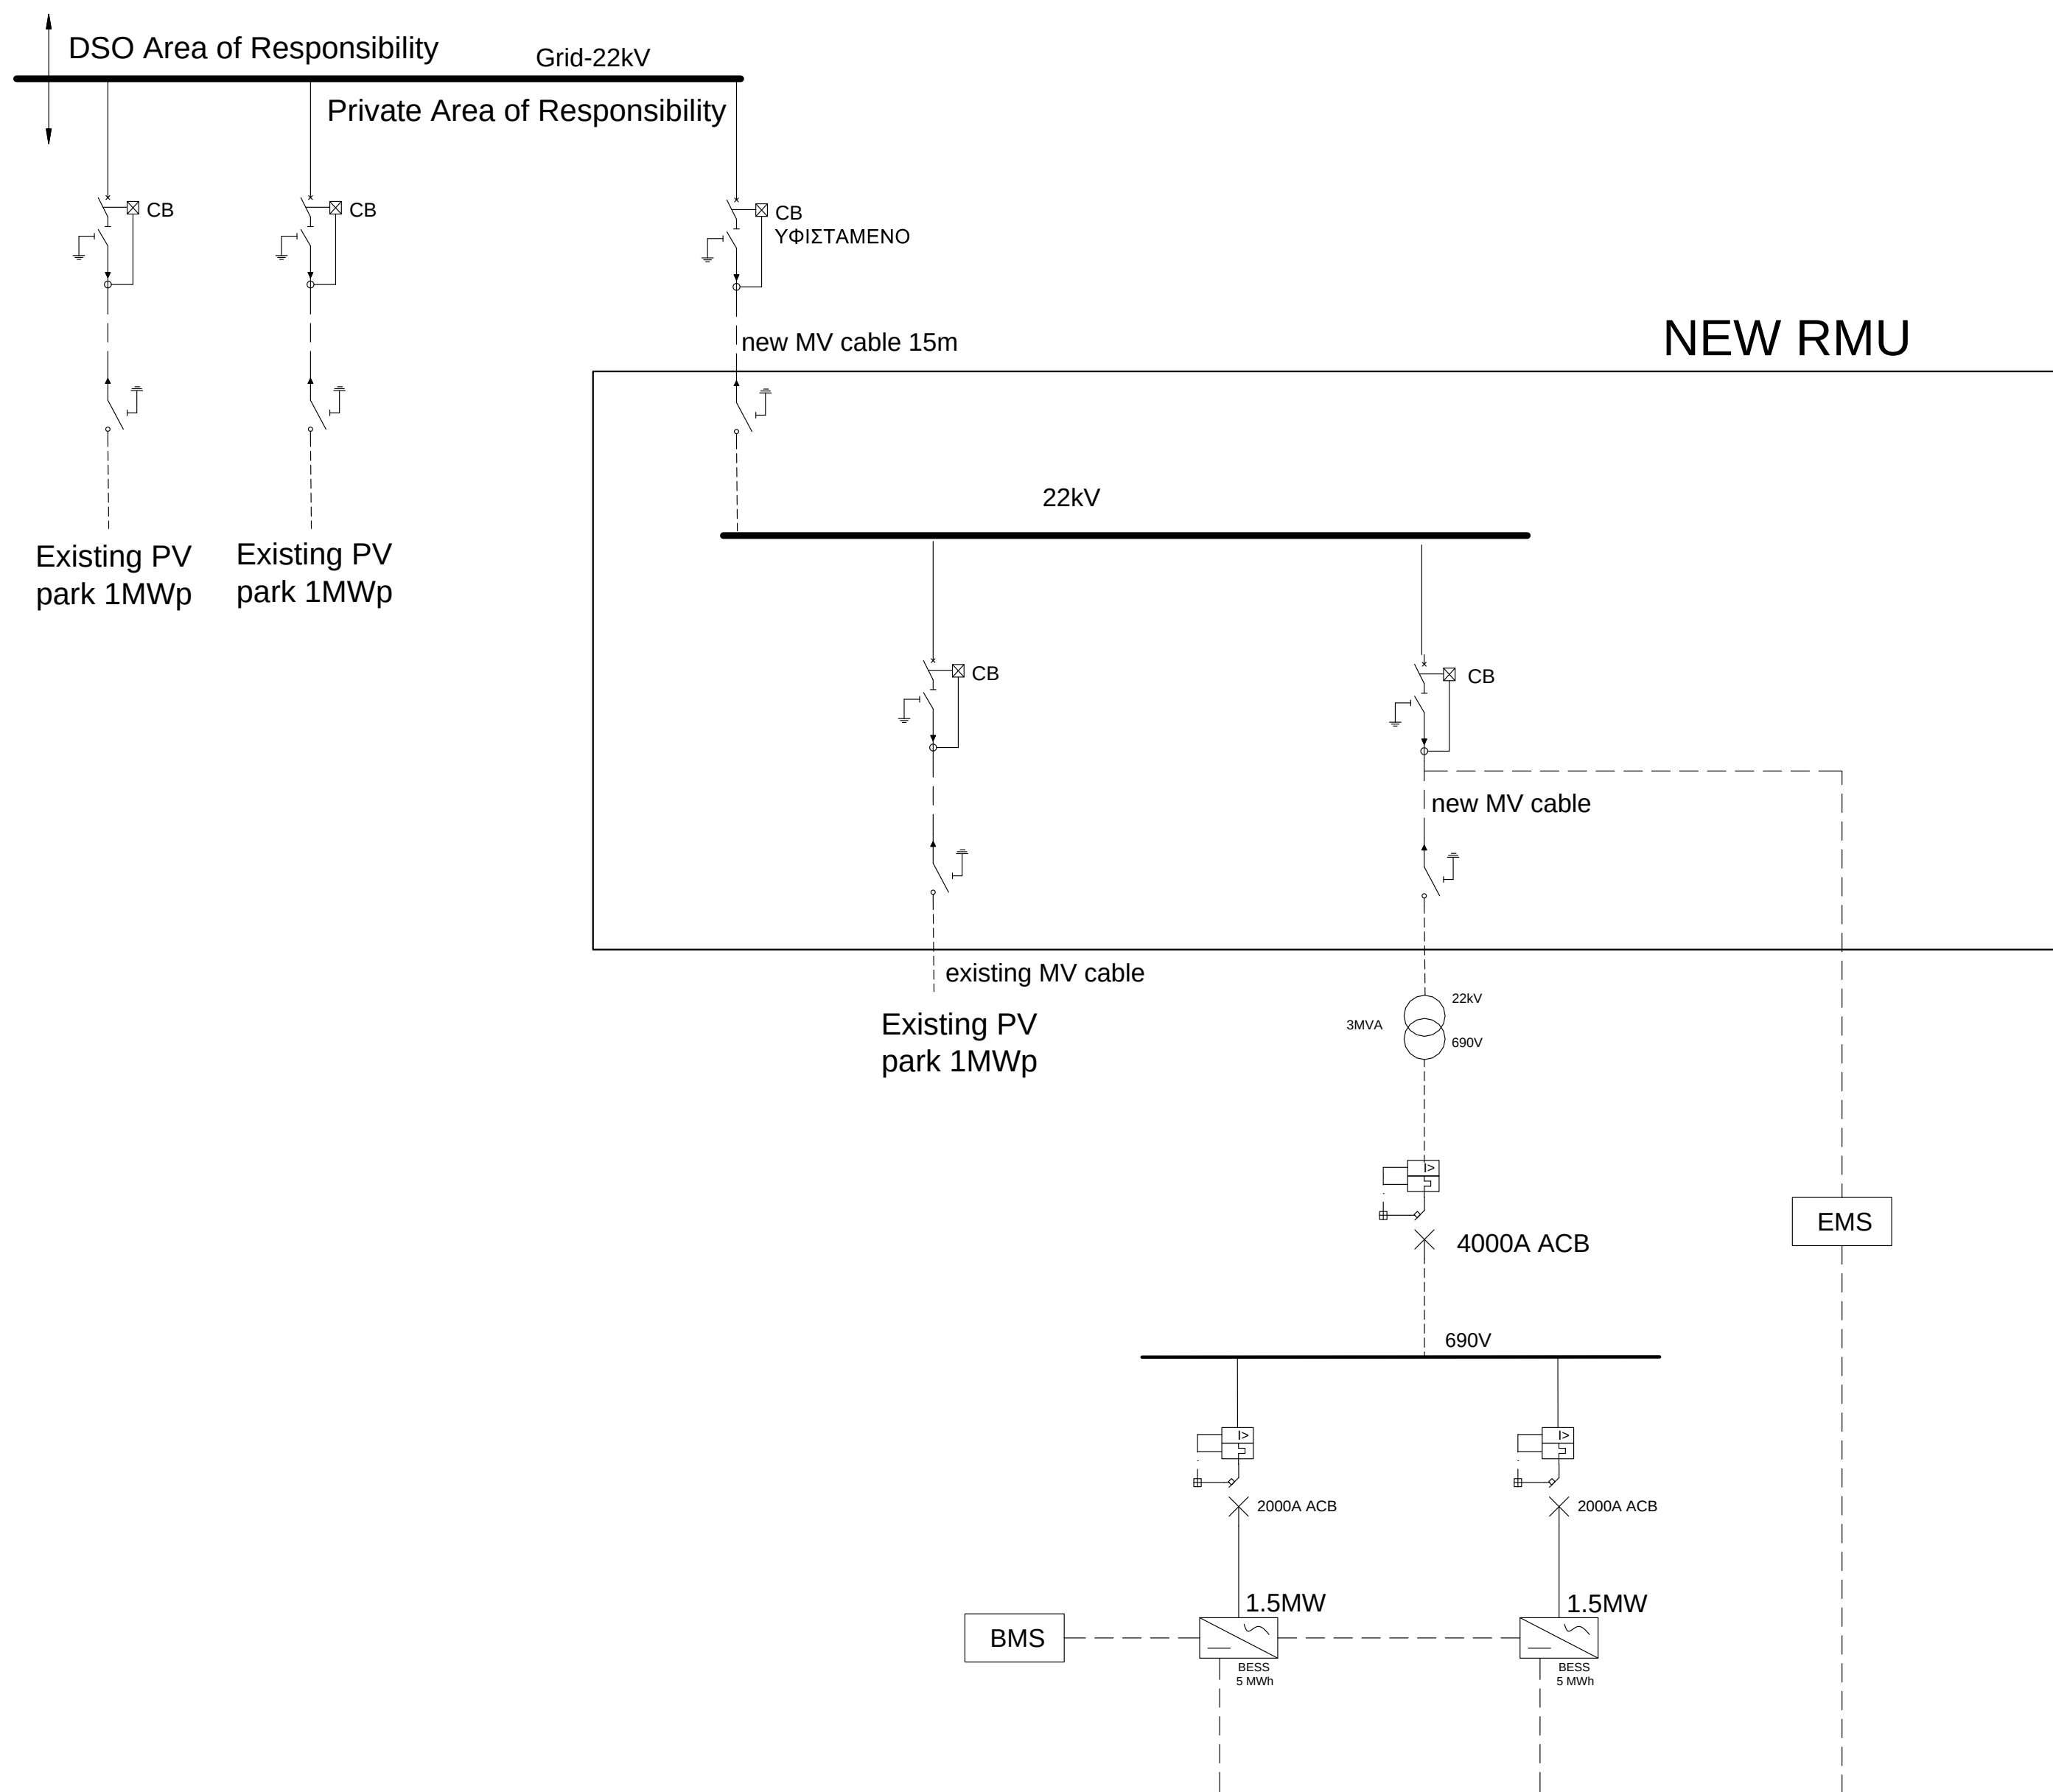

Project description:		Details:	
Waneron 3MWp		Waneron 3MWp - MV SLD Scale 1 : 75 @A2	
Design firm:		Design date:	
Iacovos Charalambous		10/12/2025	
Client:		Revision date:	
Abio Power LTD		Sheet No.:	



ELECTRICAL ENGINEERING
IACOVOΣ ΧΑΡΑΛΑΜΒΟΥΣ